


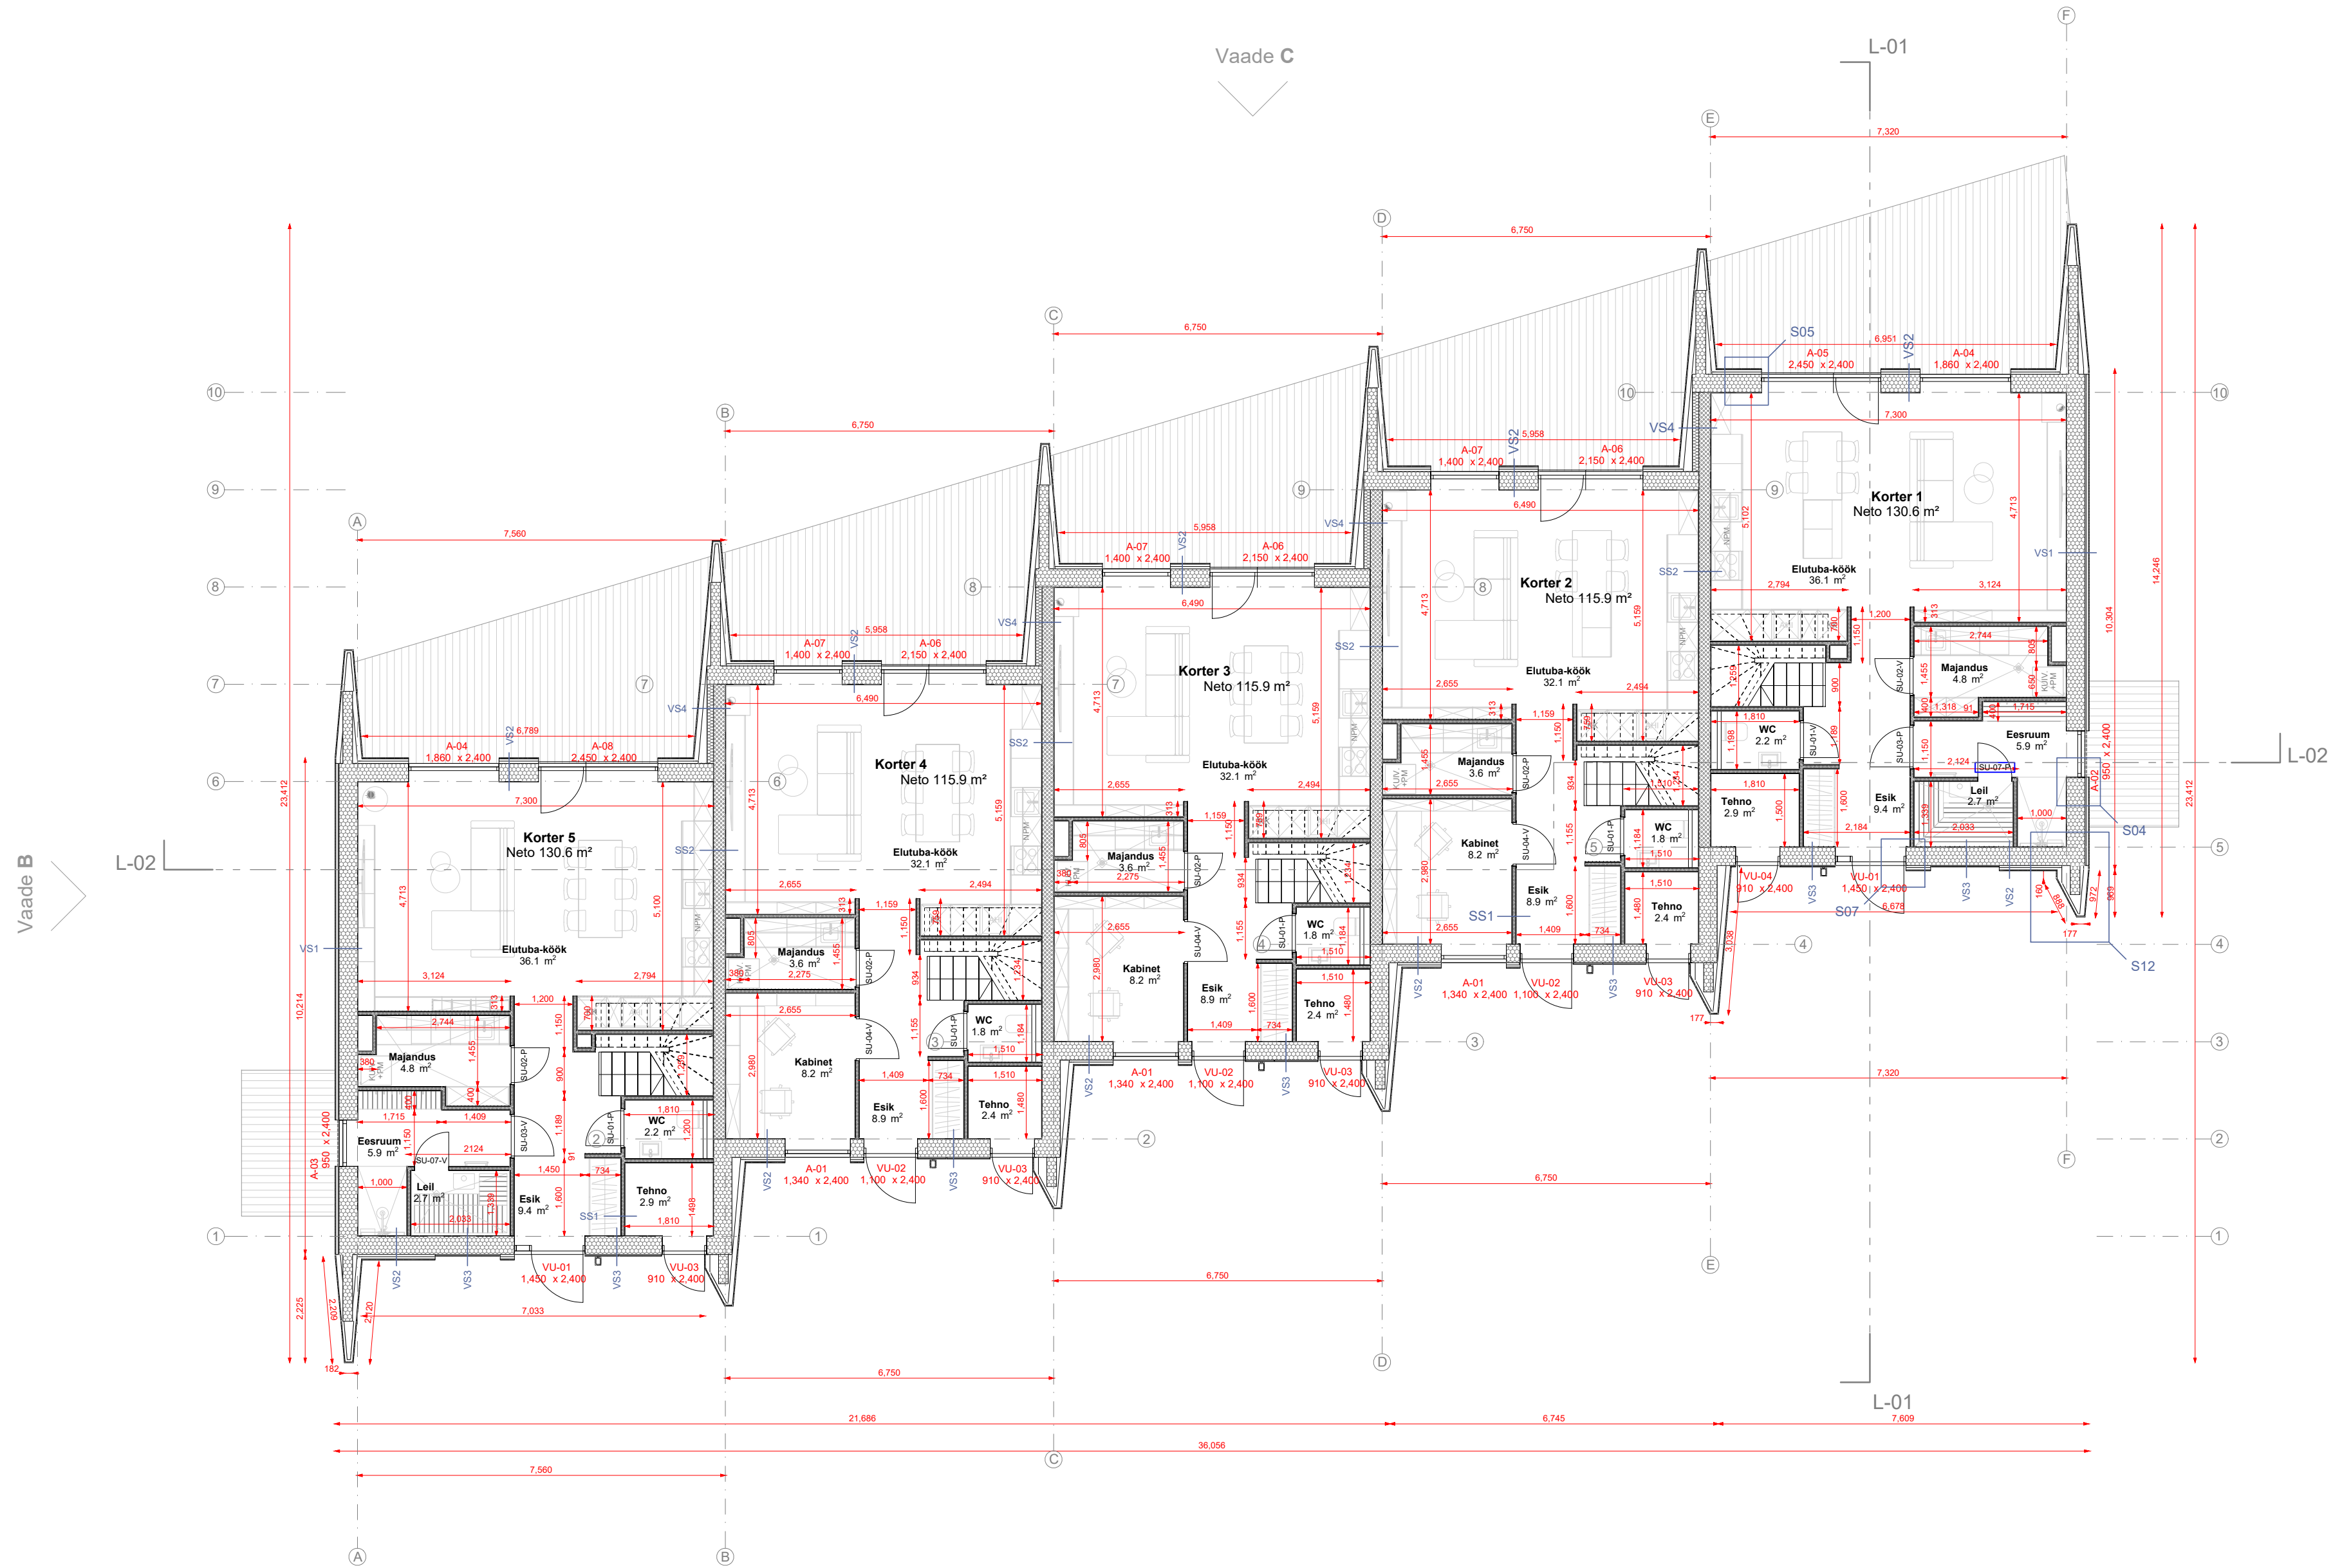

Objekt: Saku Ridaelamu
Address: Kuu tee 16, Komeedi 1, Komeedi 2, Saku alevik

1.KORRUS PÕHIPLAAN

Projekteeris: Eero Endjärv
Vastutava spetsialist: Eero Endjärv
Arhitekt11 OÜ, reg nr 12190827; Jõe 2/1, 10127 Tallinn, Eesti; info@arhitekt11.ee; KMKR EE101499183

Joonise nr: AR-5-01

Kuupäev: 27/08/2026
Mõõtkava: 1:100
Töö nr: A2
#Project ID
Projektis: Nele Soobik
+372 56619889; nele.sooibik@nobe.ee