


NB! Tulekaitsega võõbatud laudise ja tsementkiudplaadi puidust roovid immutada HolzProf HR Prof tulekaitsevõõbaga.

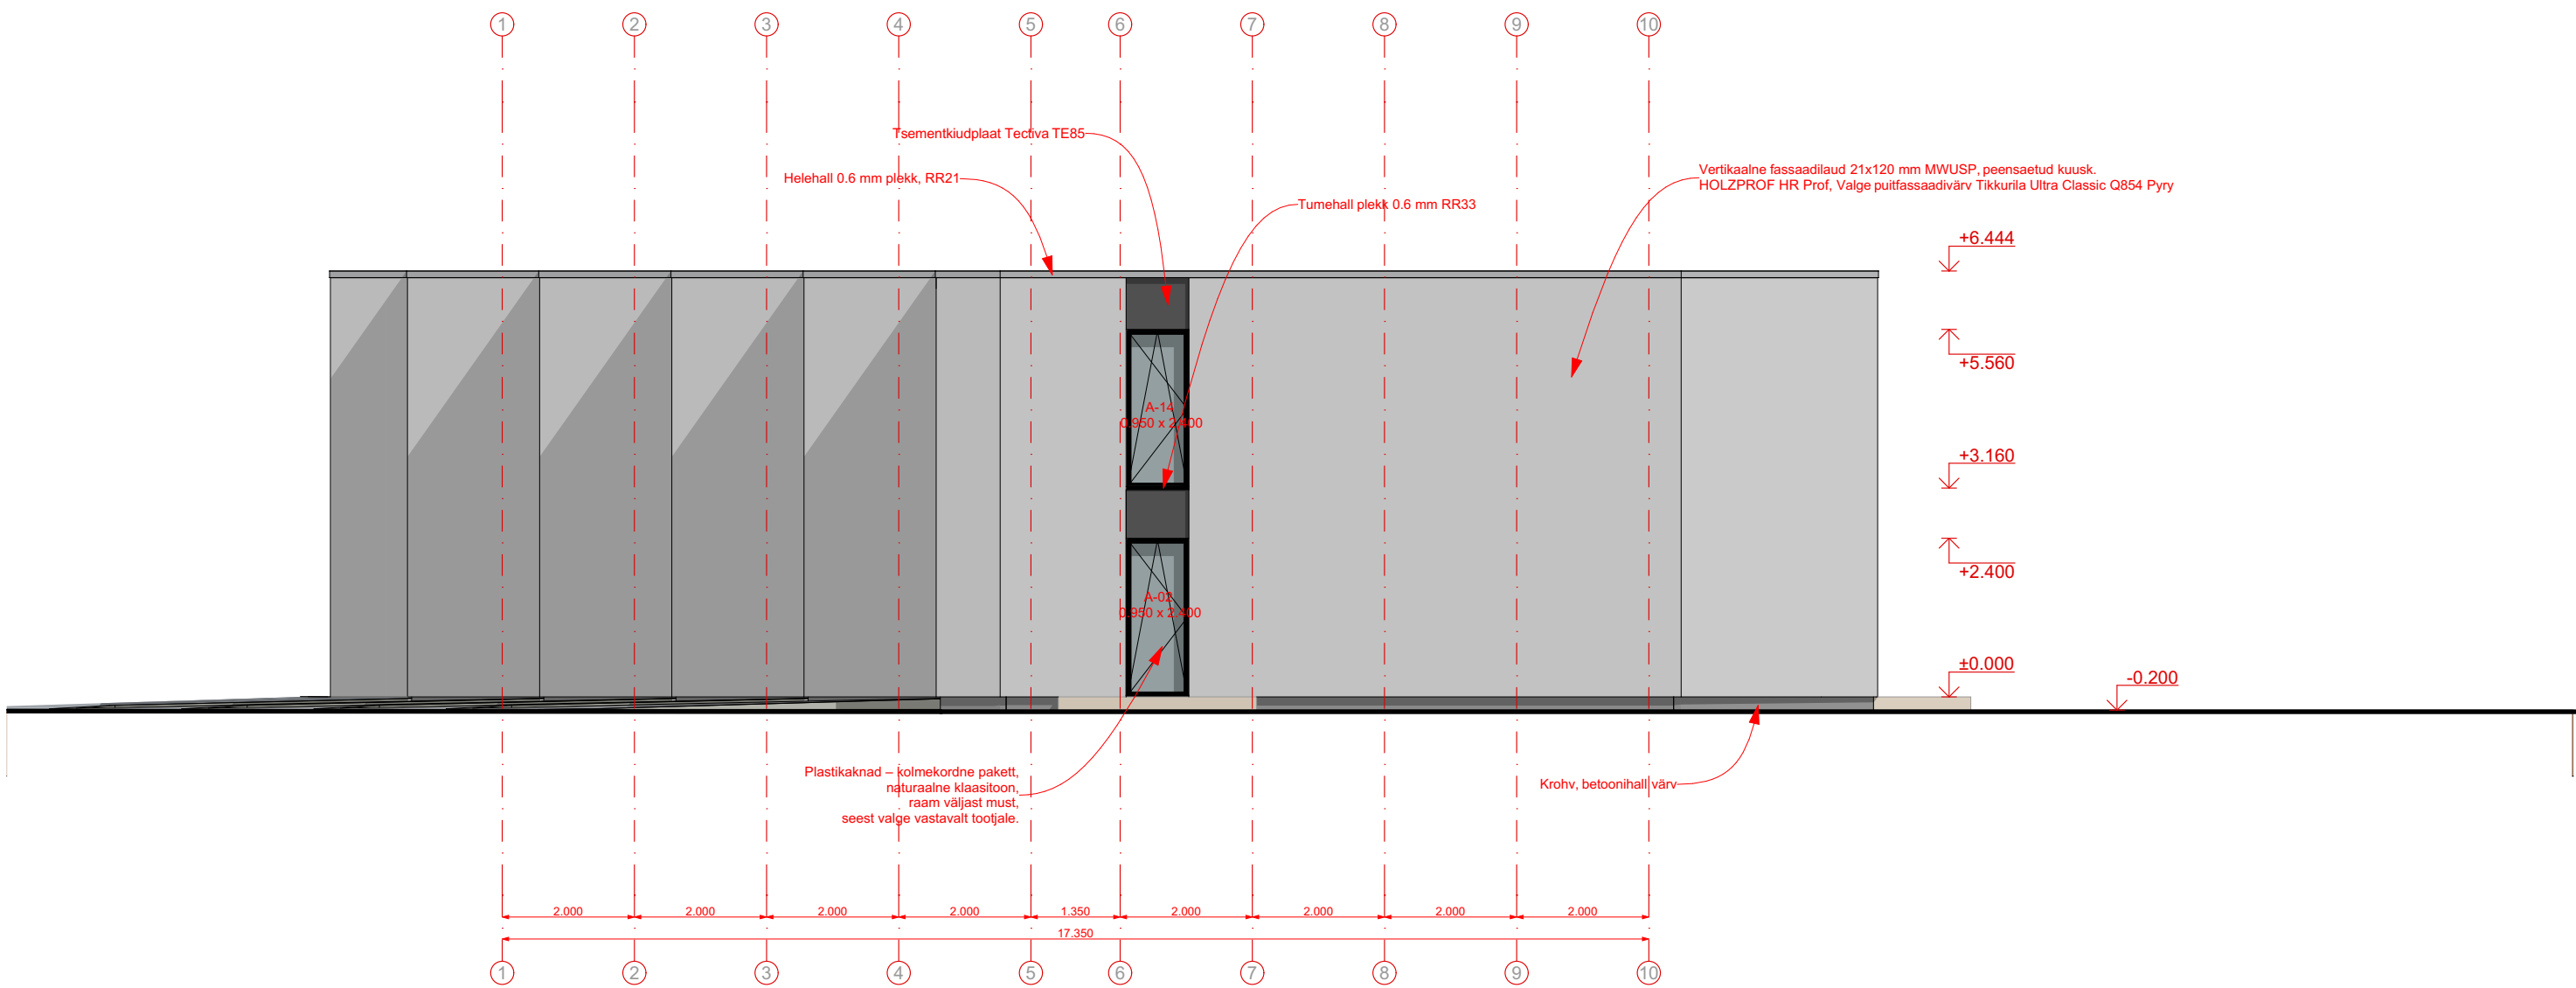

ARHITEKT 		Joonise nr:		AR-6-02	
Objekt:		Address:		Kuspilev:	
Saku Ridaelamu		Kuu tee 16, Komeedi 1, Komeedi 2, Saku alevik		23/05/2025	
Joonis:		Vastutav spetsialist:		01 - WIP	
Vaade B		Eero Endjärv		1:100	
Projekteeris:		Eero Endjärv		A2	
Arhitekt11 OÜ, reg nr 12190827, Jõe 2/1, 10127 Tallinn, Eesti; info@arhitekt11.ee; KMKR EE101499183		Projektijuh:		PP	
		Eero Endjärv		#Project ID	
				Projektijuh:	
				Nele Soobik	
				+372 56619889; nele.soobik@nobe.ee	