


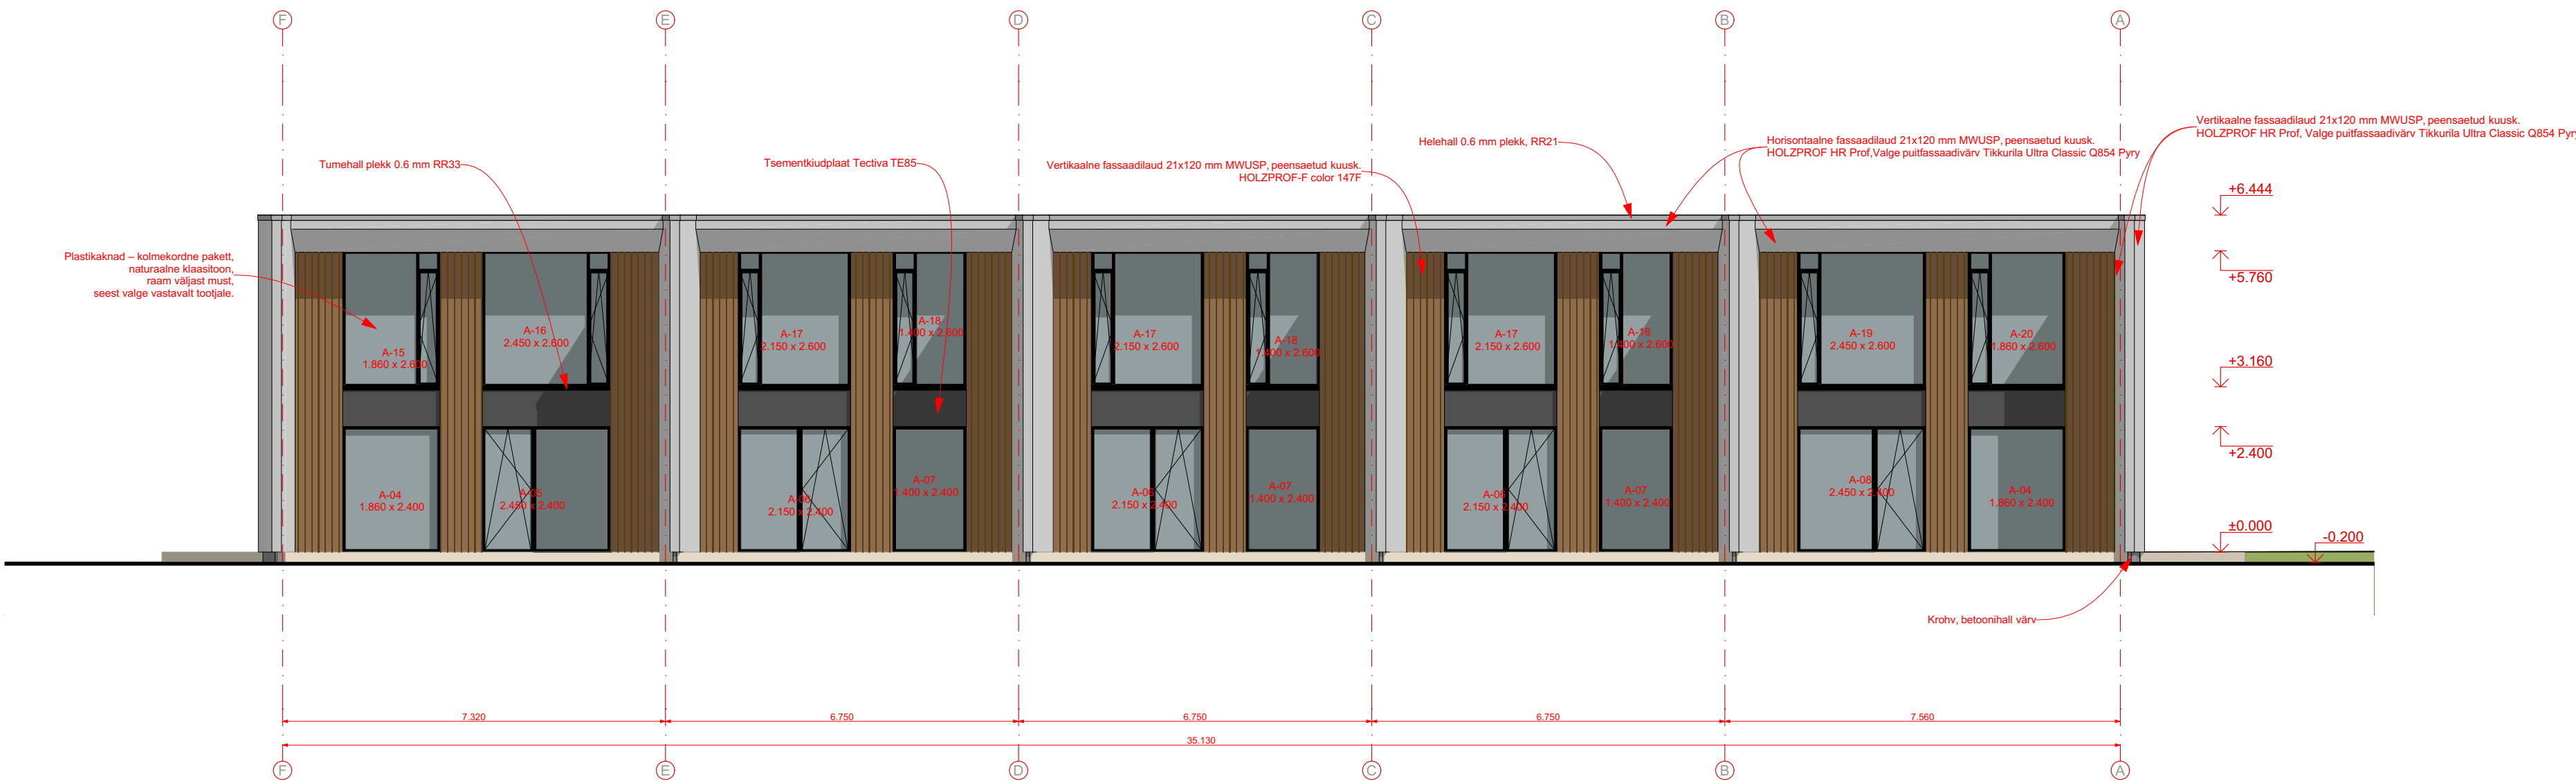

NB! Tulekaitsega võõbatud laudise ja tsementkiudplaadi puidust roovid immutada HolzProf HR Prof tulekaitsevõõbaga.

ARHITEKT 

Objekt:
Saku Ridaelamu

Address:
Kuu tee 16, Komeedi 1, Komeedi 2, Saku alevik

Joonis:
Vaade C

Projekts: Eero Endjärv

Vastutav spetsialist:
Eero Endjärv

Arhitekt11 OÜ, reg nr 12190827, Jõe 2/1, 10127 Tallinn, Eesti; info@arhitekt11.ee; KMKR EE101499183

Joonise nr:
AR-6-03

Kuupäev:
23/05/2025

01 - WIP

Mõõtkava:
1:100

A2

PP

Töö nr:
#Project ID

Projekti juht:
Nele Soobik

+372 56619889; nele.sobik@nobe.ee