


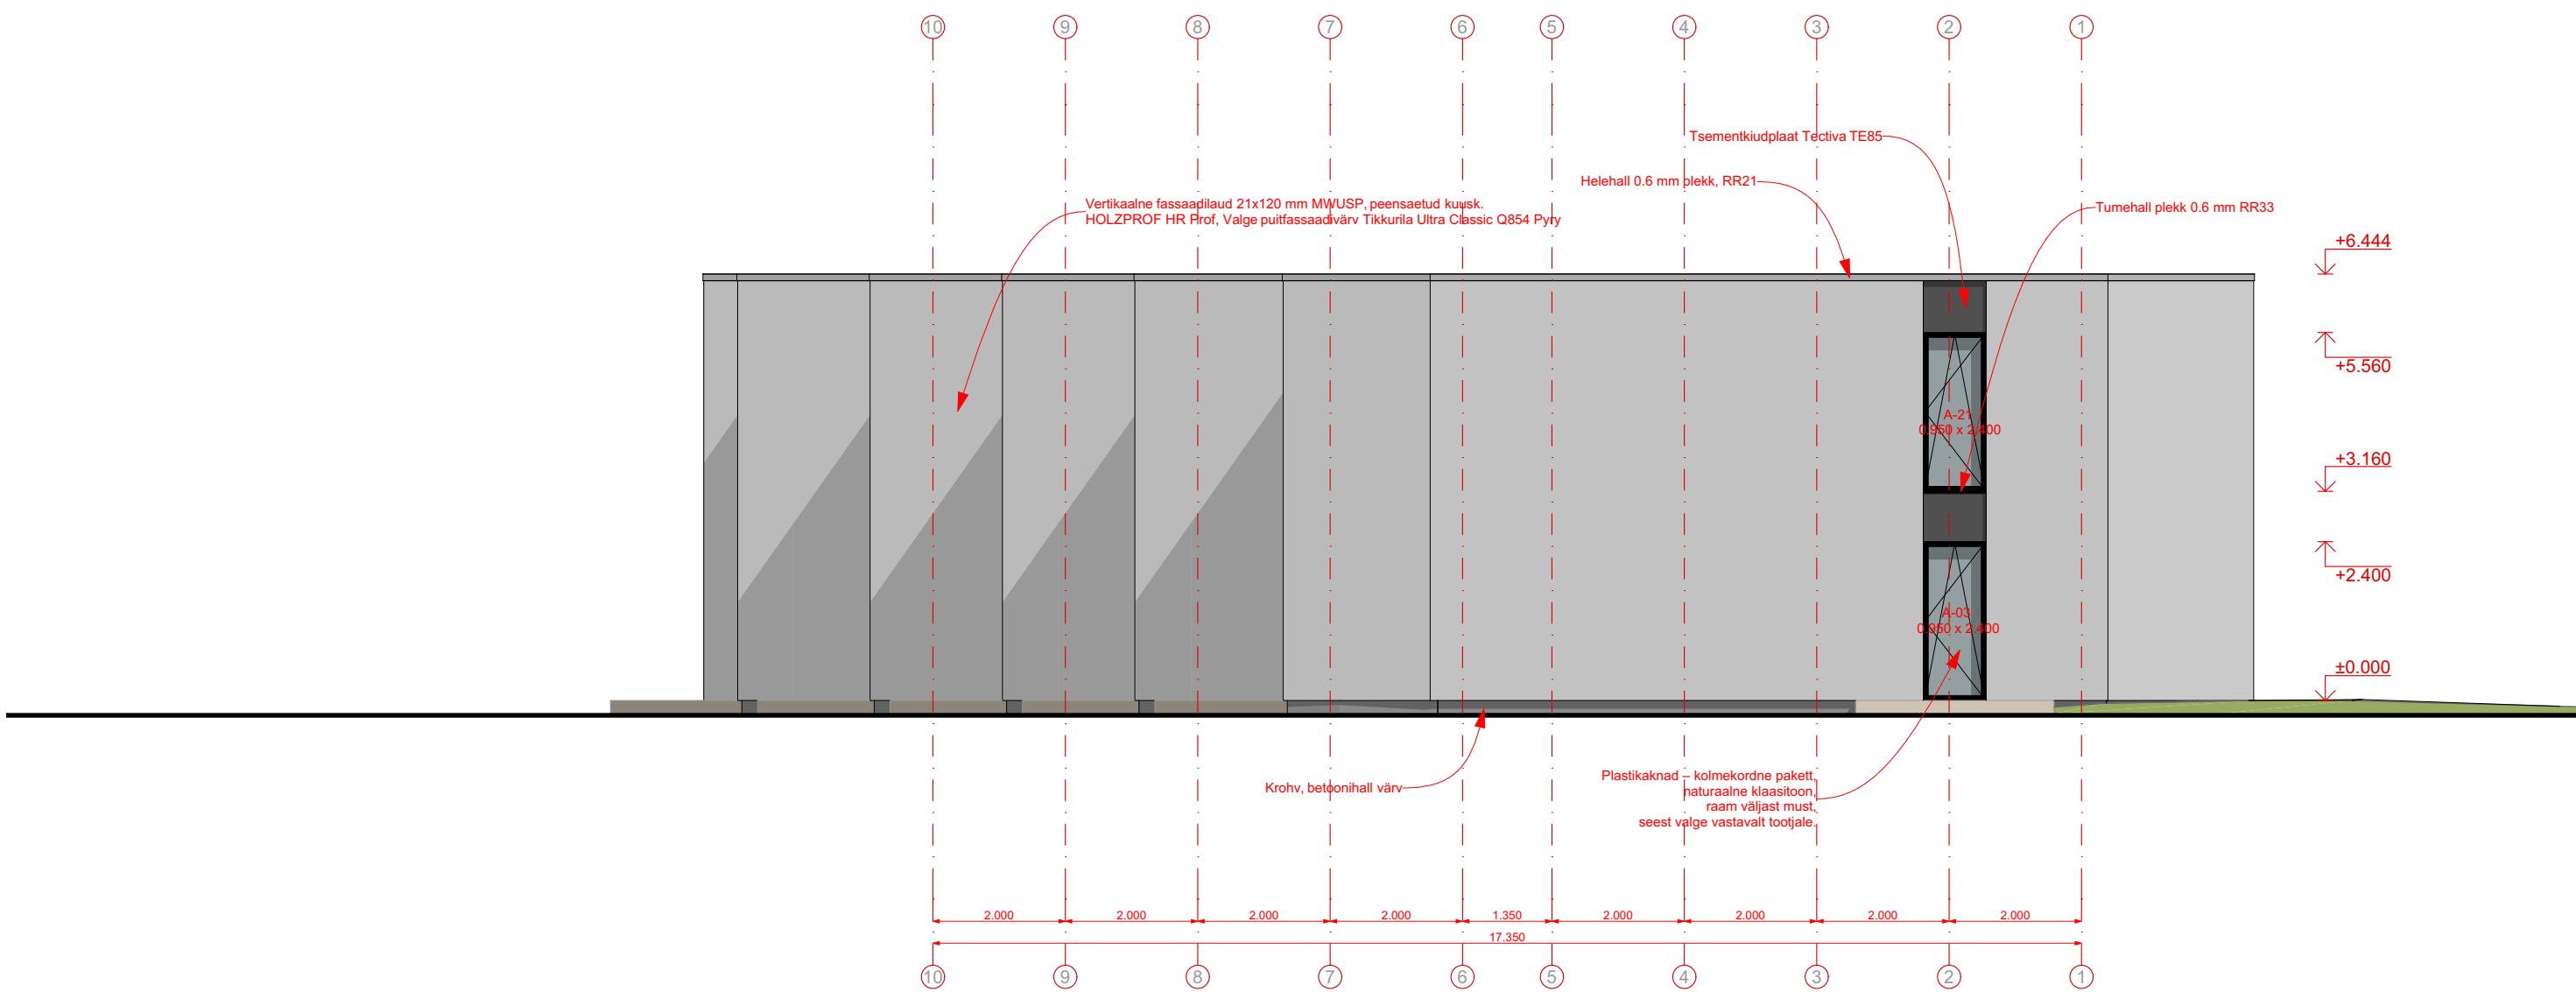

**NB!** Tulekaitsega võõbatud laudise ja tsementkiudplaadi puidust roovid immutada HolzProf HR Prof tulekaitsevõõbaga.

|   |  |                                               |  |                                    |    |
|---|--|-----------------------------------------------|--|------------------------------------|----|
| ARHITEKT       |  | Joonise nr:                                   |  | AR-6-04                            |    |
| Objekt:                                                                                             |  | Address:                                      |  | Kuspilev:                          |    |
| Saku Ridaelamu                                                                                      |  | Kuu tee 16, Komeedi 1, Komeedi 2, Saku alevik |  | 23/05/2025                         |    |
| Joonis:                                                                                             |  | Vastutav spetsialist:                         |  | 01 - WIP                           |    |
| Vaade D                                                                                             |  | Eero Endjärv                                  |  | Mõõtkava:                          |    |
| Projekteeris:                                                                                       |  | Eero Endjärv                                  |  | 1:100                              | A2 |
| Arhitekt11 OÜ, reg nr 12190827, Jõe 2/1, 10127 Tallinn, Eesti; info@arhitekt11.ee; KMKR EE101499183 |  | Projektijuh:                                  |  |                                    | PP |
|   |  | Nele Soobik                                   |  | #Project ID                        |    |
|   |  |                                               |  | +372 56619889; nele.soobik@nobe.ee |    |