


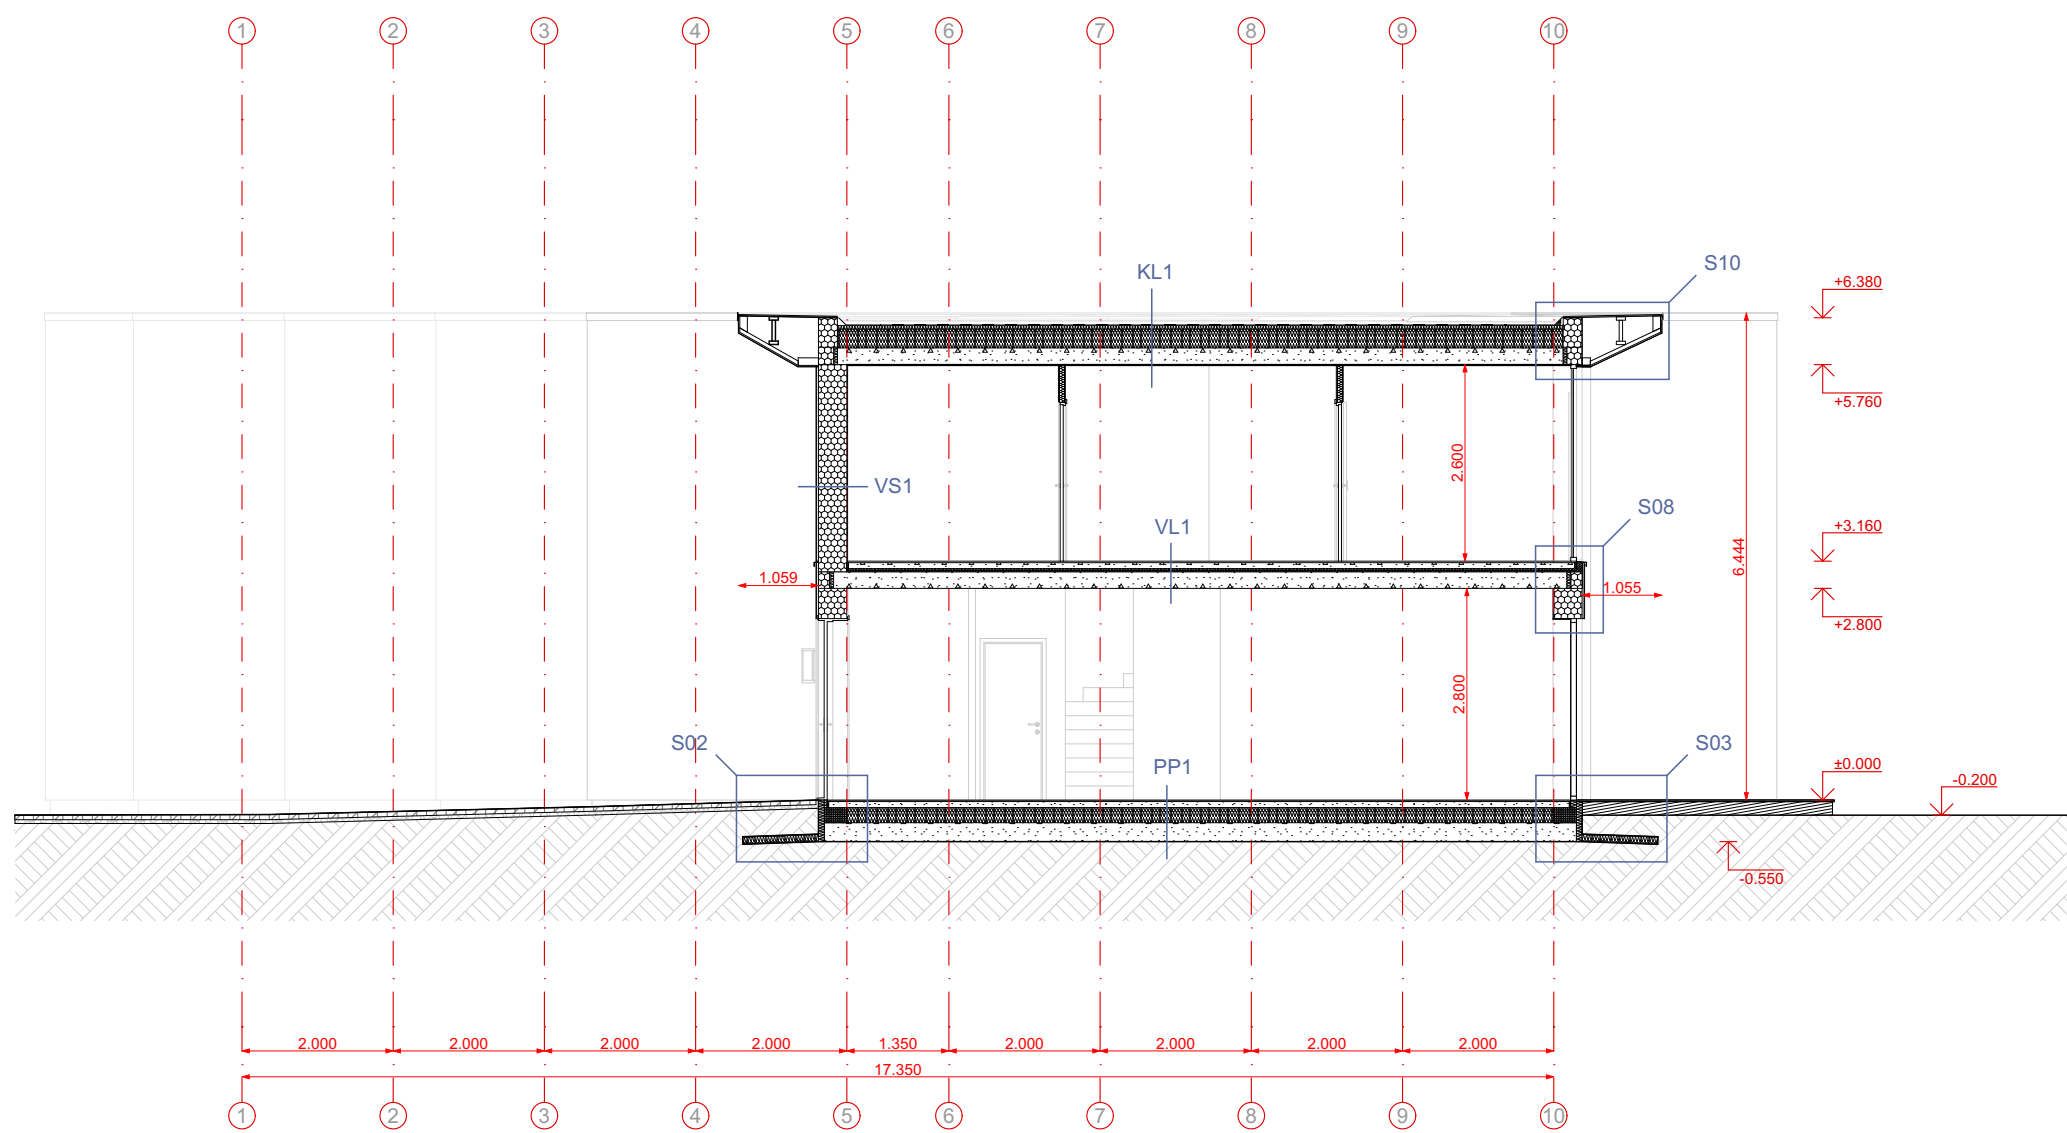

ARHITEKT 

Objekt:
Saku Ridaelamu

Address:
Kuu tee 16, Komeedi 1, Komeedi 2, Saku alevik

Joonis:
Lõige S-01

Projekts: Eero Endjäär

Vastutav spetsialist:
Eero Endjäär

Arhitekt11 OÜ, reg nr 12190827, Jõa 2/1, 10127 Tallinn, Eesti; info@arhitekt11.ee; KMKR EE101499183

Joonise nr:

AR-6-05

Kuupäev:
02/04/2025

01 - WIP

Mõõtkava:

1:100

A2

PP

Töö nr:

#Project ID

Projekti juht:

Nele Soobik

+372 56619889; nele.soobik@nobe.ee