


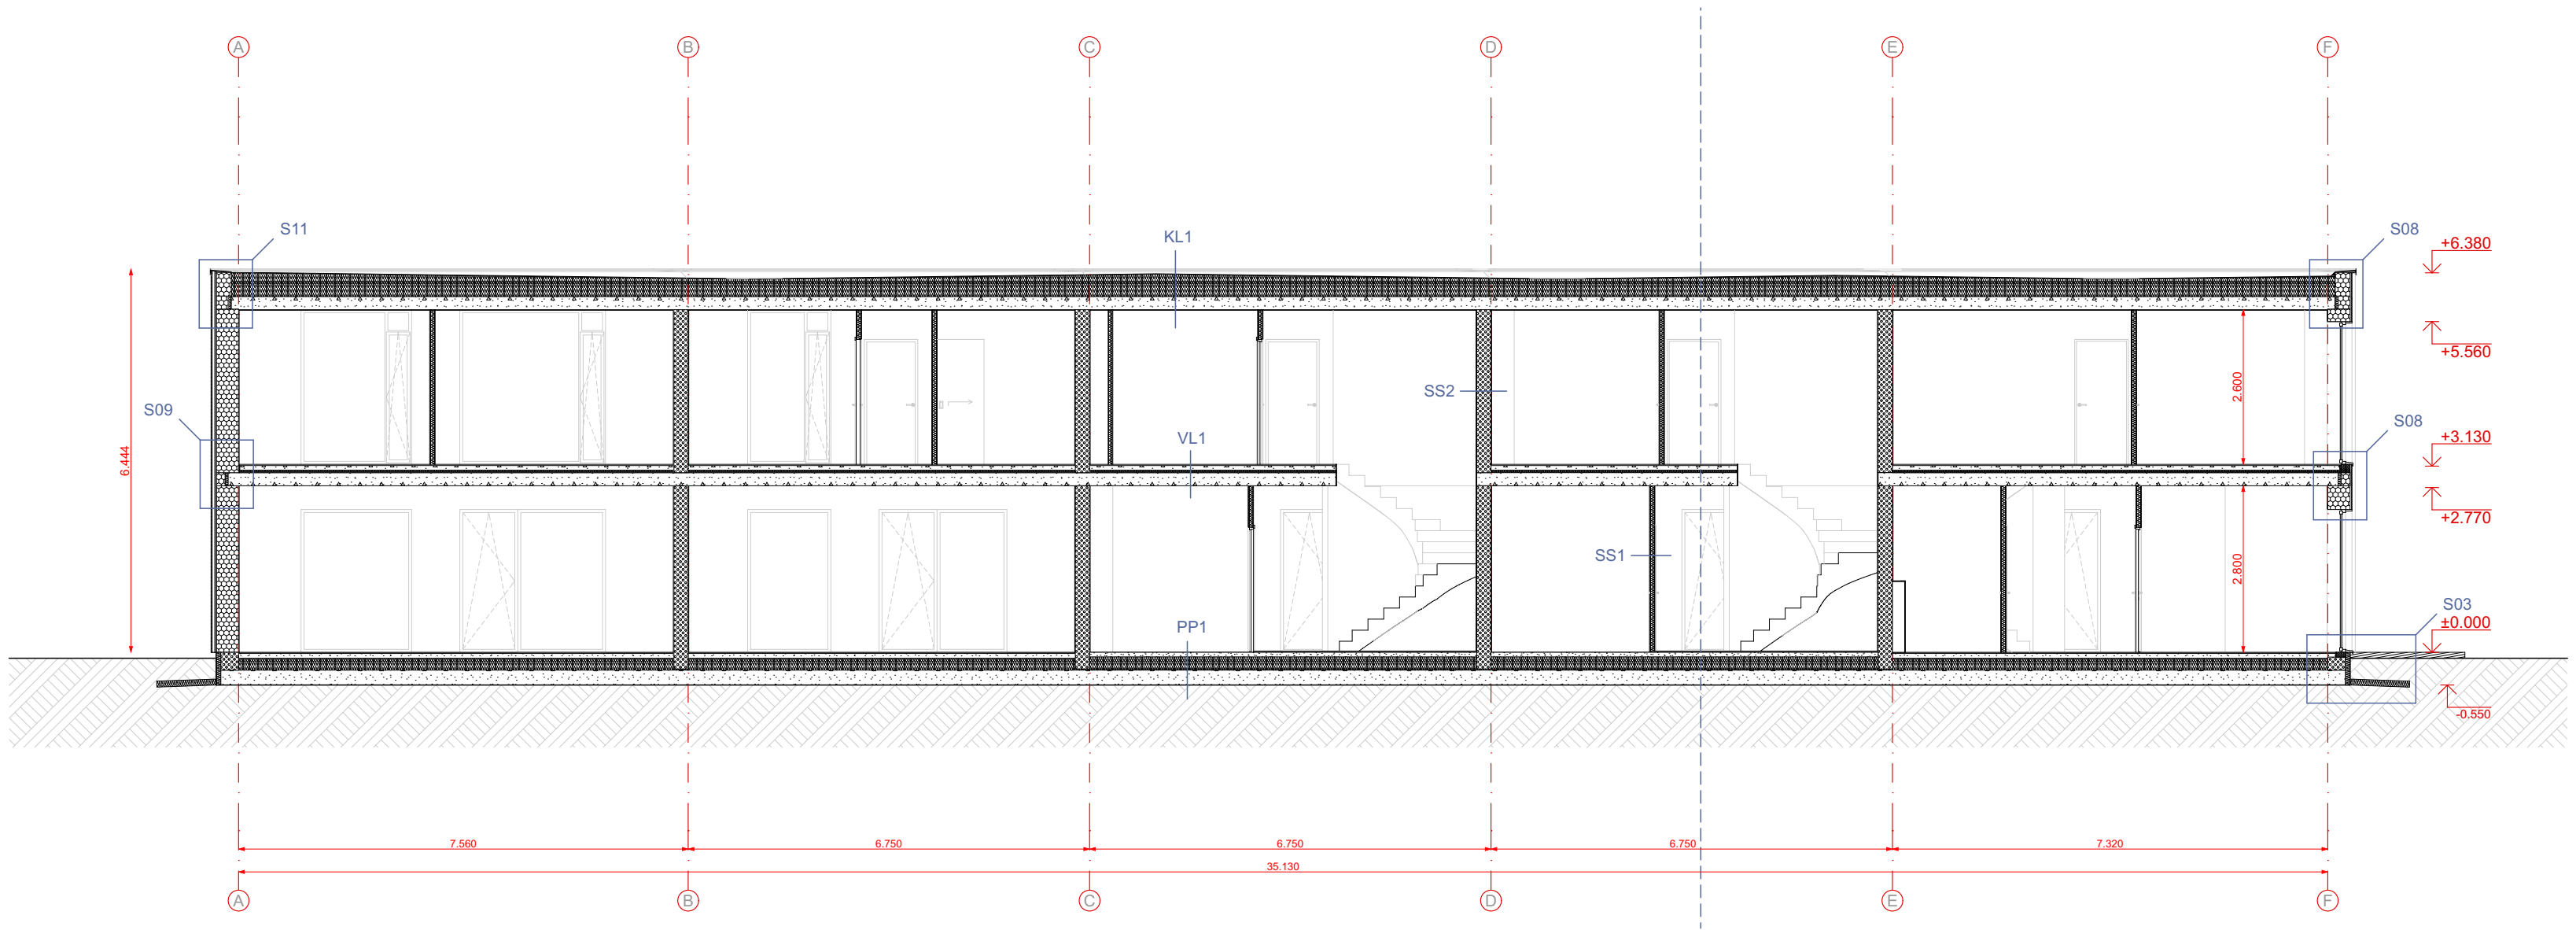

ARHITEKT 

Objekt:
Saku Ridaelamu

Address:
Kuu tee 16, Komeedi 1, Komeedi 2, Saku alevik

Joonis:

Lõige S-02

Projekts: Eero Endjäv

Arhitekt11 OÜ, reg nr 12190827, Jõe 2/1, 10127 Tallinn, Eesti; info@arhitekt11.ee; KMKR EE101499183

Vastutav spetsialist:

Eero Endjäv

Joonise nr:

AR-6-06

Kuupäev:

02/04/2025

Mõõtkava:

1:100

Töö nr:

#Project ID

Projektant:

Nele Soobik

+372 56619889; nele.soobik@nobe.ee

01 - WIP

A2

PP