


NB! Sissepääsuvoolsete seinte fassaadilaudad ja roovid immutatud tulekaitsevõõbaga! vt. vaatepöörnis.

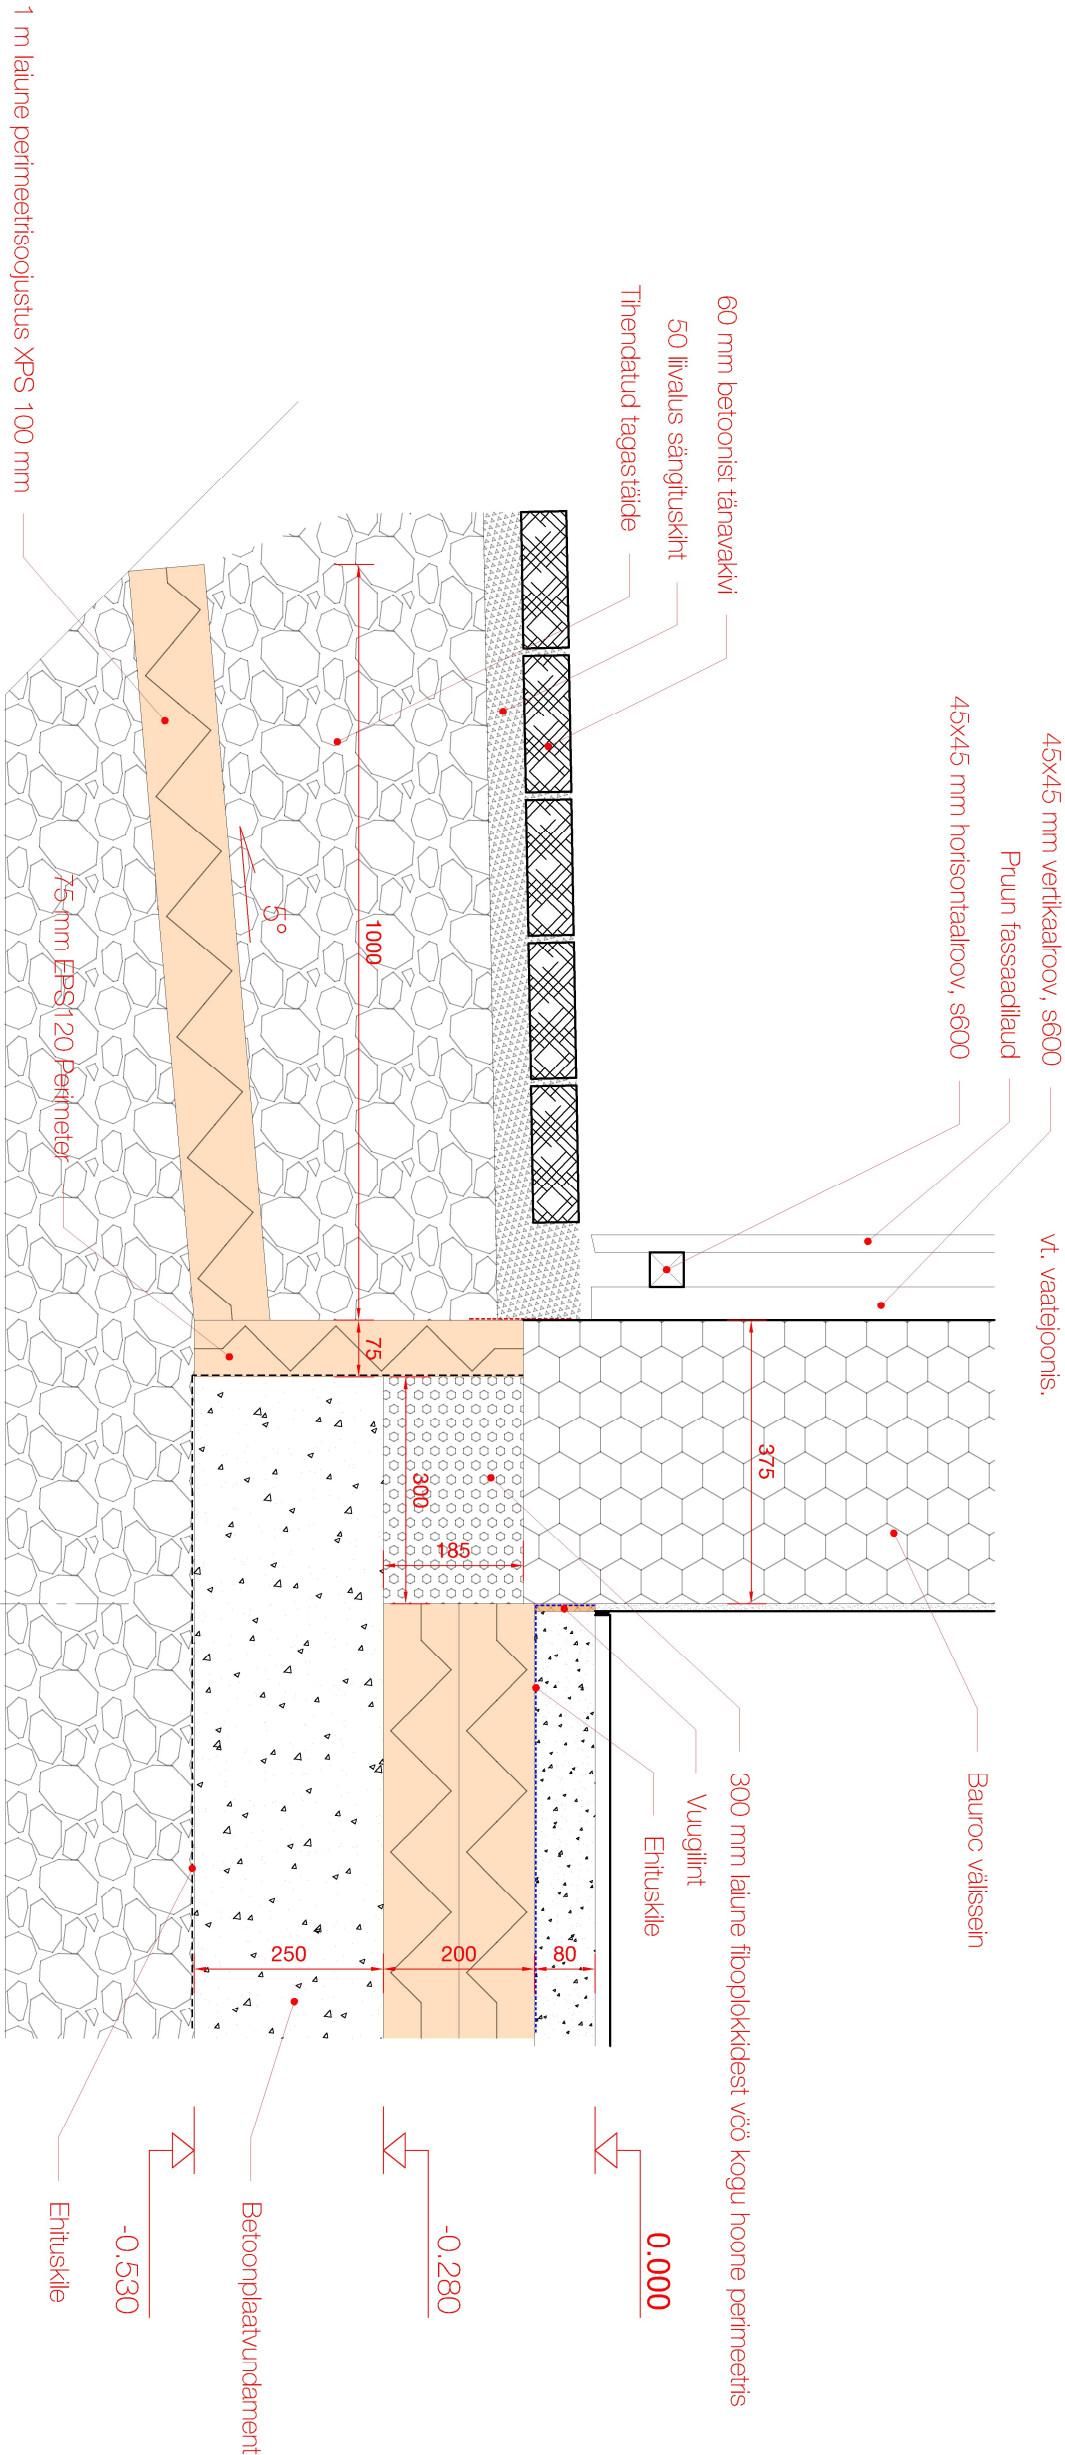

ARHITEKT



Objekt:	Saku Ridaelamu	Address:	Kuu tee 16, Komeedi 1, Komeedi 2, Saku alevik
Joonis:			

S01 Soklisõlm (hoone esine sein)

Projekteeris:	E.Endjärv	Vastutav arhitekt:	E.Endjärv
Arhitekti 1 OÜ, reg nr 12190827, Jõa 2/1, 10127 Tallinn, ESTONIA, info@arhitekti1.ee; KMKR EE101499183			

Joonise nr.

AR-7-01

Kuupäev:	23/05/2025	
Mõõtkava:	1:10; A3	PP
Töö nr:	---	

Projekti juht:	Nele Soobik
mele.sobik@nobe.ee	
+372 566 19 889	