


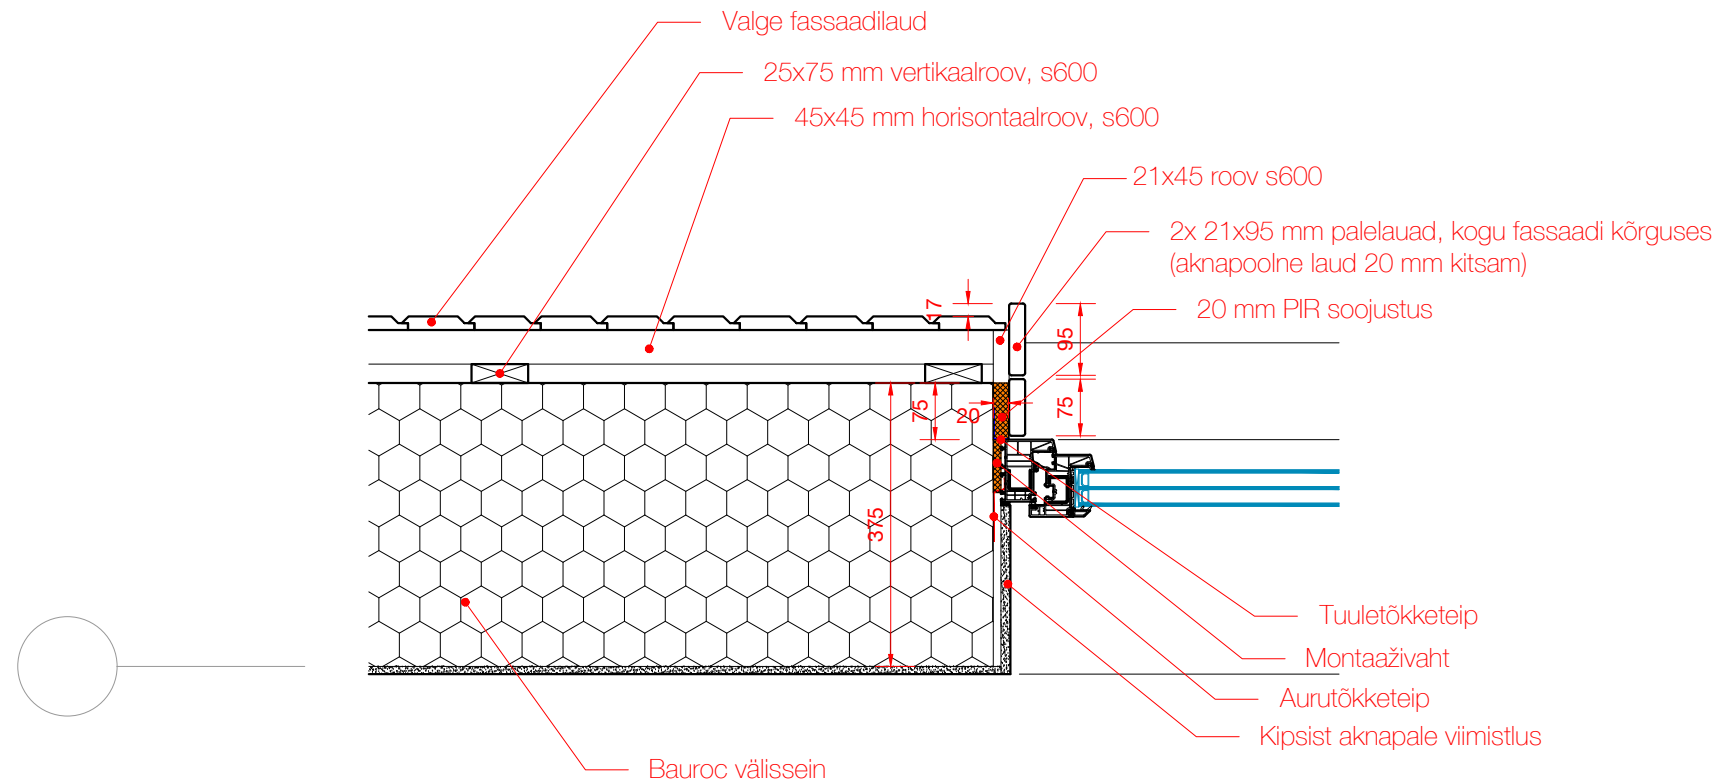

ARHITEKT 

Objekt: Saku Ridaelamu Aadress: Kuu tee 16, Komeedi 1, Komeedi 2, Saku alevik

Joonis: **S04 Aknapale** (valge laudisega sein)

Projekteeris: E.Endjärv Vastutav arhitekt: E.Endjärv

Arhitekt11 OÜ, reg nr 12190827, Joa 2/1, 10127 Tallinn, ESTONIA, info@arhitekt11.ee; KMKR EE101499183

Joonise nr. **AR-7-04**

Kuupäev: 31/03/2025

Mõõtkava: 1:10; A3 PP

Töö nr: ---

Projekti juht:
Nele Soobik

mele.soobik@nobe.ee
+372 566 19 889