


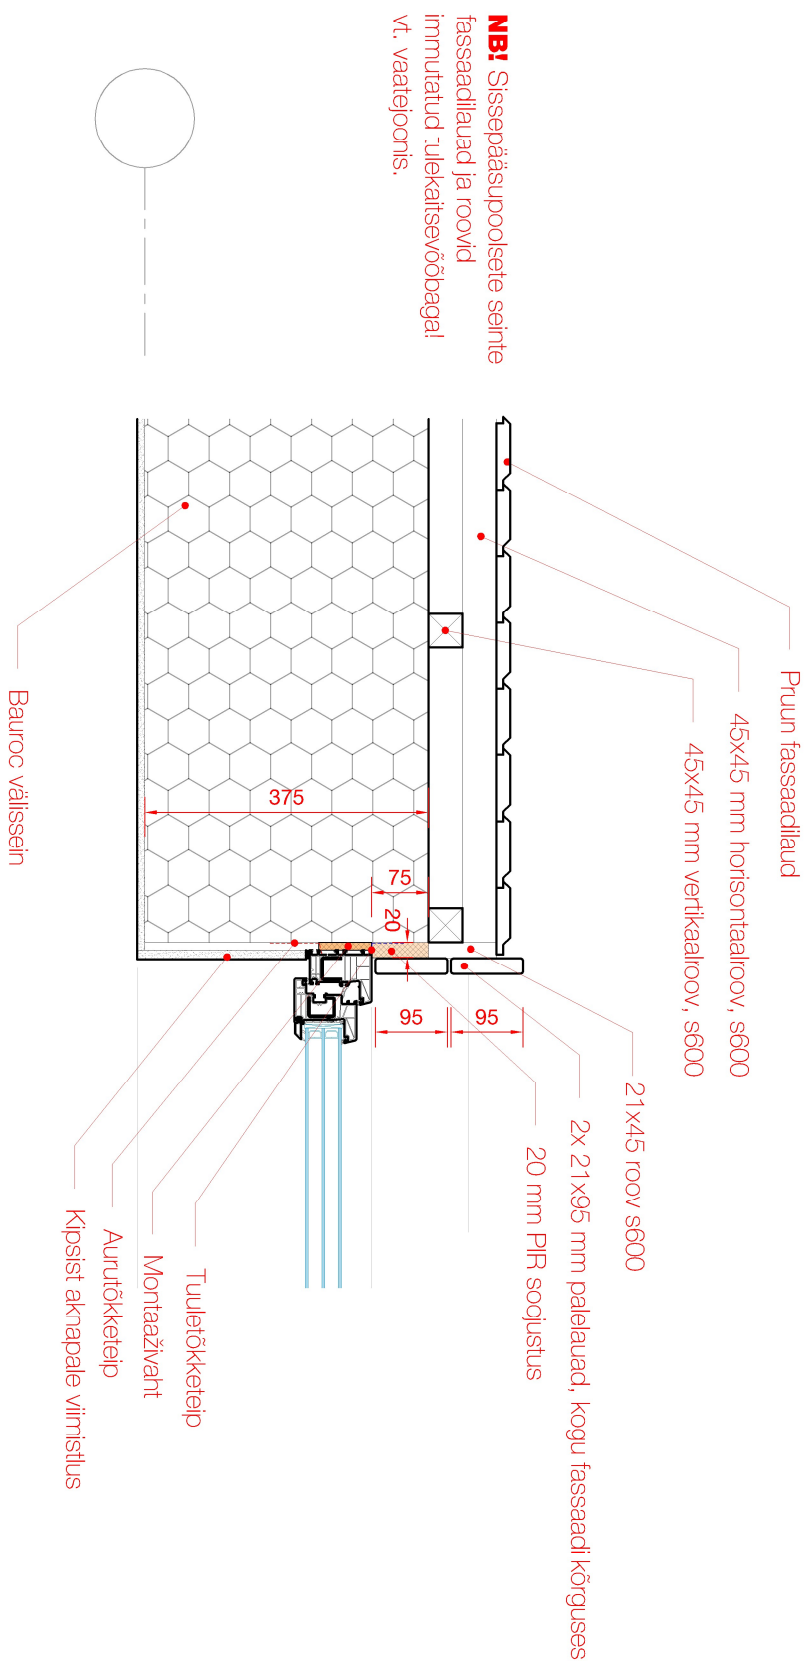

ARHITEKT

Objekt:	Saku Ridaelamu	Address:	Kuu tee 16, Komeedi 1, Komeedi 2, Saku alevik	Kuupäev:	23/05/2025
Joonis:	S05 Aknapale (tumedalauisega sein)			Mõõtkava:	1:10; A3
				Töö nr:	---
					PP