


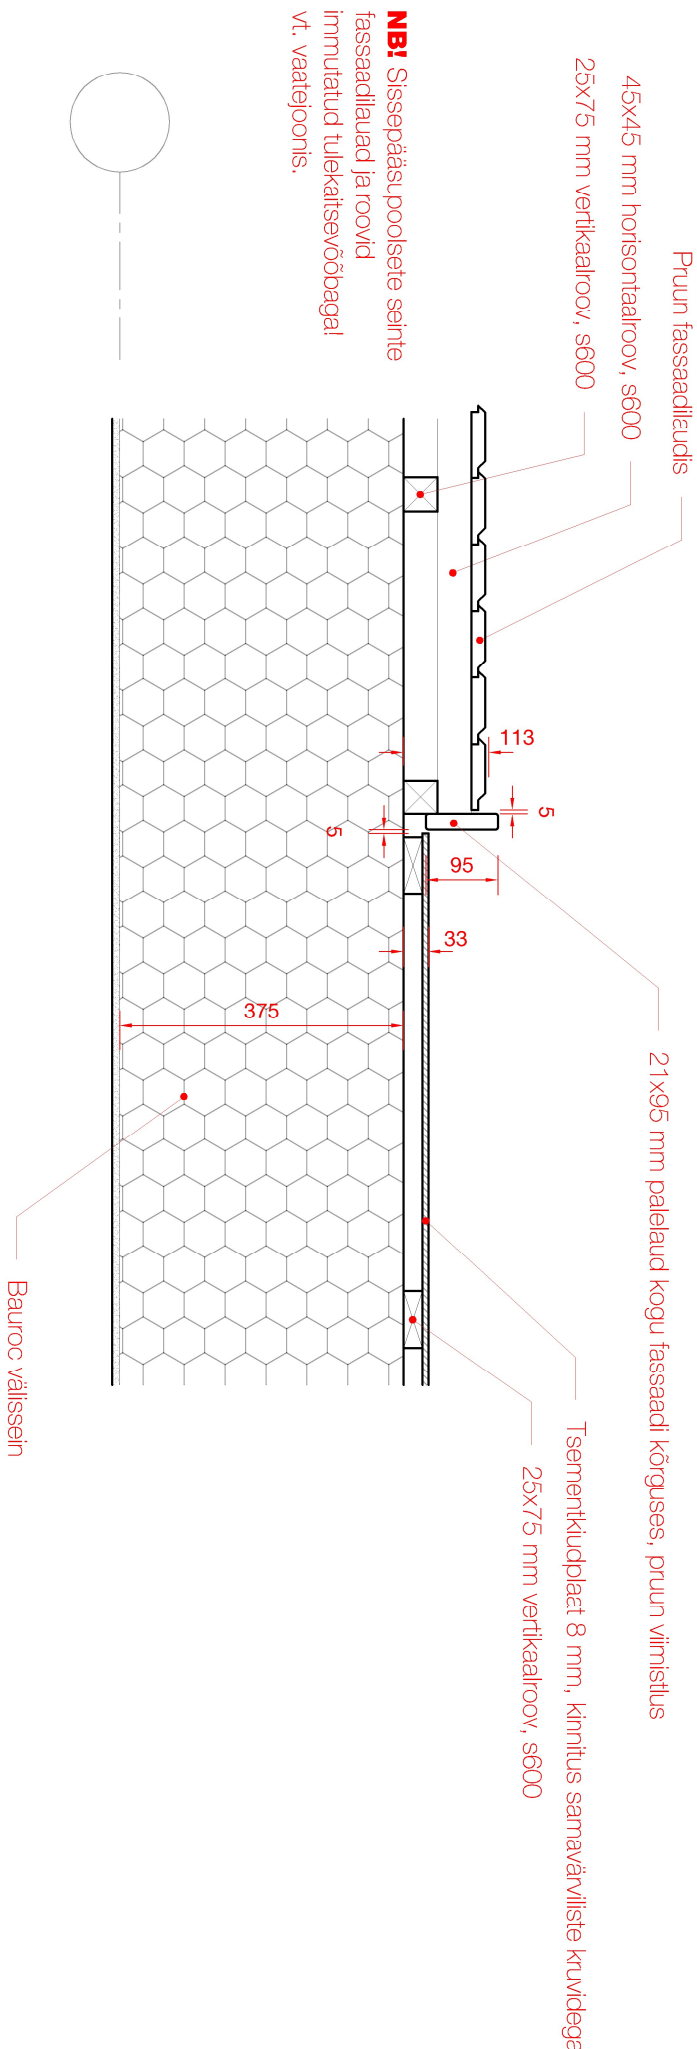

ARHITEKT



Joonise nr.

AR-7-07

Objekt: Saku Ridaelamu

Address:

Kuu tee 16, Komeedi 1, Komeedi 2, Saku alevik

Joonis:

Kuupäev: 23/05/2025

Mõõtkava: 1:10; A3

PP

S07 Seinadetail (tsementplaadi ja laudise liitumine)

Projekteeris: E.Endjärv

Vastutav arhitekt:

E.Endjärv

Projekti juht:

Nelle Soobik

Arhitekt 1 OÜ, reg nr 12190827, Jõa 2/1, 10127 Tallinn, ESTONIA, info@arhitekt1.ee; KMKR EE101499183

nnelle.sobik@nobe.ee

+372 566 19 889