


NB! Sissepääsupoolsete seinte
fassaadilauad ja roovid
immutatud tulekaitsevööbaga!
vt. vaatejoonis.

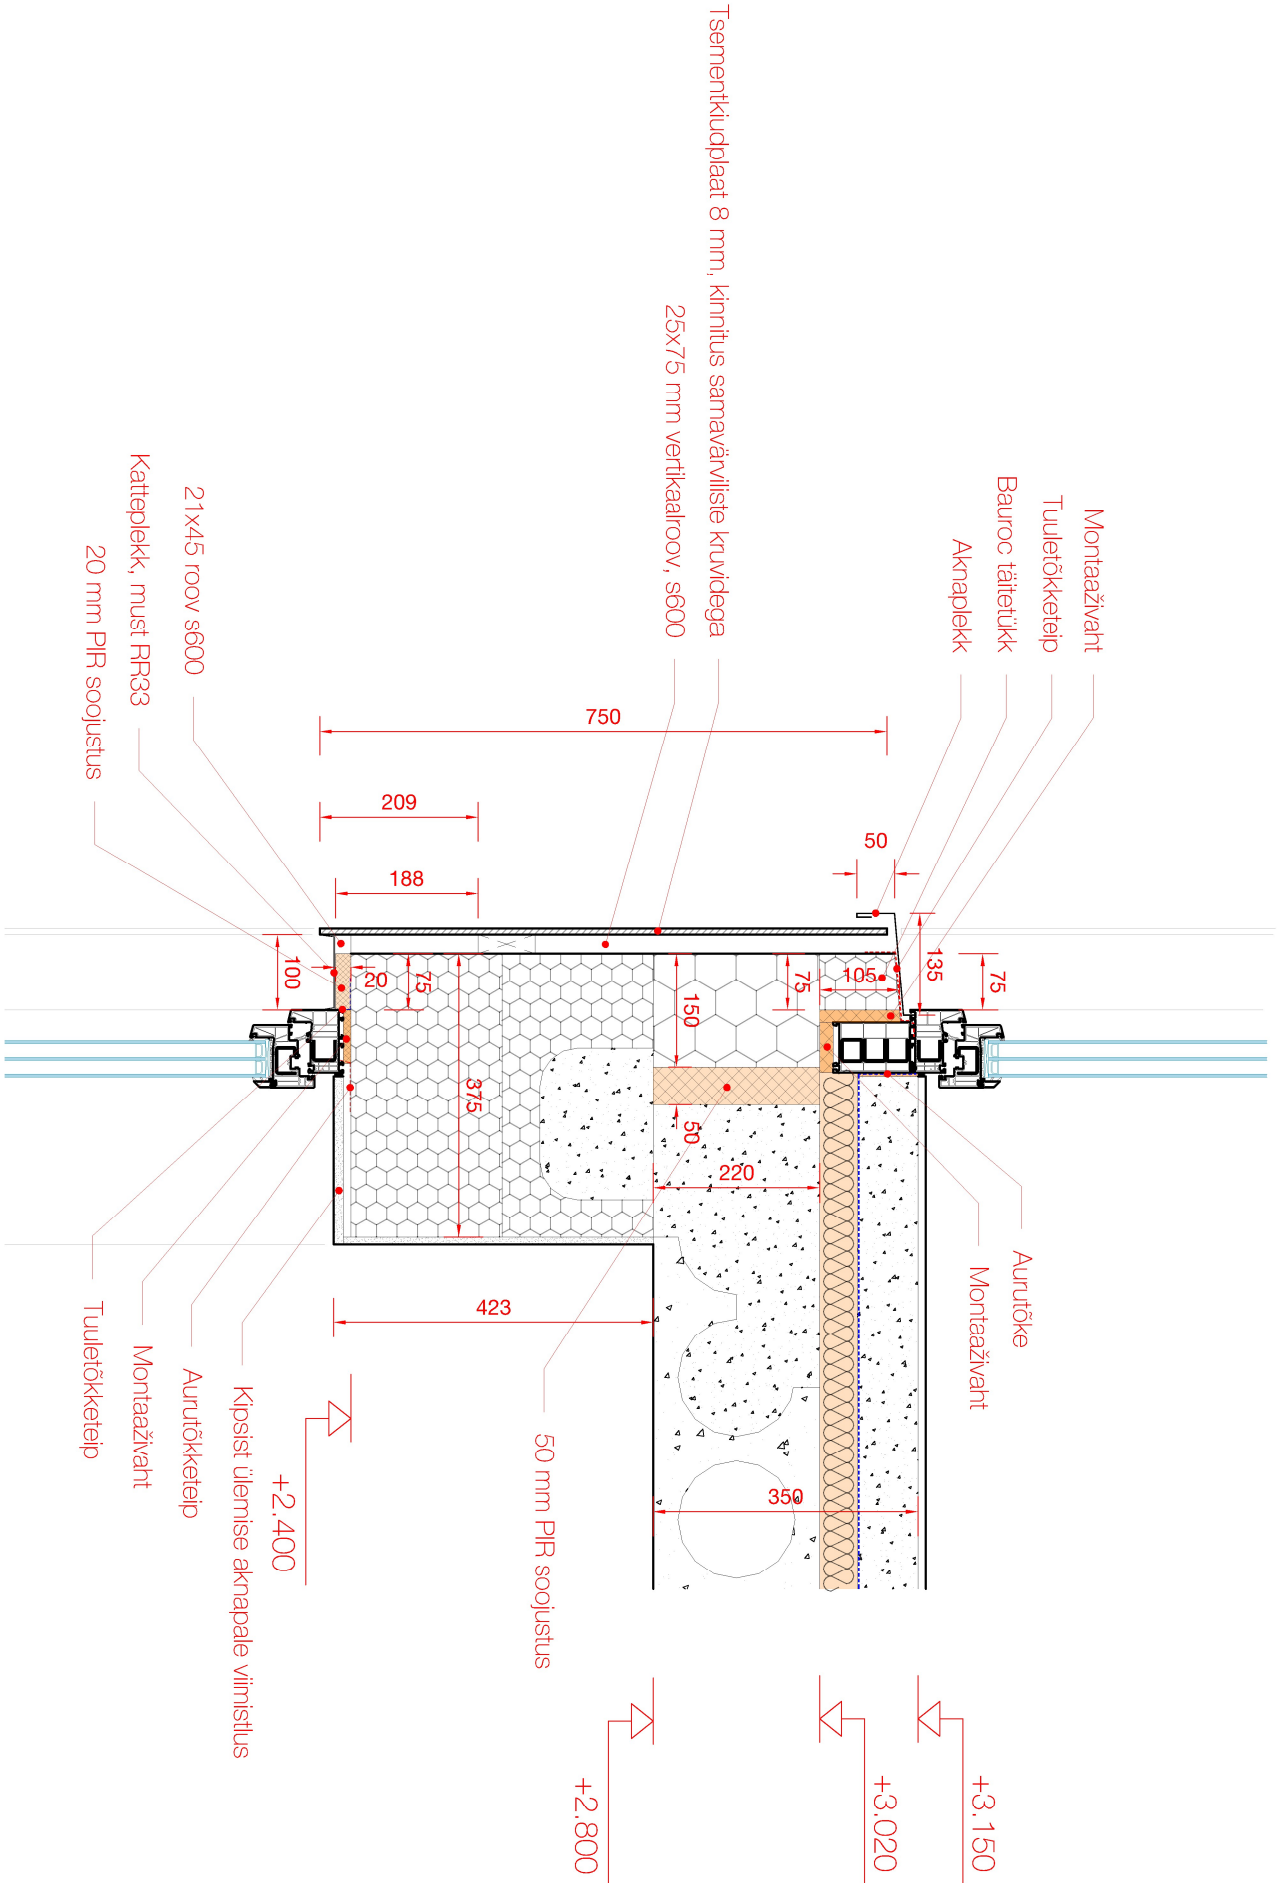

ARHITEKT 

Objekt:	Saku Ridaelamu	Address:	Kuu tee 16, Komeedi 1, Komeedi 2, Saku alevik
Joonis:			

S08 Vahelagi fassaadis (aknad vahelae osas)

Projekteeris:	E.Endjärv	Vastutav arhitekt:	E.Endjärv
Arhitekti 1 OÜ, reg nr 12190827, Jõa 2/1, 10127 Tallinn, ESTONIA, info@arhitekti1.ee; KMKR EE101499183			

Joonise nr. **AR-7-08**

Kuupäev:	23/05/2025	
Mõõtkava:	1:10; A3	PP
Töö nr:	---	

Projekti juht:	Nele Soobik
mele.sobik@nobe.ee	+372 566 19 889