


NB! Sissepääsupoolsete seinte fassaadilauded ja roovid immutatud tulekaitsevõõbaga! vt. vaatejoonis.

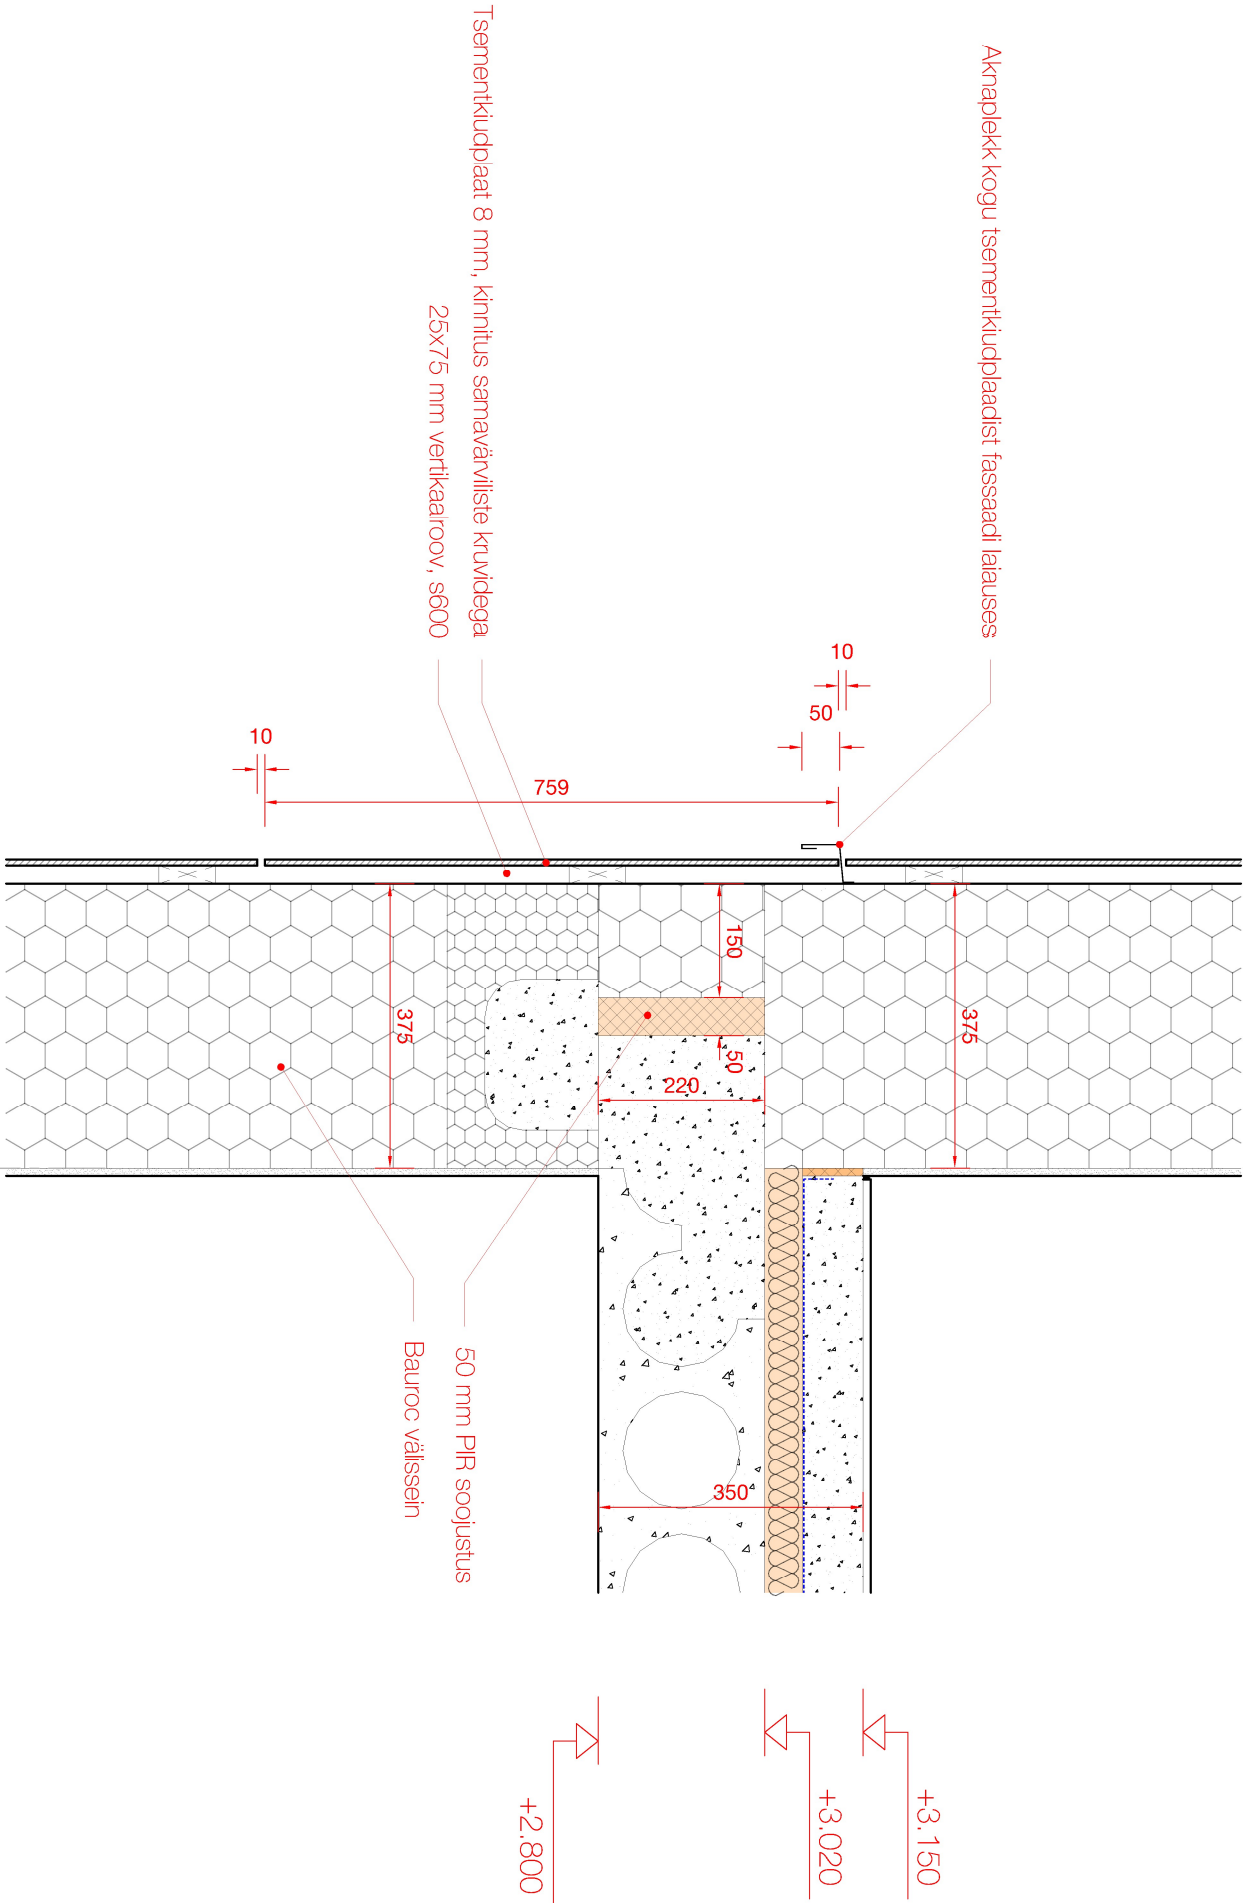

ARHITEKT



Objekt:	Saku Ridaelamu	Address:	Kuu tee 16, Komeedi 1, Komeedi 2, Saku alevik
Joonis:			

S09 Sein vahelaes (tsementikiudpladi hor. vuuk)

Projekteeris:	E.Endjärv	Vastutav arhitekt:	E.Endjärv
Arhitekti 1 OÜ, reg nr 12190827, Jõa 2/1, 10127 Tallinn, ESTONIA, info@arhitekt1.ee; KMKR EE101499183			

Joonise nr.

AR-7-09

Kuupäev:	23/05/2025
Mõõtkava:	1:10; A3
Töö nr:	---

Projekti juht:	Nelle Soobik
meie soobik@nobe.ee	+372 566 19 889