


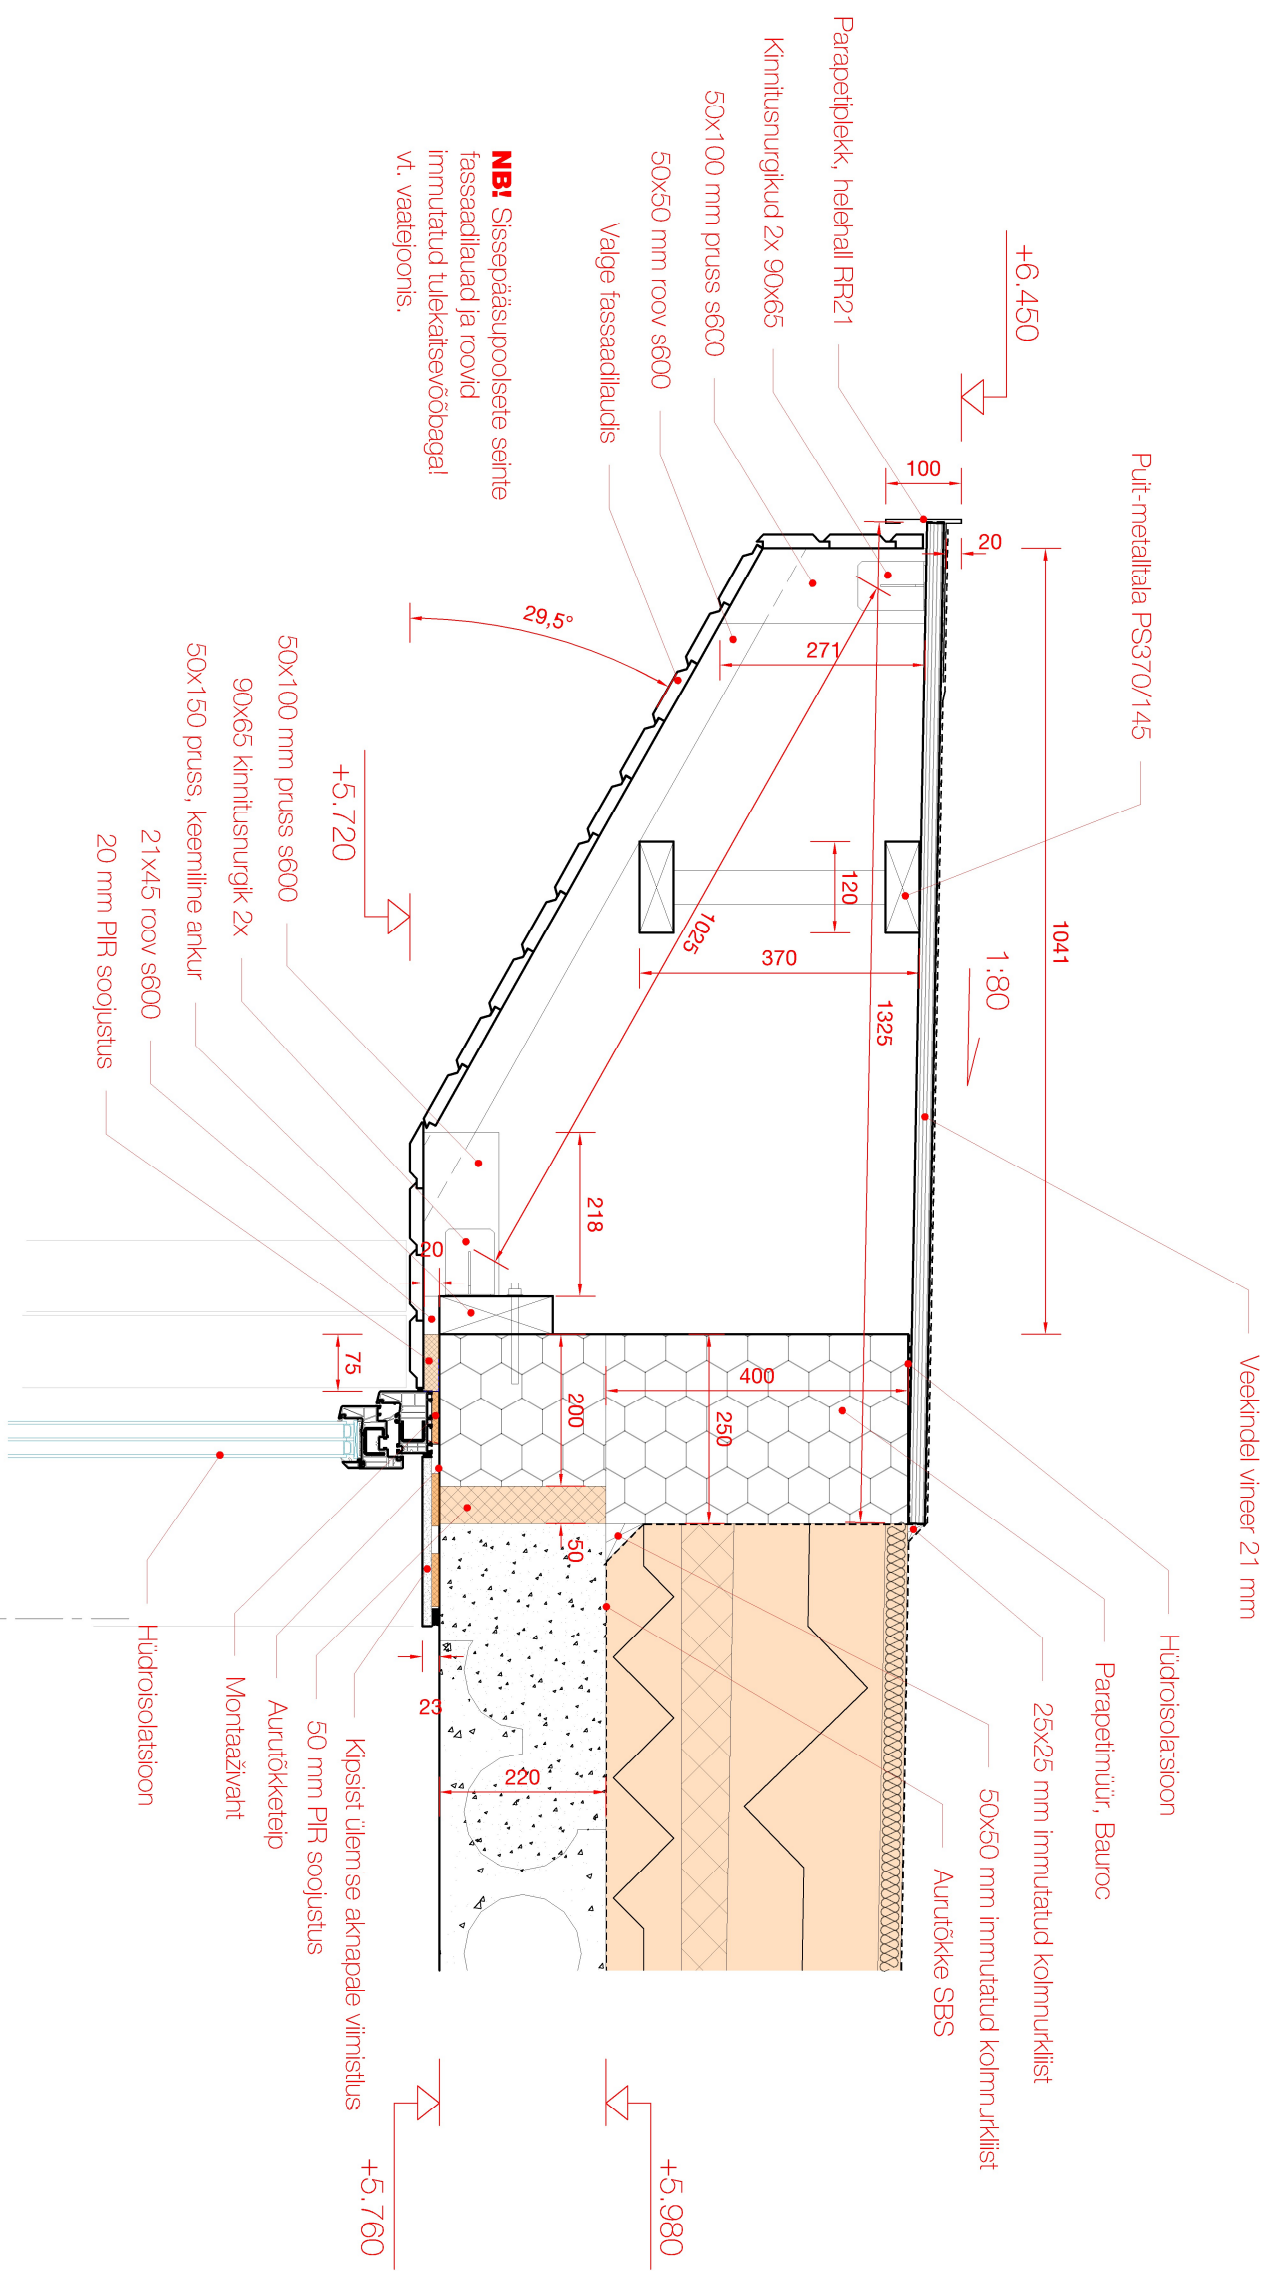

ARHITEKT

Objekt:	Saku Ridaelamu	Address:	Kuu tee 16, Komeedi 1, Komeedi 2, Saku alevik	Kuupäev:	23/05/2025	
Joonis:	S10 Katuse konsool			Mõõtkaava:	1:10; A3	PP
				Töö nr:	---	

Projekteeris:	Vastutav arhitekt:	Projektdiisr:
E. Endjänn	E. Endjänn	Nele Soobik
Arhitekti 1 OÜ, reg nr 12190827, Jõa 2/1, 10127 Tallinn, ESTONIA, info@arhitekti1.ee; KMKR EE101499183		
nele.soobik@nobe.ee +372 566 19 889		

nele.soobik@nobe.ee
+372 566 19 889