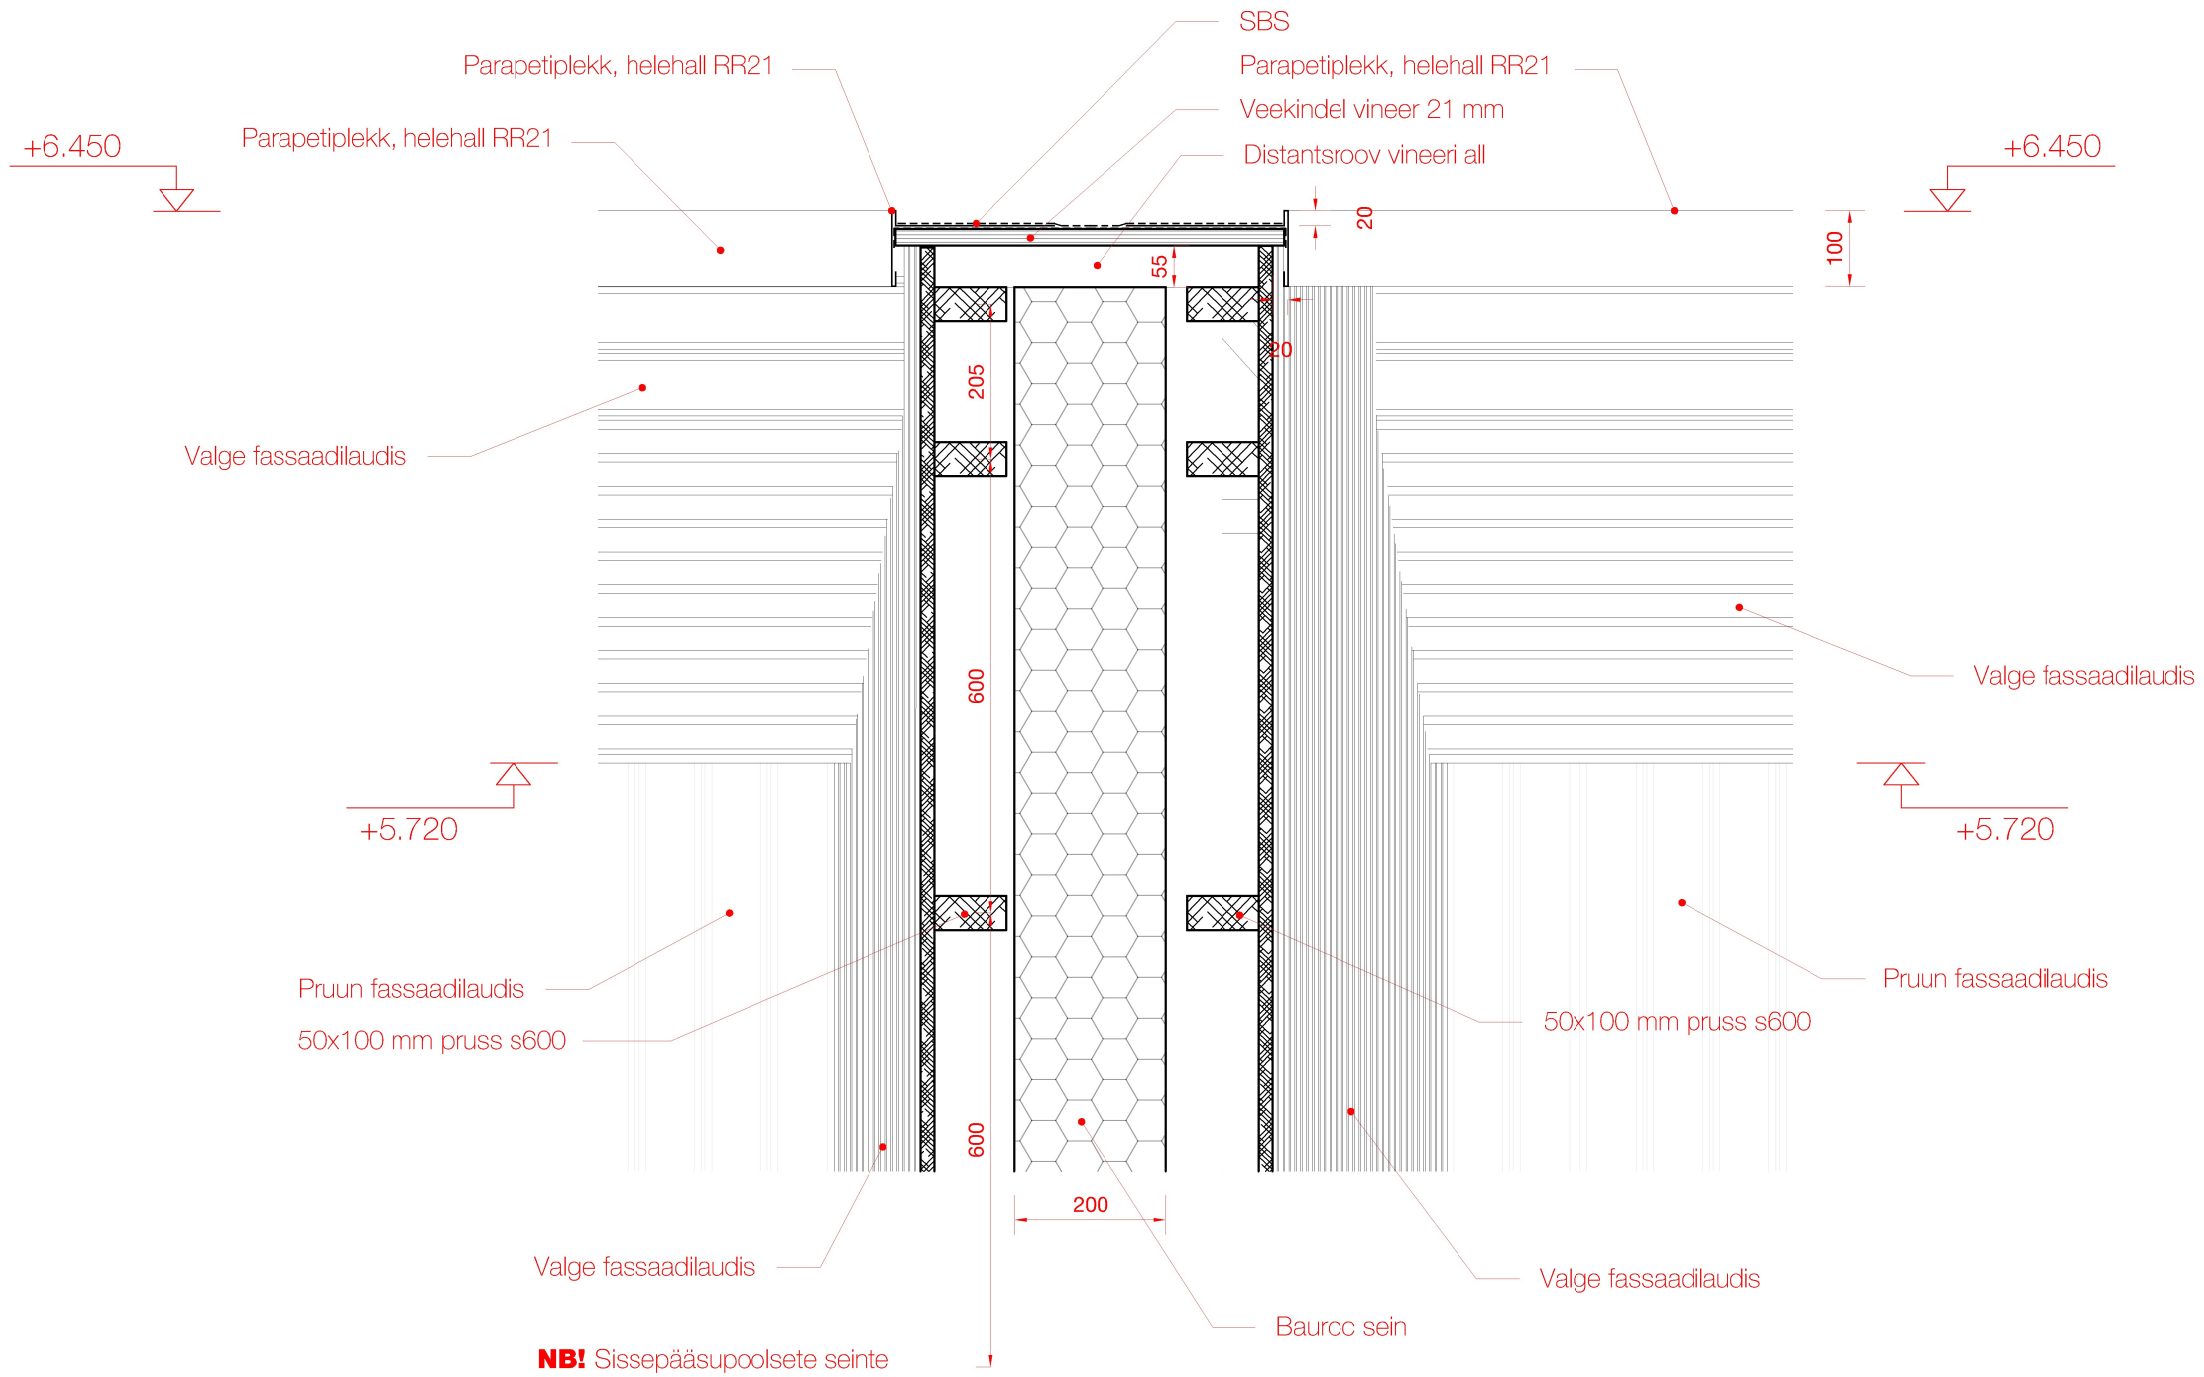

NB! Sissepääsupoolsete seinte fassaadilauad ja roovid immutatud tulekaitsevõõbaga! vt. vaateoonis.

ARHITEKT 11

Objekt:	Saku Ridaelamu	Aadress:	Kuu tee 16, Komeedi 1, Komeedi 2, Saku alevik

Joonis:

S12 Seina eendi parapet

Projekteeris:	E.Endjärv	Vastutav arhitekt:	E.Endjärv

Arhitekt11 OÜ, reg nr 12190827, Joa 2/1, 10127 Tallinn, ESTONIA, info@arhitekt11.ee; KMKR EE101499183

Joonise nr.	AR-7-13
Kuupäev:	23/05/2025
Mõõtkava:	1:10; A3 PP
Töö nr:	---

Projektijuht:
Nele Soobik
nele.soobik@nobe.ee
+372 566 19 889