



VALGUSTITE TINGMÄRGID		
Tähis	Tingmärk	Nimetus
V-01	⊗	Süvisvalgusti
V-02	⊗	Süvisvalgusti niiskukindel
V-03	⌞	Pinnapealne laevalgusti
V-04	⊗	Pinnapealne laevalgusti
V-06.1	—	Peegel valgustusega
V-06.2	—	Peegel valgustusega
V-07	⊗	Laevalgusti
V-LED	—	LEDriba valgustus mööblis toide

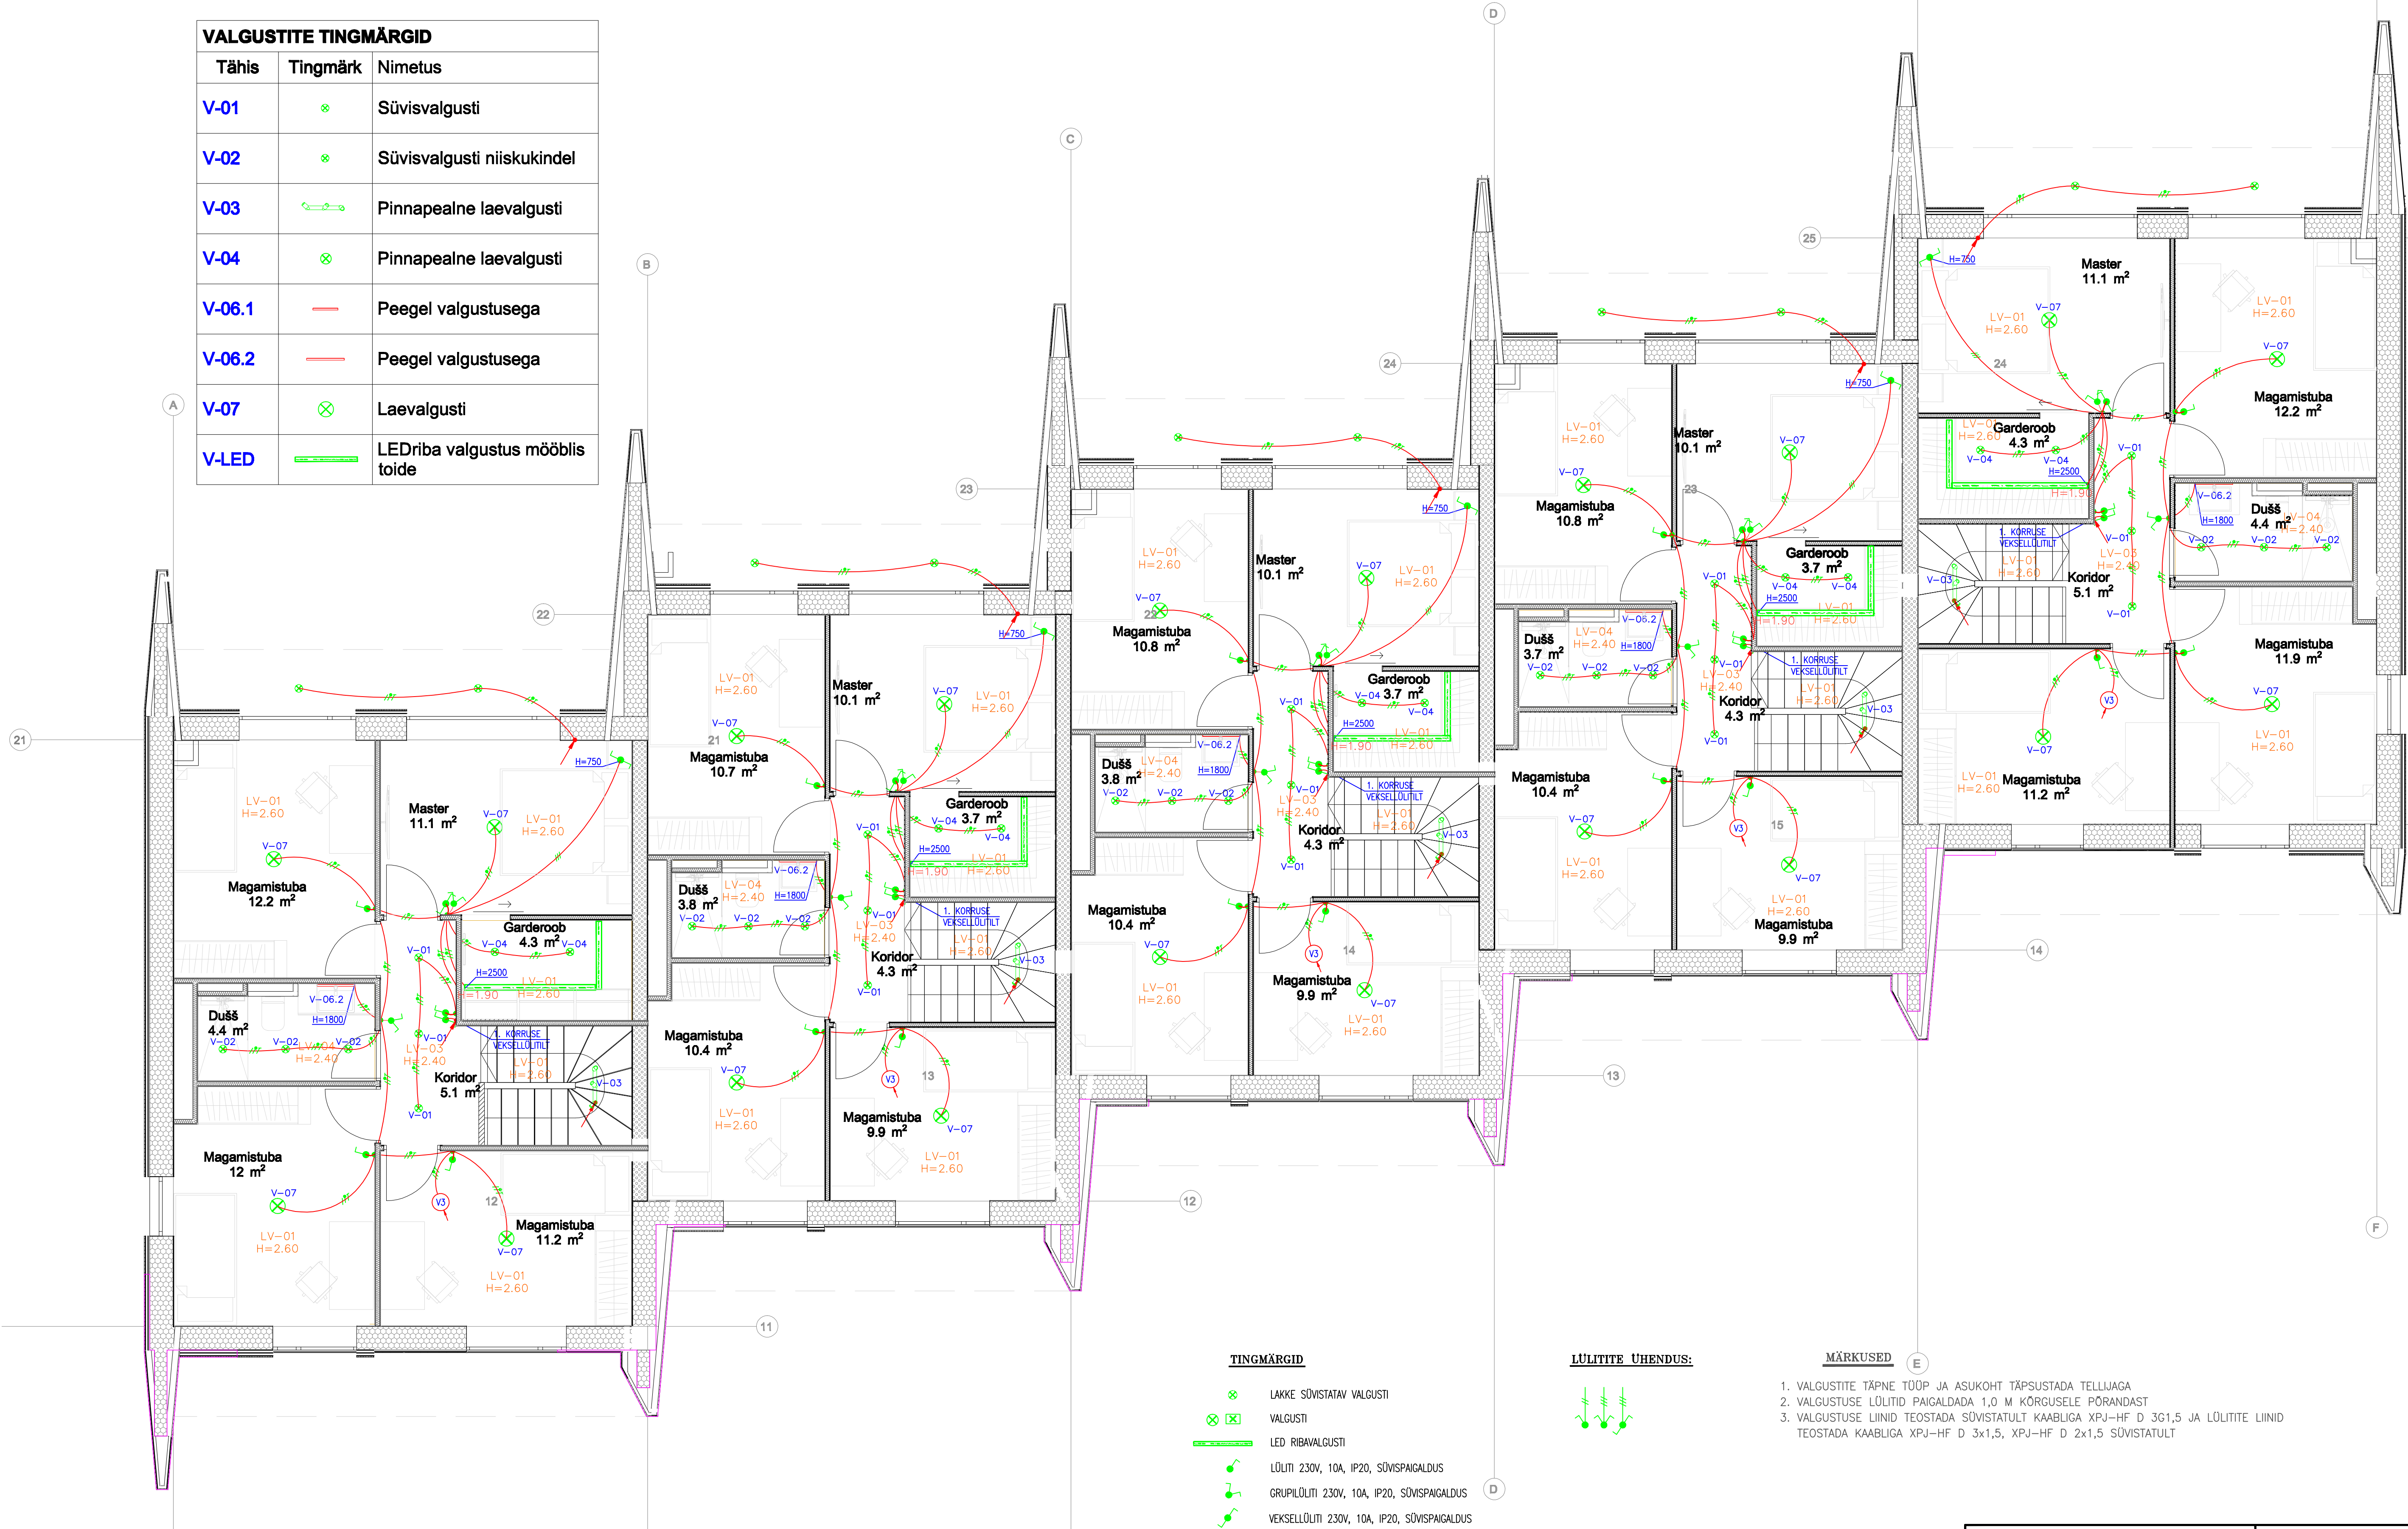

TINGMÄRGID

- ⊗ LAKKE SÖVISTATAV VALGUSTI
- ⊗ VALGUSTI
- LED RIBAVALGUSTI
- ⌞ LÖLITI 230V, 10A, IP20, SÖVISPAILGALDUS
- ⌞ GRUPLÖLITI 230V, 10A, IP20, SÖVISPAILGALDUS
- ⌞ VEKSELLÖLITI 230V, 10A, IP20, SÖVISPAILGALDUS

LÜLITITE ÜHENDUS:

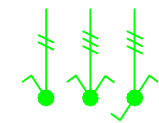

MÄRKUSED

- VALGUSTITE TÄPNE TÖÖP JA ASUKOHT TÄPSUSTADA TELLIJAGA
- VALGUSTUSE LÜLITID PAIGALDADA 1,0 M KÕRGUSELE PÕRANDAST
- VALGUSTUSE LIINID TEOSTADA SÖVISTATULT KAABLIGA XPJ-HF D 3G1,5 JA LÜLITITE LIINID TEOSTADA KAABLIGA XPJ-HF D 3x1,5, XPJ-HF D 2x1,5 SÖVISTATULT

Tellija NOBE OÜ		Töö RIDAEALAMU ELEKTRIPAIGALDIS	
Objekt KOMEDI TN. 1, SAKU, SAKU VALD, HARJUMAA		Töö nr: 2418	
Joonis 2.KORRUSE VALGUSTUSPAIGALDISE PLAAN			
Projekteeris: V. RANNAKIVI	VivaLight	Muudatus:	Joonise nr: EL-02
Kontrollis:		Staudum: PÕHIPROJEKT	Leht/nr: 1/1
Kuupäev: 28.02.2025	TEL-000204	Falt: 2418_PP_E-4-02_V01_2c.külg	Mööbelska: 1:50