


VALGUSTITE TINGMÄRGID		
Tähis	Tingmärk	Nimetus
V-01	✱	Süvisvalgusti
V-02	✱	Süvisvalgusti niiskukindel
V-04	✱	Pinnapealne laevalgusti
V-05	✱	Tehnoruumi laevalgusti
V-06.1	—	Peegel valgustusega
V-07	✱	Laevalgusti
V-LED	—	LEDriba valgustus mööblis toide

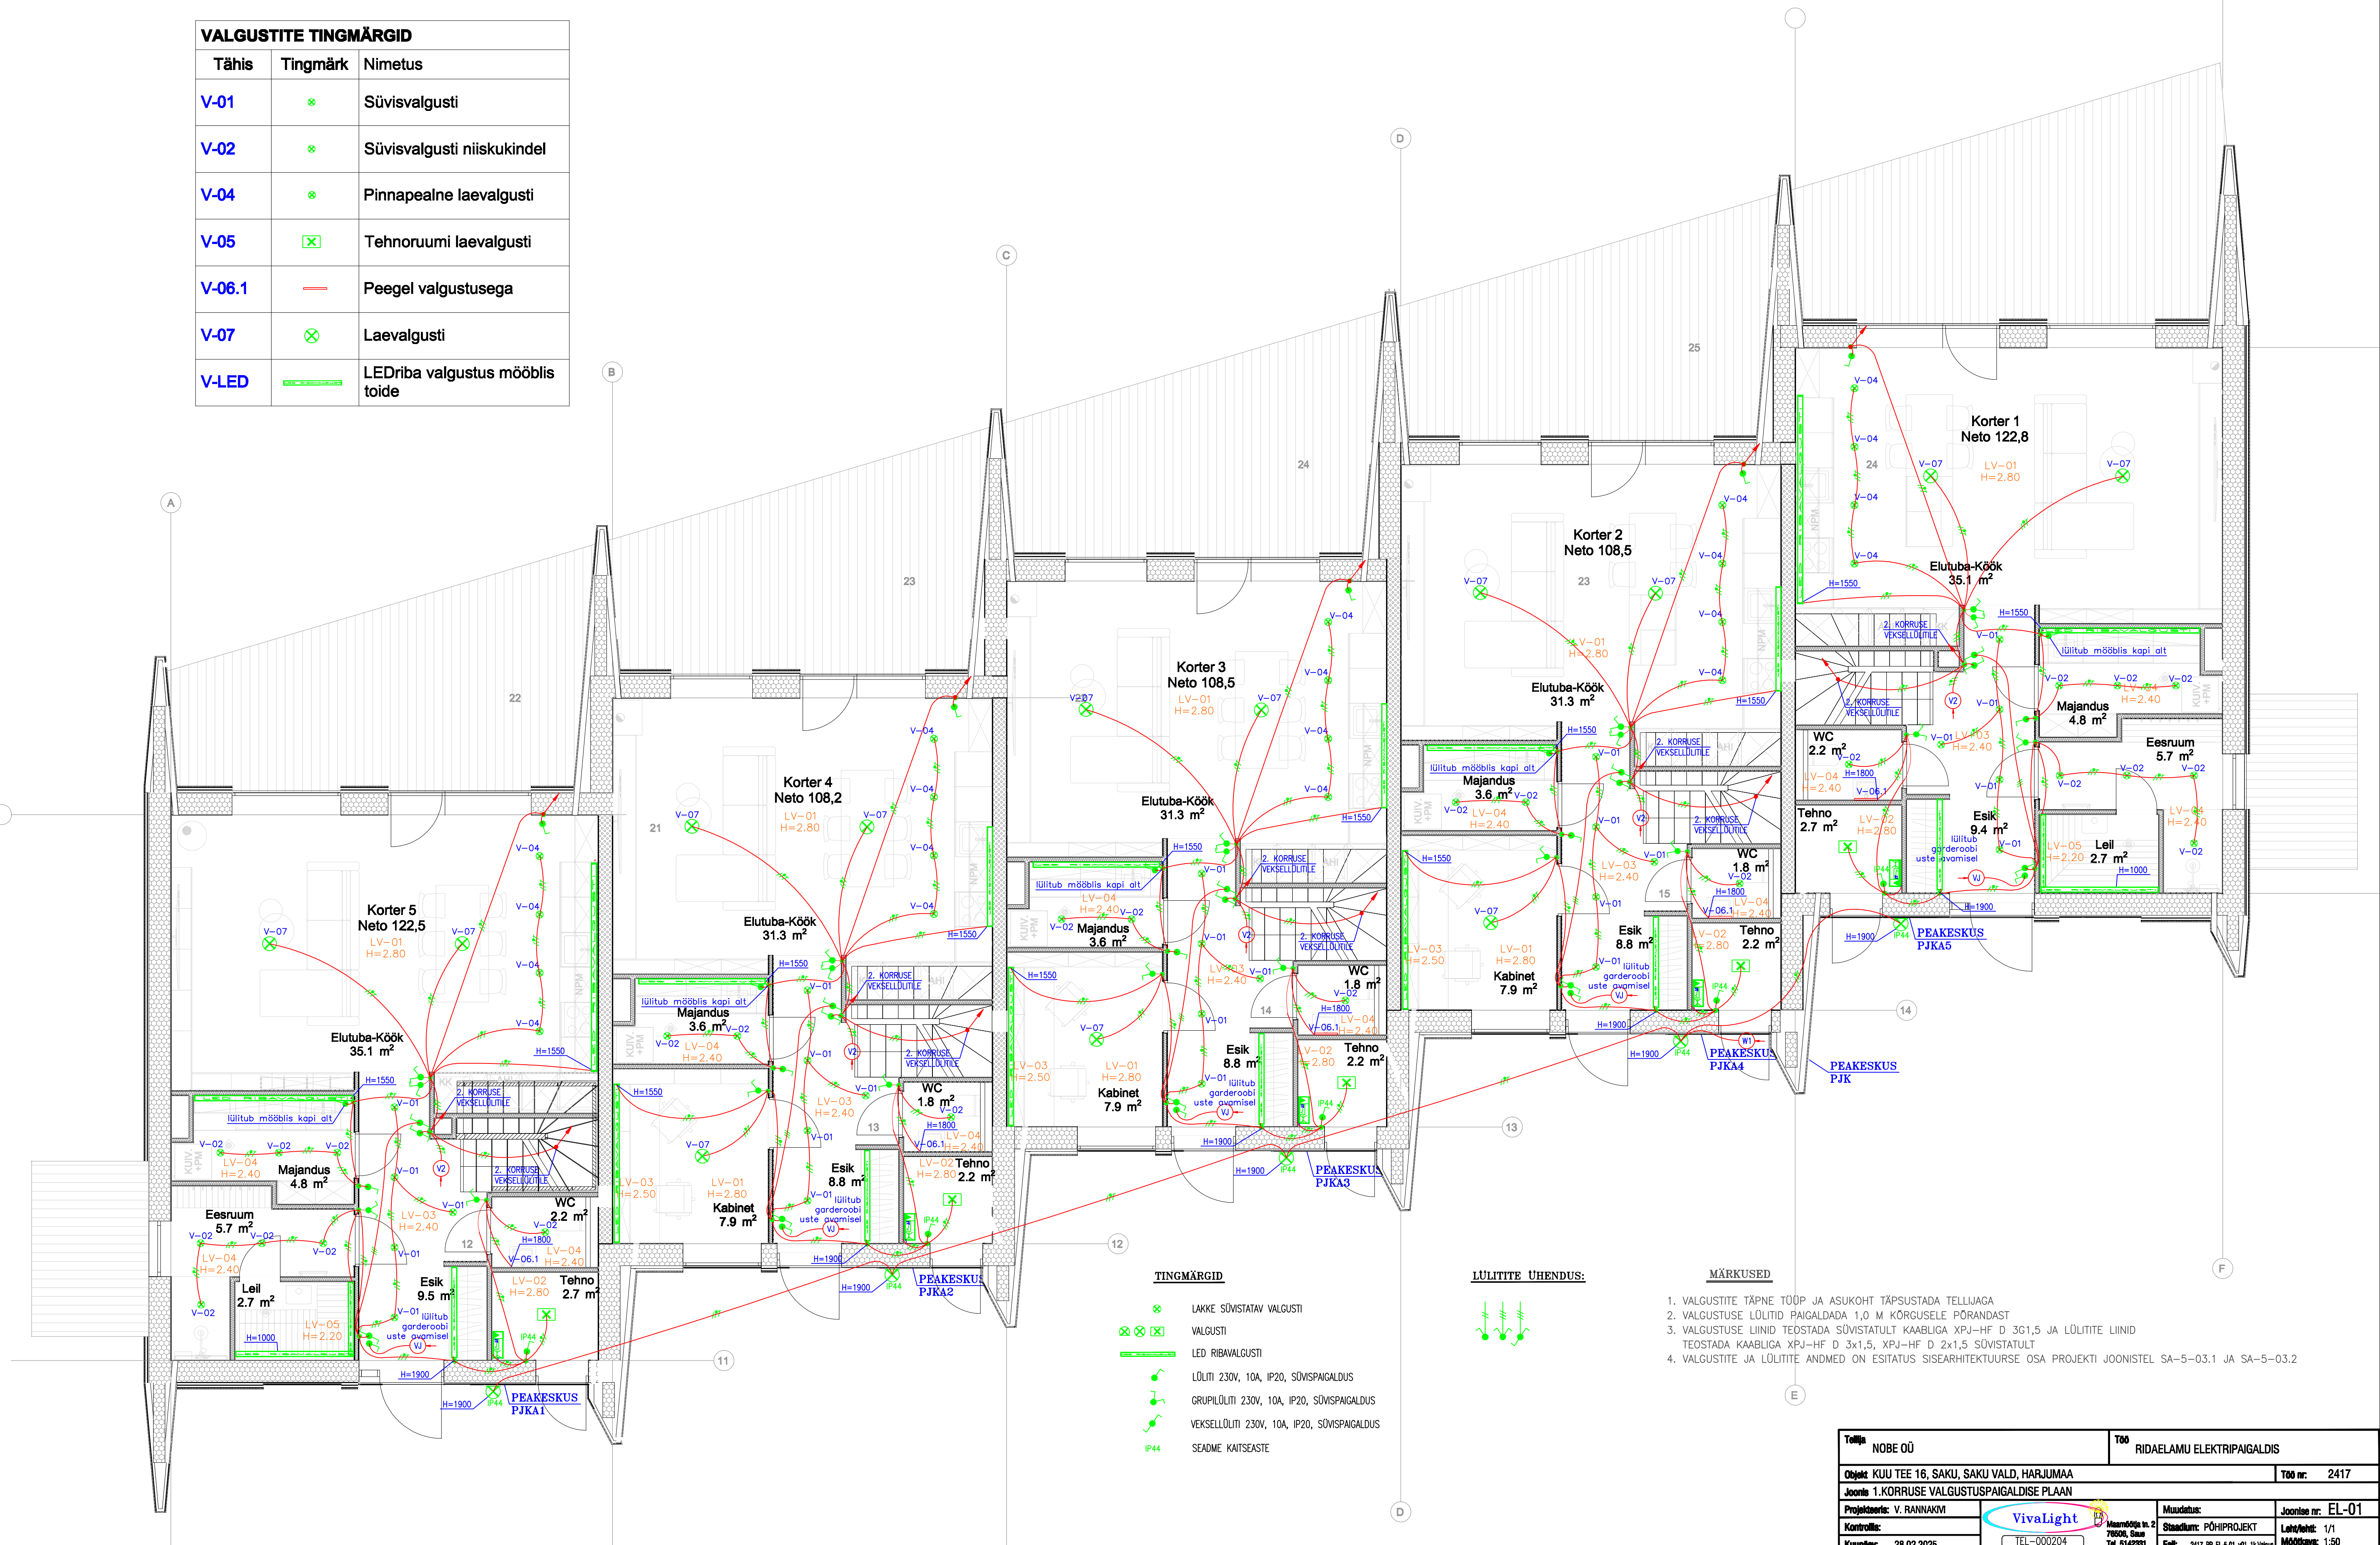

- TINGMÄRGID**
- ✱ LAKKE SÖVISTATAV VALGUSTI
 - ✱ VALGUSTI
 - LED RIBAVALGUSTI
 - LÜLITI 230V, 10A, IP20, SÖVISPAGALDUS
 - GRUPILÜLITI 230V, 10A, IP20, SÖVISPAGALDUS
 - VEKSELLÜLITI 230V, 10A, IP20, SÖVISPAGALDUS
 - IP44 SEADME KAITSEASTE

LÜLITITE ÜHENDUS:

- MÄRKUSED**
- VALGUSTITE TÄPNE TÖÖP JA ASUKOHT TÄPSUSTADA TELLUAGA
 - VALGUSTUSE LÜLITID PAIGALDADA 1,0 M KÕRGUSELE PÕRANDAST
 - VALGUSTUSE LIINID TÄPSUSTADA SÖVISTATULT KAABLIGA XPJ-HF D 3G1,5 JA LÜLITITE LIINID TÄPSUSTADA KAABLIGA XPJ-HF D 3x1,5, XPJ-HF D 2x1,5 SÖVISTATULT
 - VALGUSTITE JA LÜLITITE ANDMED ON ESITATUS SISEARHITEKTUURSE OSA PROJEKTI JOONISTEL SA-5-03.1 JA SA-5-03.2

Tööaja NOBE OÜ		Töö RIDAELAMU ELEKTRIPAIGALDIS	
Objekt KUU TEE 16, SAKU, SAKU VALD, HARJUMAA			Töö nr: 2417
Joonis 1.KÕRRUSE VALGUSTUSPAIGALDISE PLaan			
Projektoris: V. RANNAKVI		Muudatus:	Joonise nr: EL-01
Kontrollis:		Staudium: PÕHIPROJEKT	Lehe/lehti: 1/1
Kuupäev: 28.02.2025		TEL: 000204	Faht: 2417_PP_EL-01_v01_1x/Valgus