


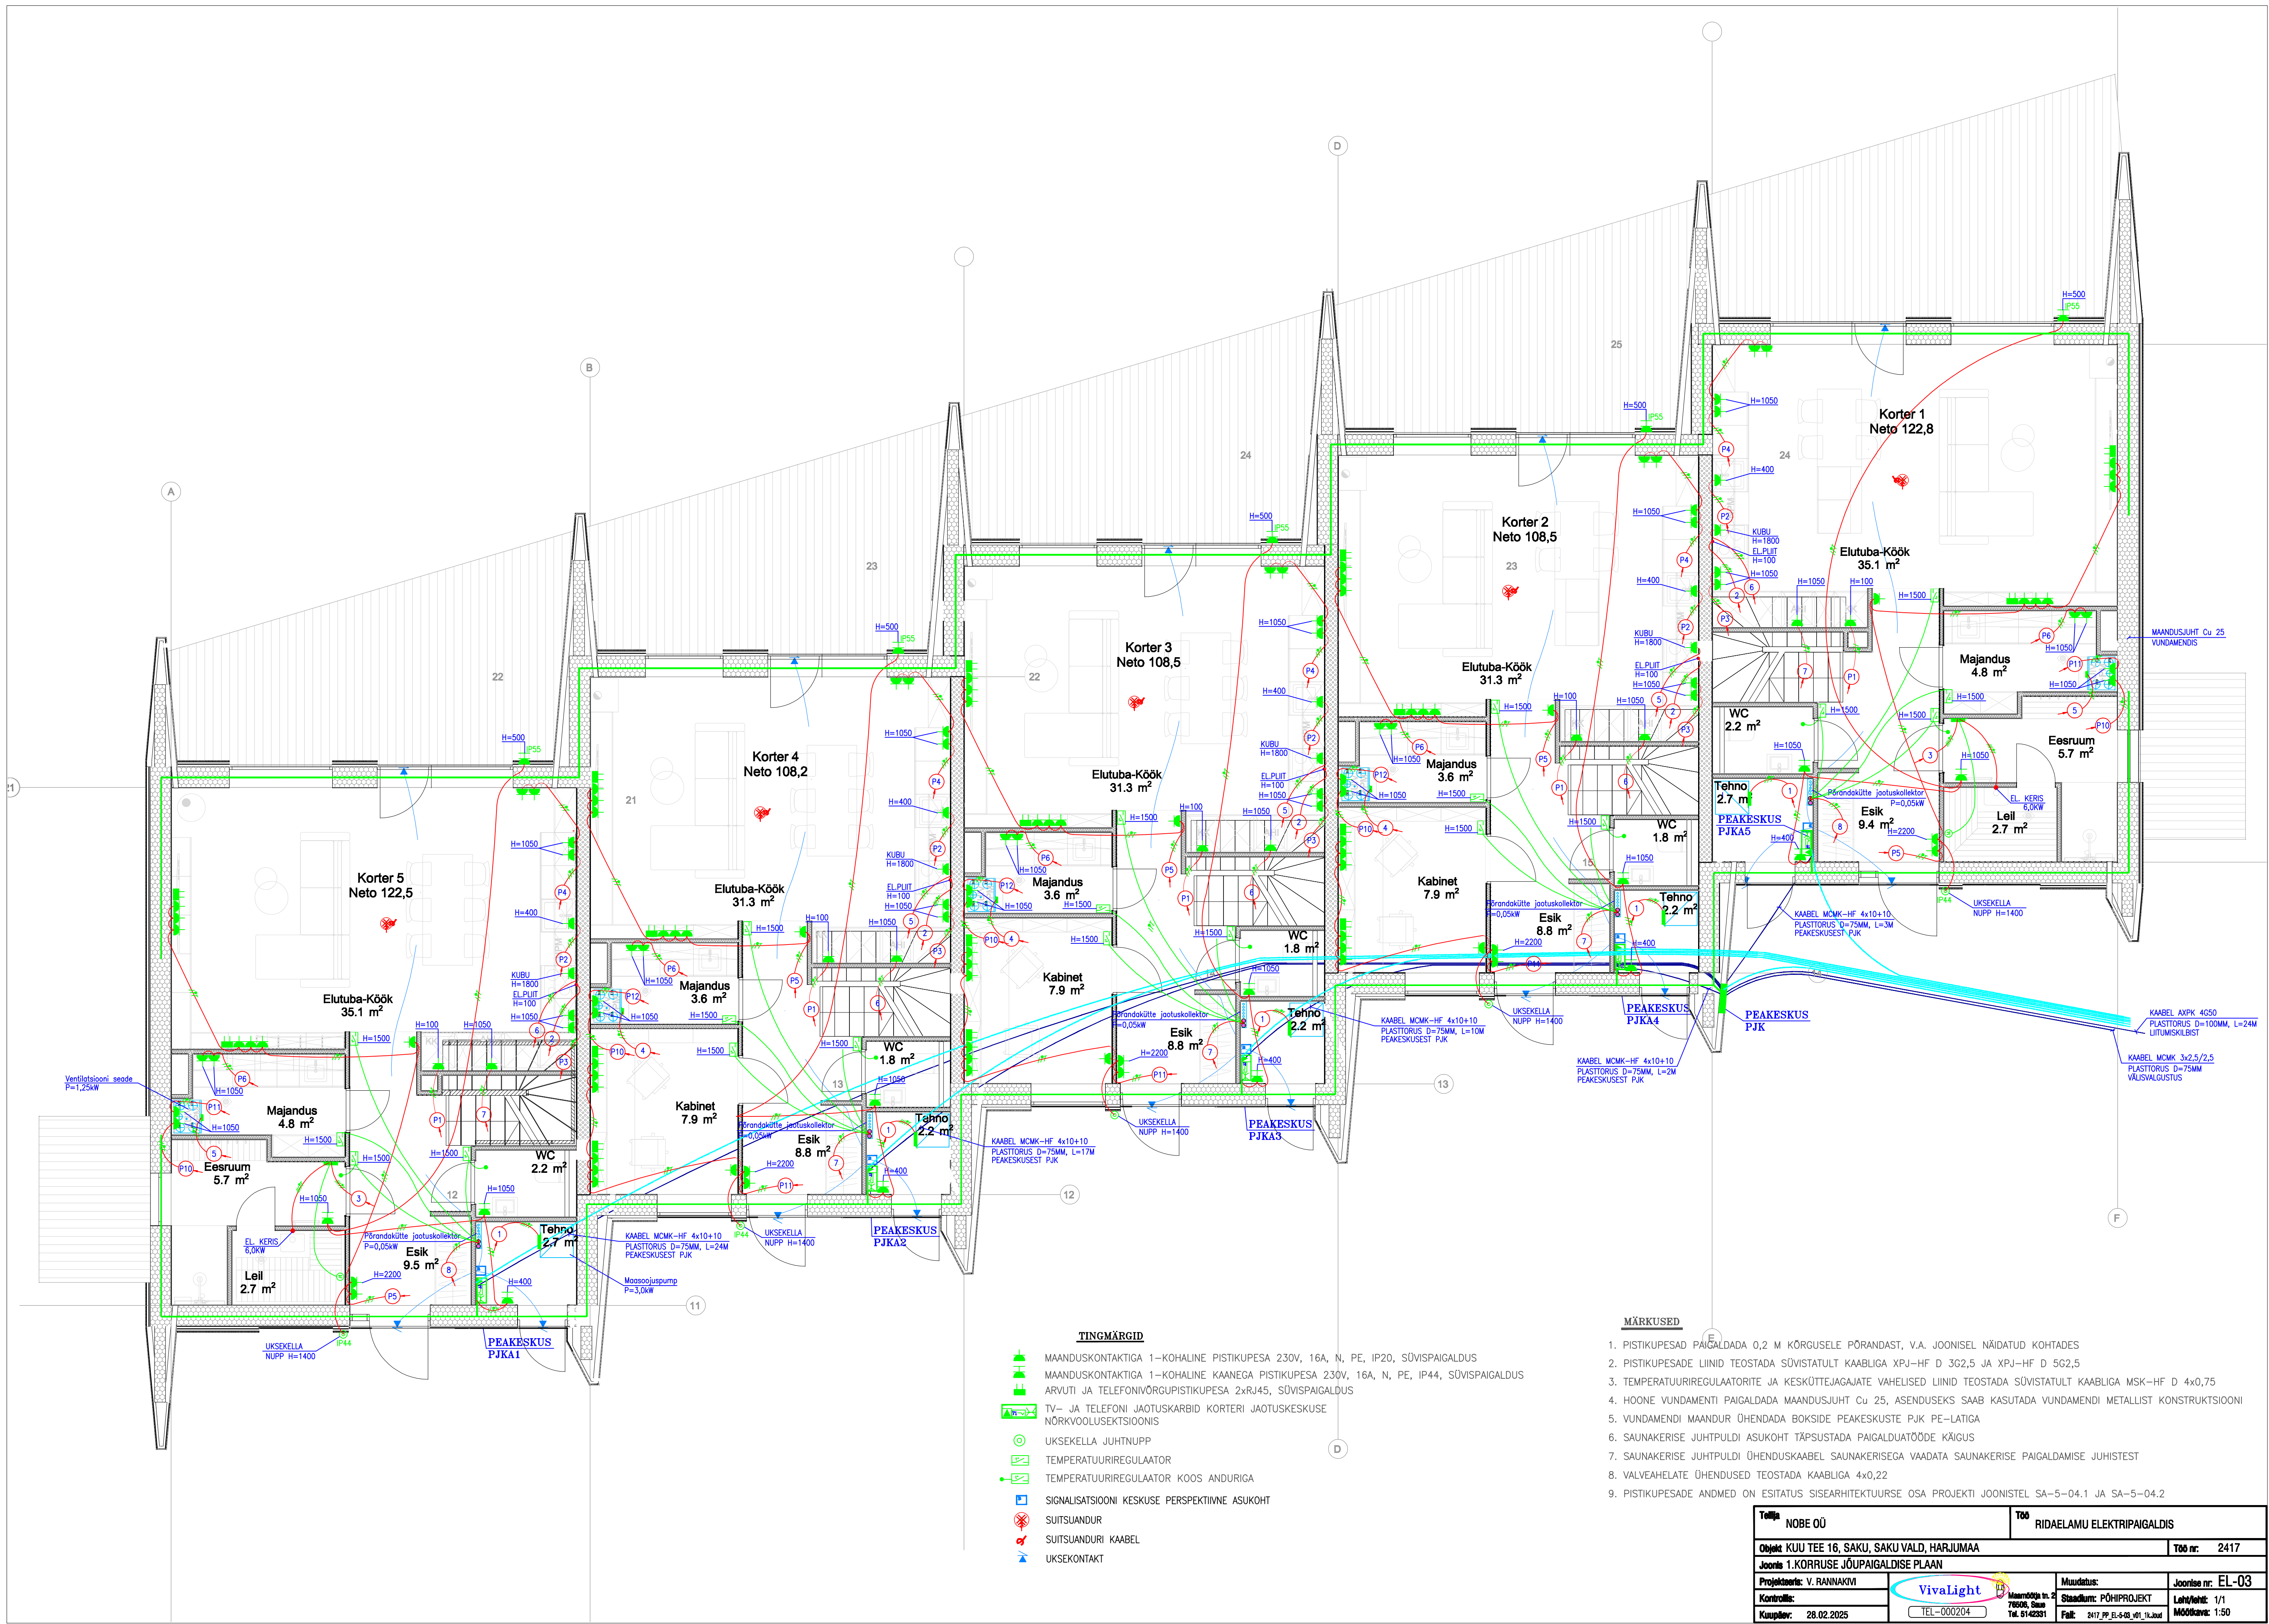

TINGMÄRGID

- MAANDUSKONTAKTIGA 1-KOHALINE PISTIKUPESA 230V, 16A, N, PE, IP20, SÜVISAIGALDUS
- MAANDUSKONTAKTIGA 1-KOHALINE KANAEVA PISTIKUPESA 230V, 16A, N, PE, IP44, SÜVISAIGALDUS
- ARVUTI JA TELEFONIVÕRGUPISTIKUPESA 2xRJ45, SÜVISAIGALDUS
- TV- JA TELEFONI JAOTUSKARBI KORTERI JAOTUSKESKUSE NÕRKVÕLUSEKTSIOONIS
- UKSEKELLA JUHTNUPP
- TEMPERatuurIREGULAATOR
- TEMPERatuurIREGULAATOR KOOS ANDURIGA
- SIGNALISATSIOONI KESKUSE PERSPEKTIVNE ASUKOHT
- SUITSUANDUR
- SUITSUANDURI KAABEL
- UKSEKONTAKT

MÄRKUSED

- PISTIKUPESAD PAIGALDADA 0,2 M KÕRGUSELE PÖRANDAST, V.A. JOONISEL NÄIDATUD KOHTADES
- PISTIKUPESADE LIINID TEOSTADA SÖVISTATULT KAABLIGA XPJ-HF D 3G2,5 JA XPJ-HF D 5G2,5
- TEMPERatuurIREGULAATORITE JA KESKÜTTEJAGAJATE VAHELISED LIINID TEOSTADA SÖVISTATULT KAABLIGA MSK-HF D 4x0,75
- HOONE VUNDAMENTI PAIGALDADA MAANDUSJUHT Cu 25, ASENDUSEKS SAAB KASUTADA VUNDAMENTI METALLIST KONSTRUKTSIOONI
- VUNDAMENTI MAANDUR ÜHENDADA BOKSIDE PEAKESKUSTE PJK PE-LATIGA
- SAUNAKERISE JUHTPULDI ASUKOHT TÄPSUSTADA PAIGALDUOTOODE KÄIGUS
- SAUNAKERISE JUHTPULDI ÜHENDUSKAABEL SAUNAKERISEGA VAADATA SAUNAKERISE PAIGALDAMISE JUHISTEST
- VALVEAHELATE ÜHENDUSED TEOSTADA KAABLIGA 4x0,22
- PISTIKUPESADE ANDMED ON ESITATUD SISARHITEKTUURSE OSA PROJEKTI JOONISTEL SA-5-04.1 JA SA-5-04.2

Töidaja	NOBE OÜ	Töö	RIDAELAMU ELEKTRIPAIGALDIS
Objekt	KUU TEE 16, SAKU, SAKU VALD, HARJUMAA	Töö nr.	2417
Joonis	1.KORRUSE JÕUPAIGALDIS PLEAAN		
Projektoris	V. RANNAKIVI	Muudatus:	Joonise nr. EL-03
Kontrollis		Standard:	PÕHIPROJEKT
Kuupäev:	28.02.2025	Faht:	2417_PP_EL-03_v01_11.dwg
		Modifitseer:	1:50