


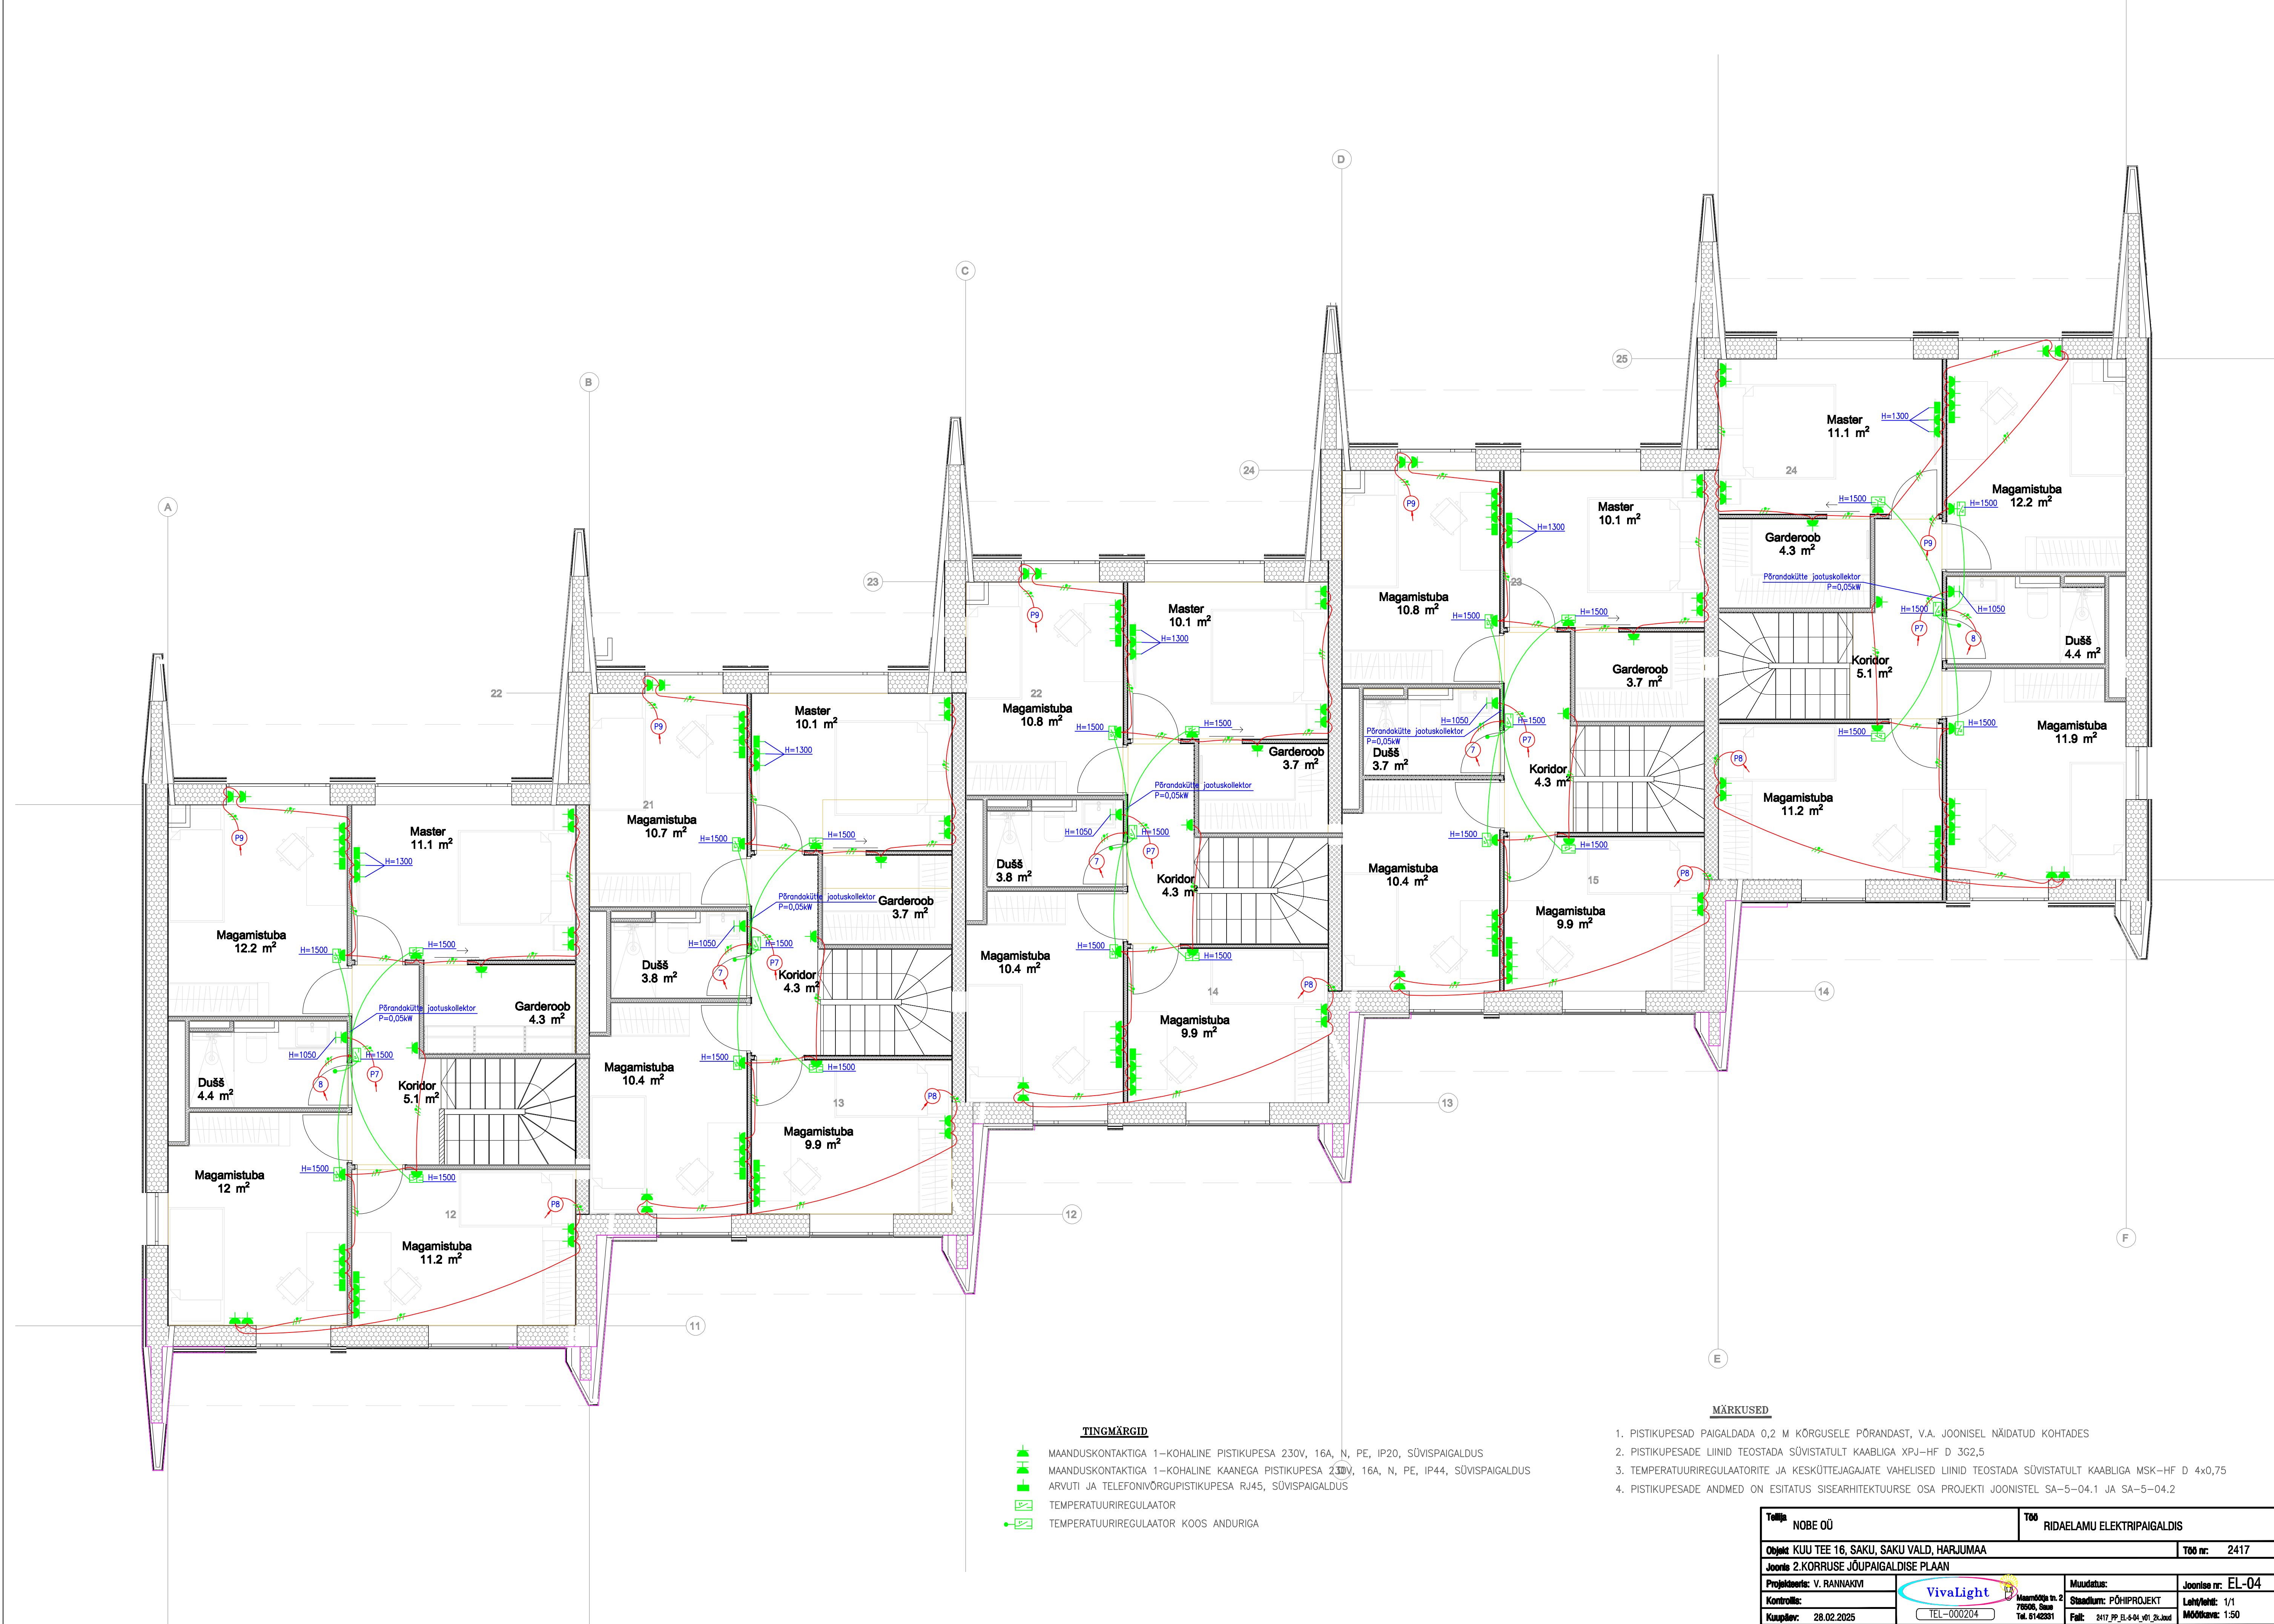

TINGMÄRGID

- MAANDUSKONTAKTIGA 1—KÖHALINE PISTIKUPESA 230V, 16A, N, PE, IP20, SÜVISPAIGALDUS
- MAANDUSKONTAKTIGA 1—KÖHALINE KANEGA PISTIKUPESA 230V, 16A, N, PE, IP44, SÜVISPAIGALDUS
- ARVUTI JA TELEFONIVÕRGUPISTIKUPESA RJ45, SÜVISPAIGALDUS
- TEMPERatuurIREGULAATOR
- TEMPERatuurIREGULAATOR KOOS ANDURIGA

MÄRKUSED

- PISTIKUPESAD PAIGALDADA 0,2 M KÕRGUSELE PÕRANDAST, V.A. JOONISEL NÄIDATUD KOHTADES
- PISTIKUPESADE LIINID TEOSTADA SÜVISTATULT KAABLIAGA XPJ—HF D 3G2,5
- TEMPERatuurIREGULAATORITE JA KESKÖTTEJAGAJATE VAHELISED LIINID TEOSTADA SÜVISTATULT KAABLIAGA MSK—HF D 4x0,75
- PISTIKUPESADE ANDMED ON ESITATUS SISEARHITEKTUURSE OSA PROJEKTI JOONISTEL SA—5—04.1 JA SA—5—04.2

Tellijä NOBE OÜ		Töö RIDAEELAMU ELEKTRIPAIGALDIS	
Objekt KUU TEE 16, SAKU, SAKU VALD, HARJUMAA			Töö nr: 2417
Joonis 2.KORRUSE JÕUPAIGALDISE PLAAN			
Projekteeris: V. RANNAKIVI	VivaLight	Muudatus:	Joonise nr: EL-04
Kontrollis:		Staadium: PÕHIPROJEKT	Leht/neli: 1/1
Kuupäev: 28.02.2025	TEL: 000204	Muudatuste nr: 2 76506, Sisse Tel. 614231	Faht: 2417_PP_E-04_V01_20.02.2025 Mõõtkava: 1:50