


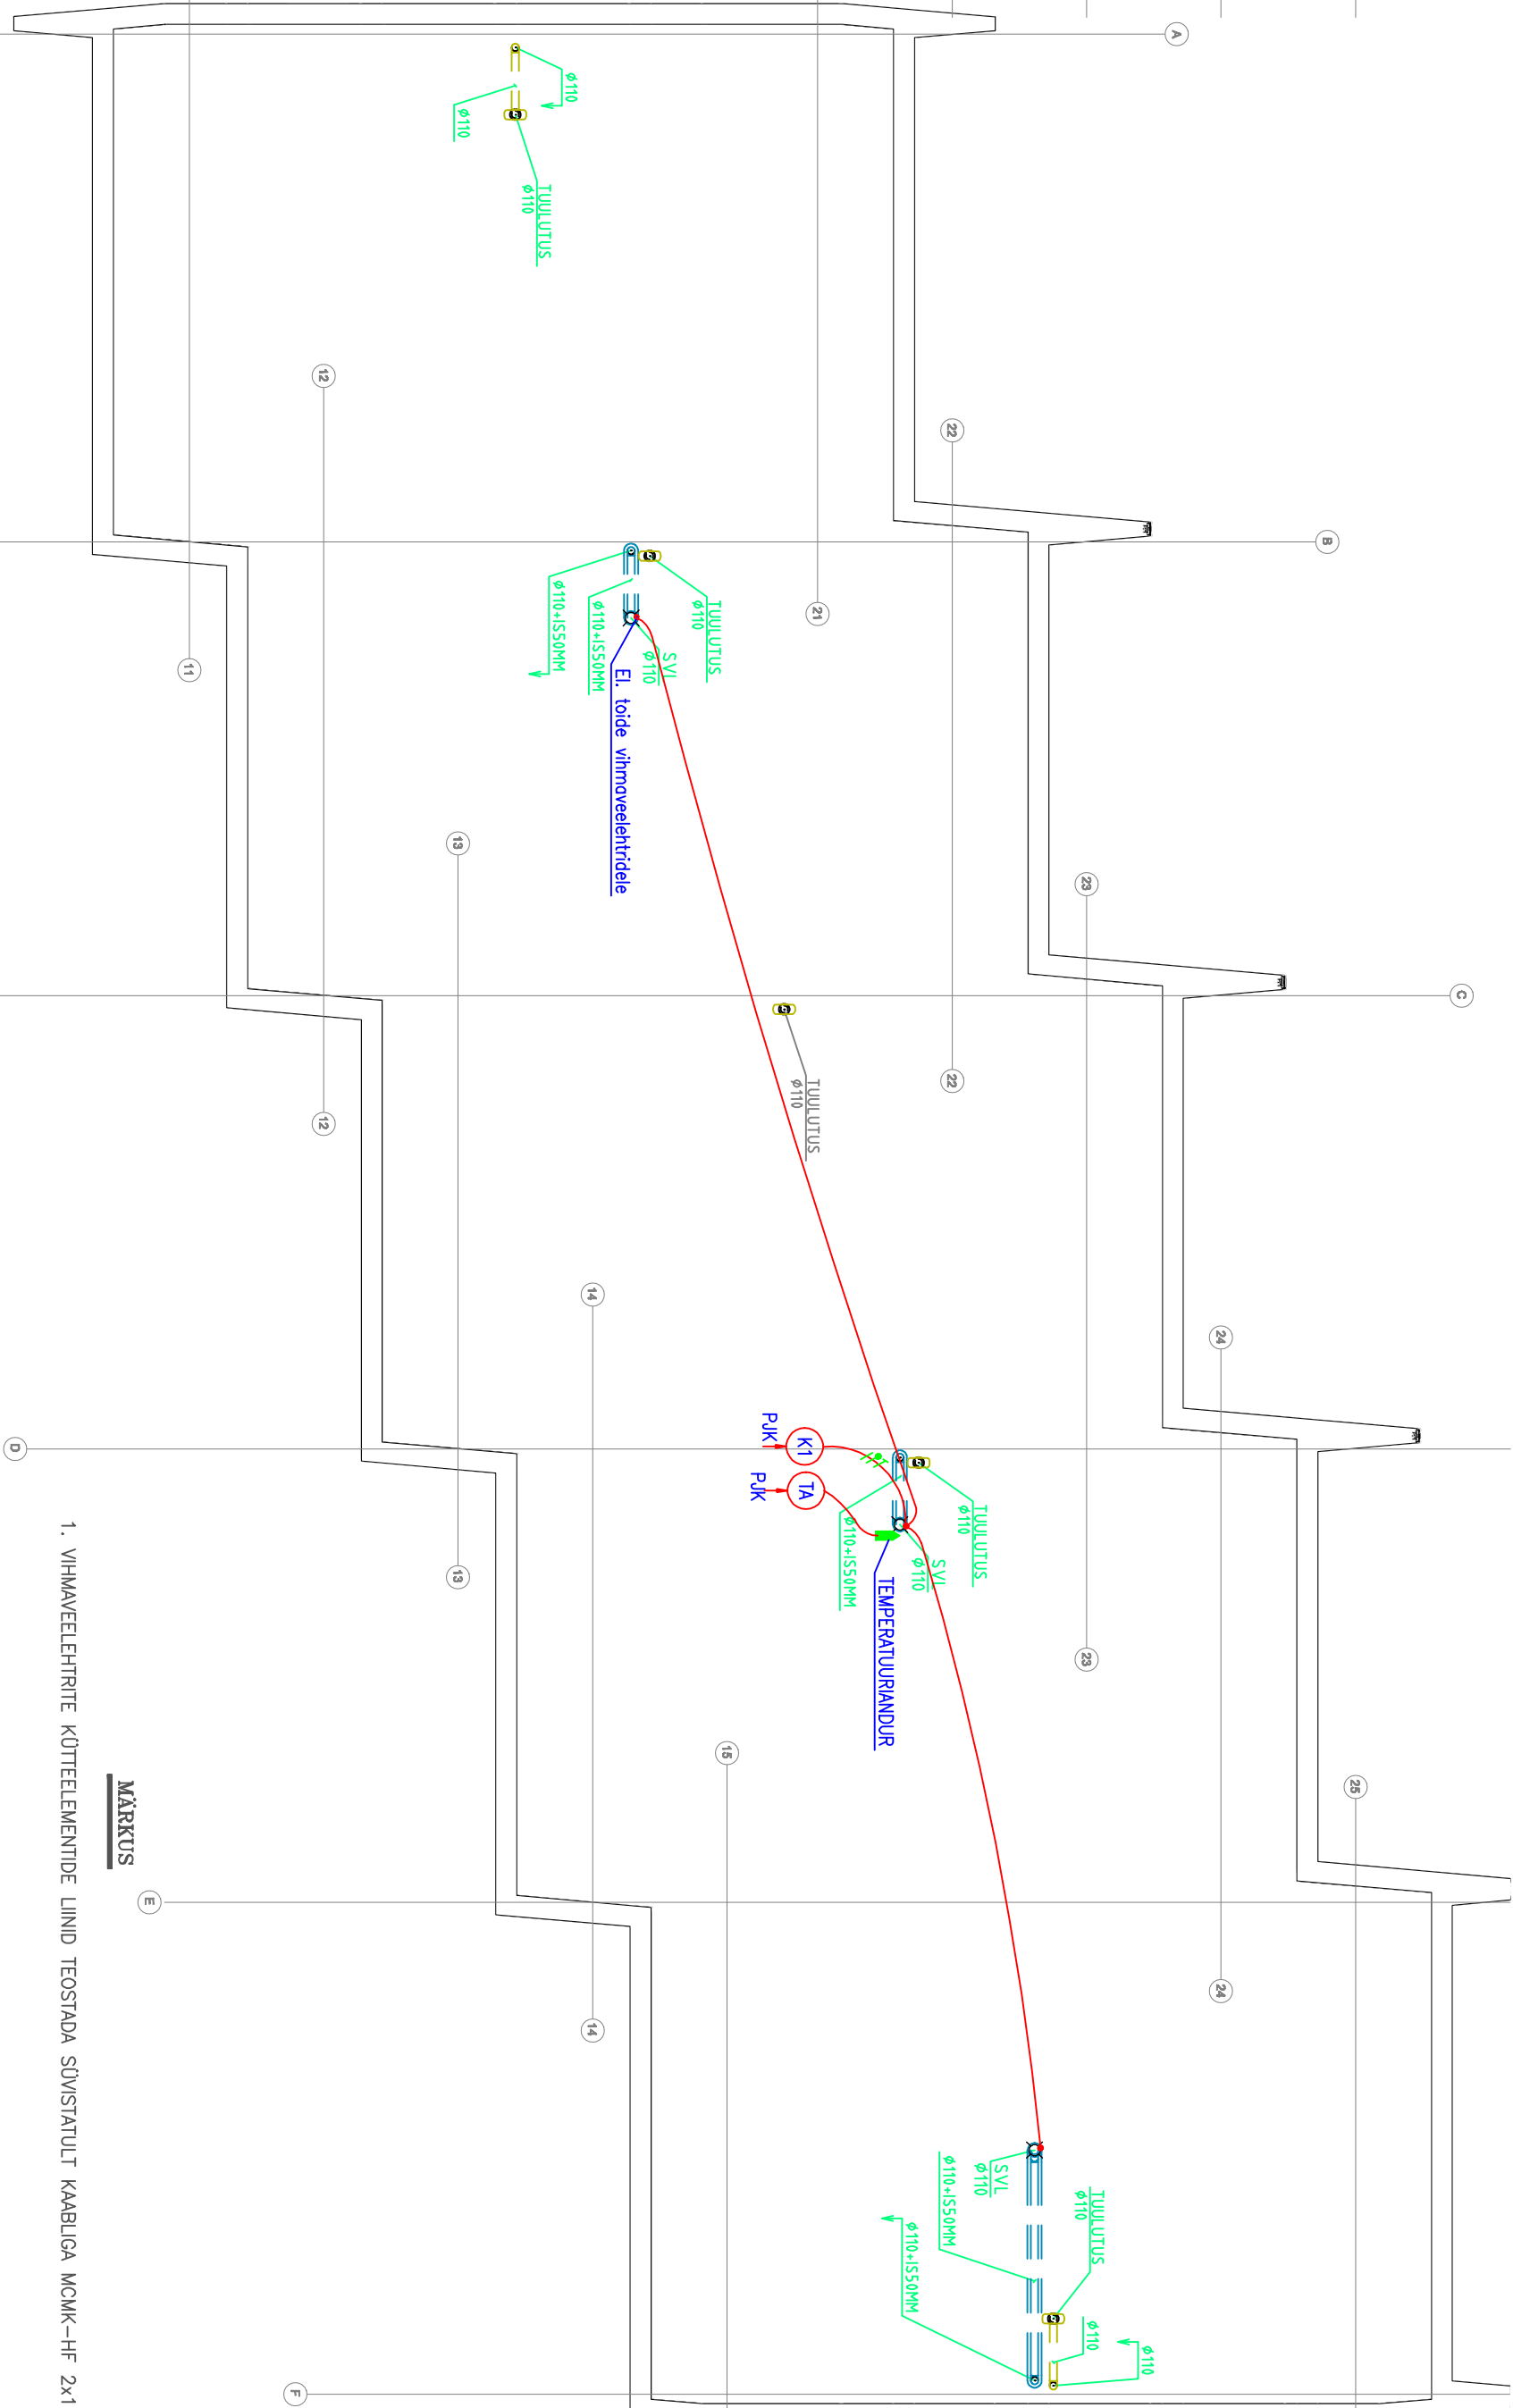

MÄRKUS

1. VIHMAVEELEHTRITE KÜTTEELEMENTIDE LIIKID TEOSTADA SÜVISTATULT KAABLIKA MCMK-HF 2x1.5/1.5

Tellijä NOBE OÜ		Töö RIIDEALAMU ELEKTRIPAIGALDIS	
Objekt KUU TEE 16, SAKU, SAKU VALD, HARJUMAA			
Joonis KATUSE ELEKTRIPAIGALDISE PLAAN		Töö nr. 2417	
Projekteeris: V. RANNAKIVI		Muudatus:	
Kontrollis:		Staadium: PÕHIPROJEKT	
Kujutäht: 28.02.2025		Lõpetamise nr: EL-05	
		Lõpetamise: 1/1	
		Mõõtkava: 1:50	