


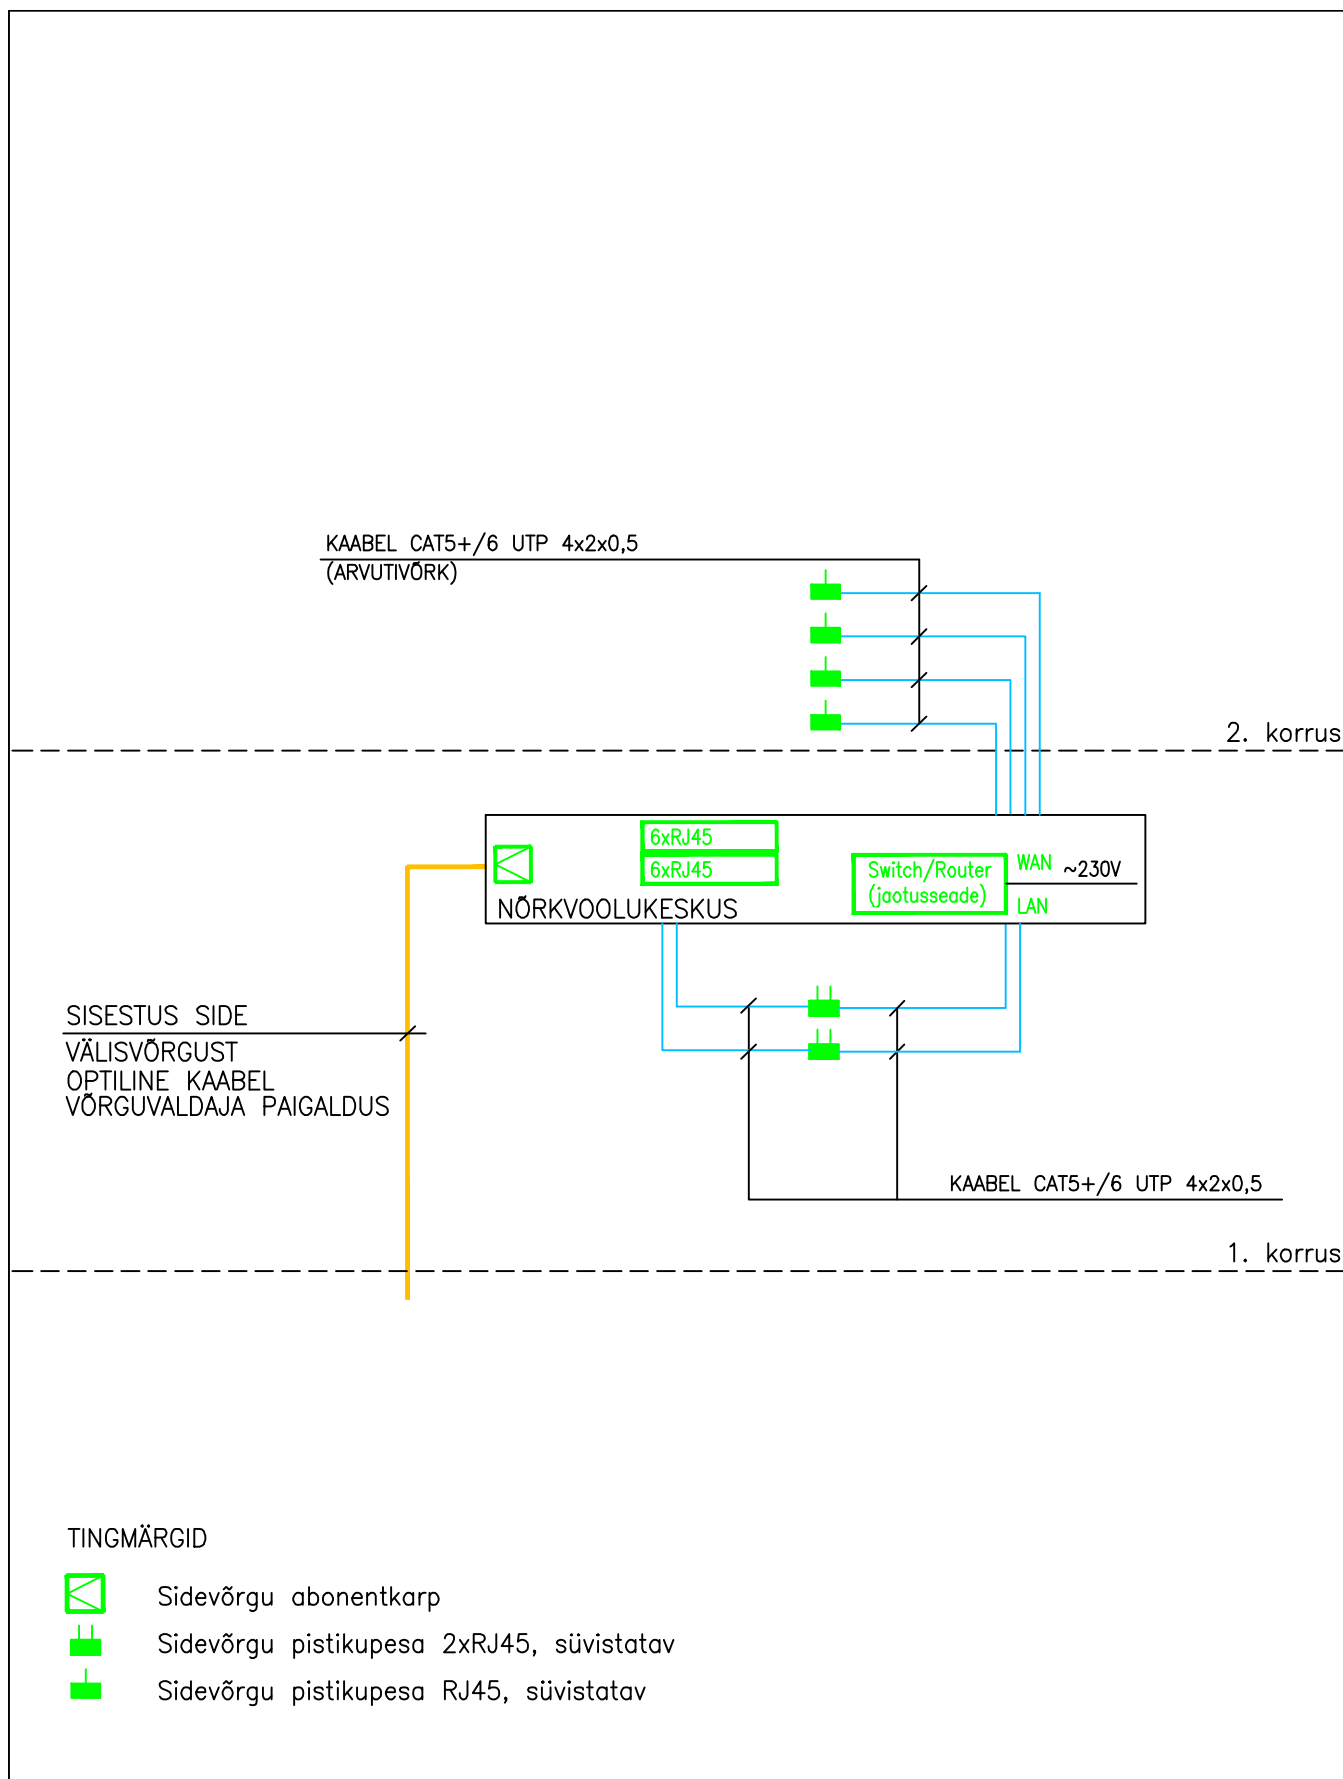

Tellija NOBE OÜ		Töö RIDAELAMU ELEKTRIPAIGALDIS	
Objekt KUU TEE 16, SAKU, SAKU VALD, HARJUMAA			Töö nr. 2417
Joonis BOKS 1 SIDEVÕRGU SKHEEM			
Projekteeris: V. RANNAKIVI	 Maamõõtja tn. 2 76506, Saue Tel 5142331 TEL-000204	Muudatus:	Joonise nr. EN-01
Kontrollis:		Stadium: PÕHIPROJEKT	Leht/lehti: 1/1
Kuupäev: 28.02.2025		Fail: 2417_PP_EN-7-01_v01_Side.sk.boks1	Mõõtkaava: .