


VALGUSTITE TINGMÄRGID		
Tähis	Tingmärk	Nimetus
V-01	⊗	Süvisvalgusti
V-02	⊗	Süvisvalgusti niiskukindel
V-04	⊗	Pinnapealne laevalgusti
V-05	⊗	Tehnoruumi laevalgusti
V-06.1	—	Peegel valgustusega
V-07	⊗	Laevalgusti
V-LED	—	LEDriba valgustus mööblis toide

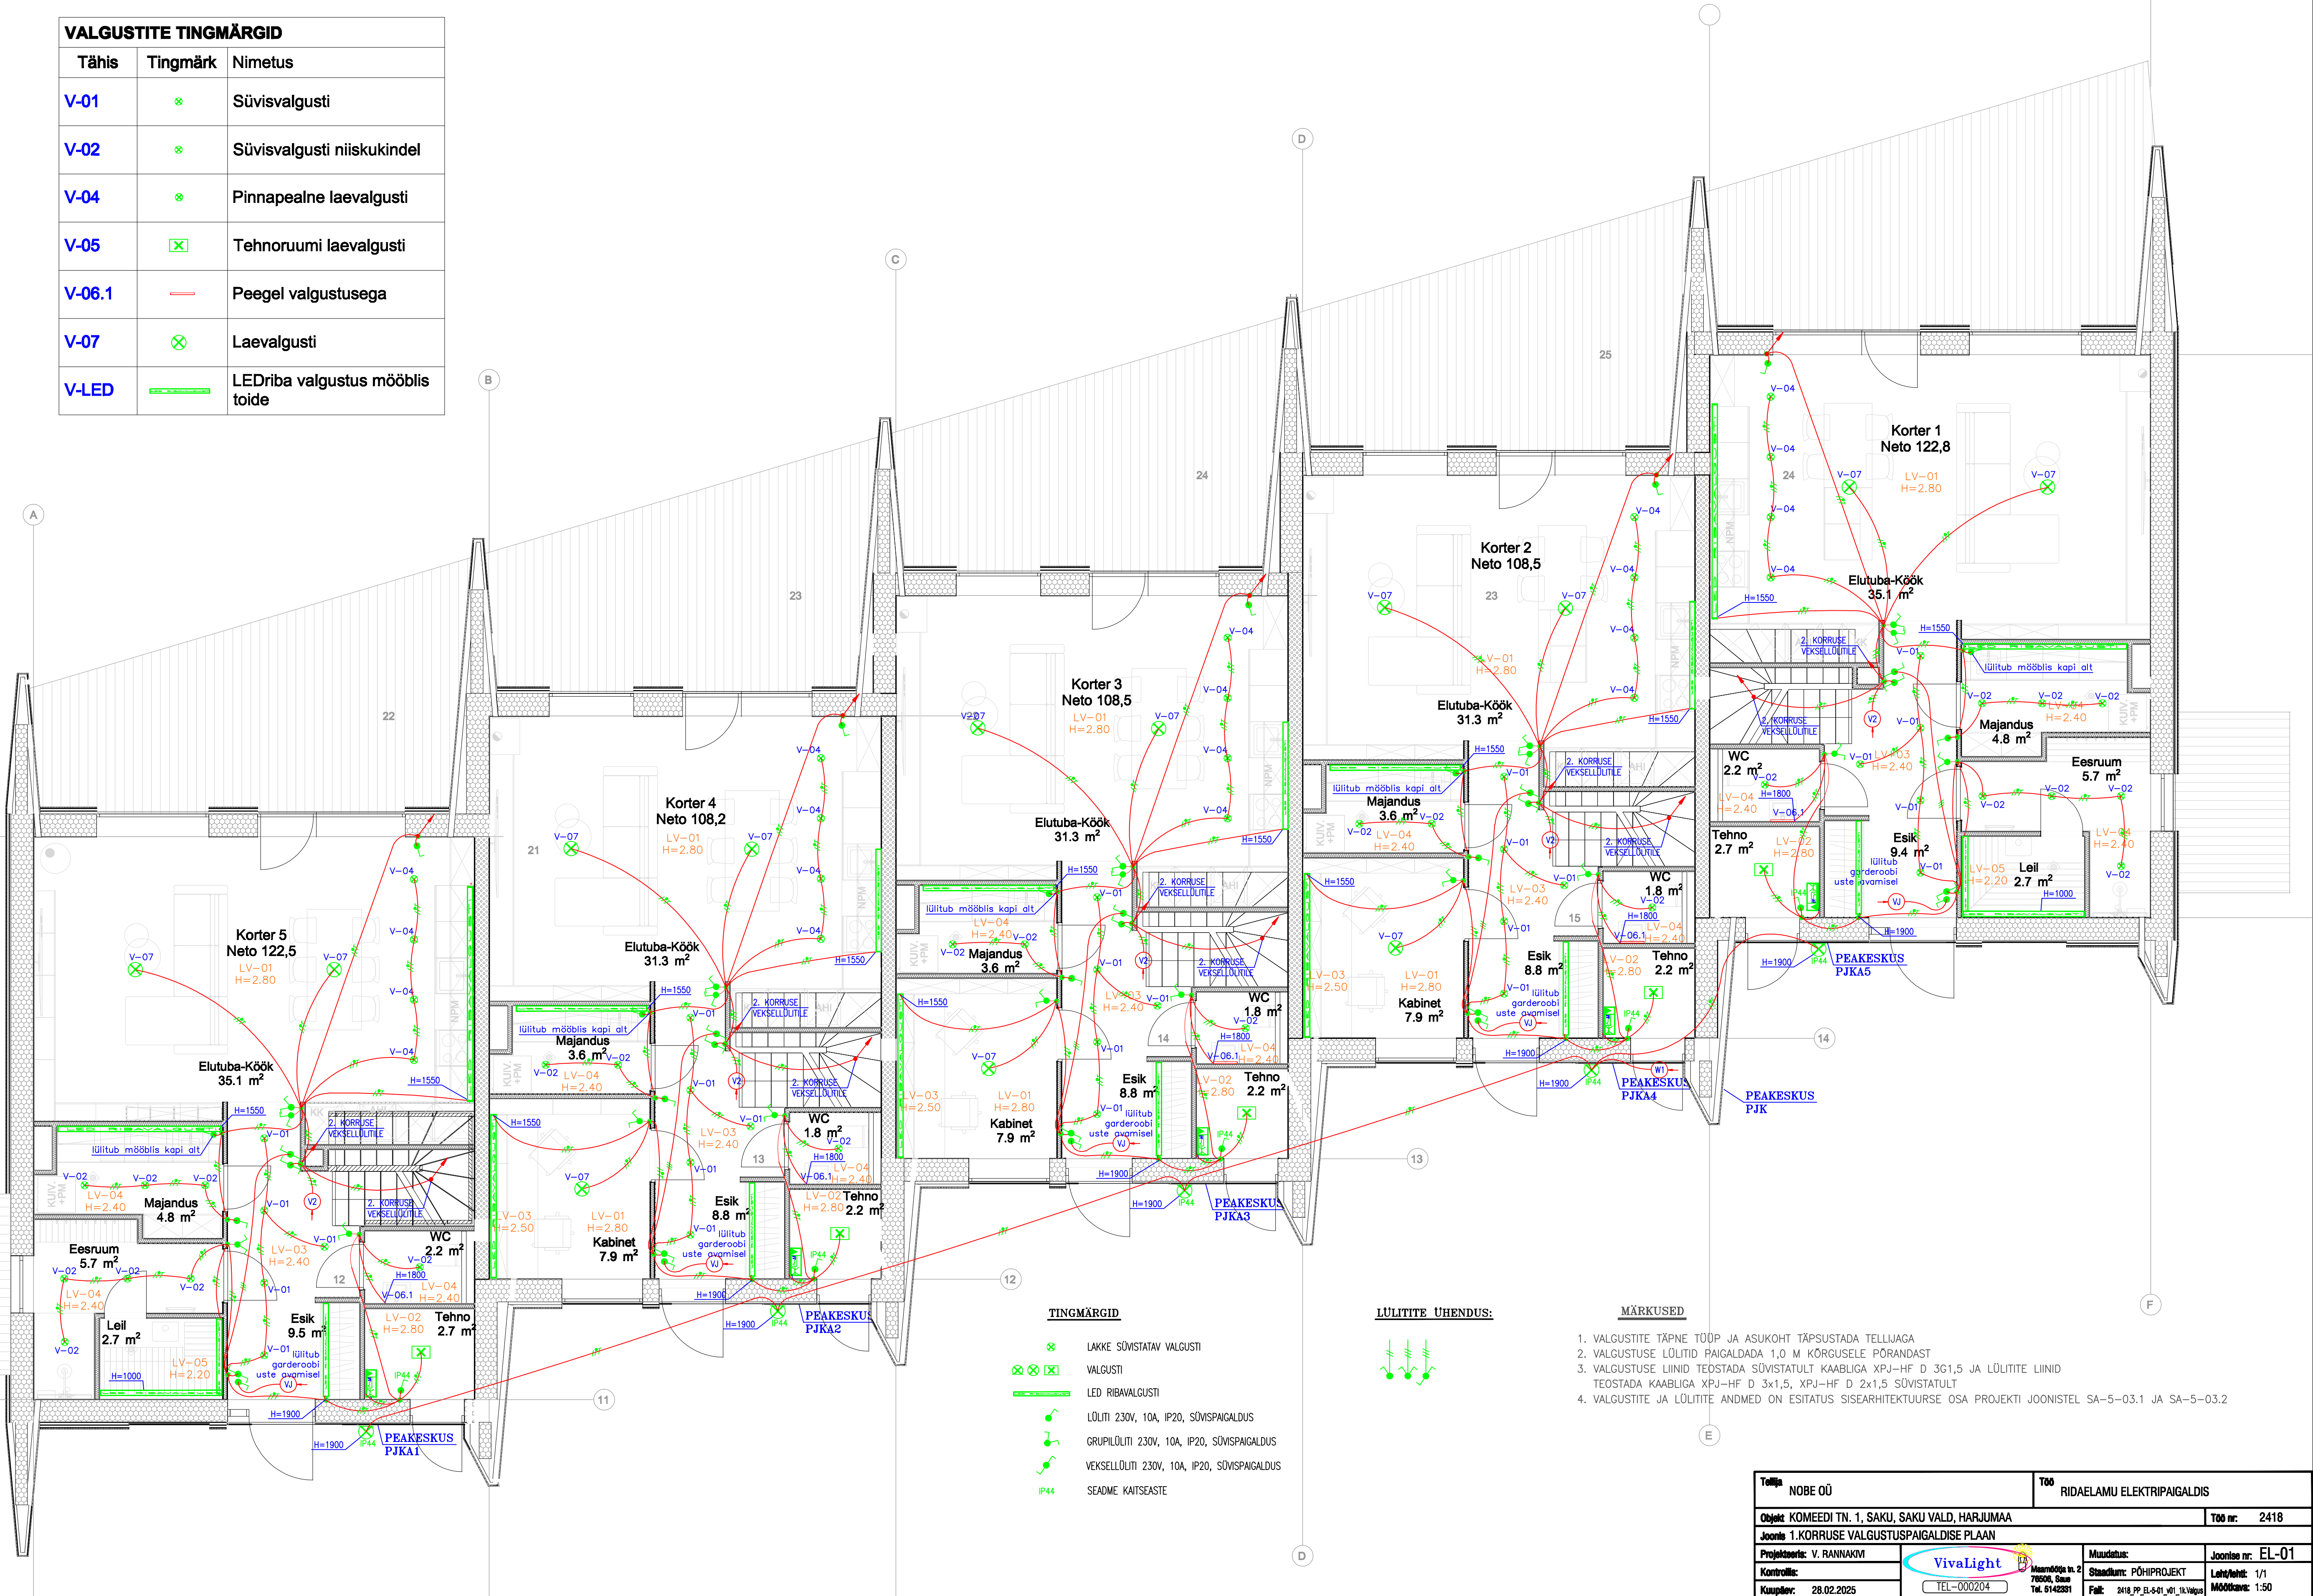

Tööja NOBE OÜ		Töö RIDAELAMU ELEKTRIPAIGALDIS	
Objekt KOMEEDI TN. 1, SAKU, SAKU VALD, HARJUMAA		Töö nr. 2418	
Joonis 1. KORRUSE VALGUSTUSPAIGALDISE PLaan			
Projektoris: V. RANNAKVI	 Maamöödloja nr. 2 76029, 63501 TEL: 000204	Muudatus:	Joonise nr. EL-01
Kontrollis:		Staudium: PÕHIPROJEKT	Lehe/lehti: 1/1
Kuupäev: 28.02.2025		Faht: 2418_PP_EL-01_v01_1x/valgus	Mööblit: 1:50