


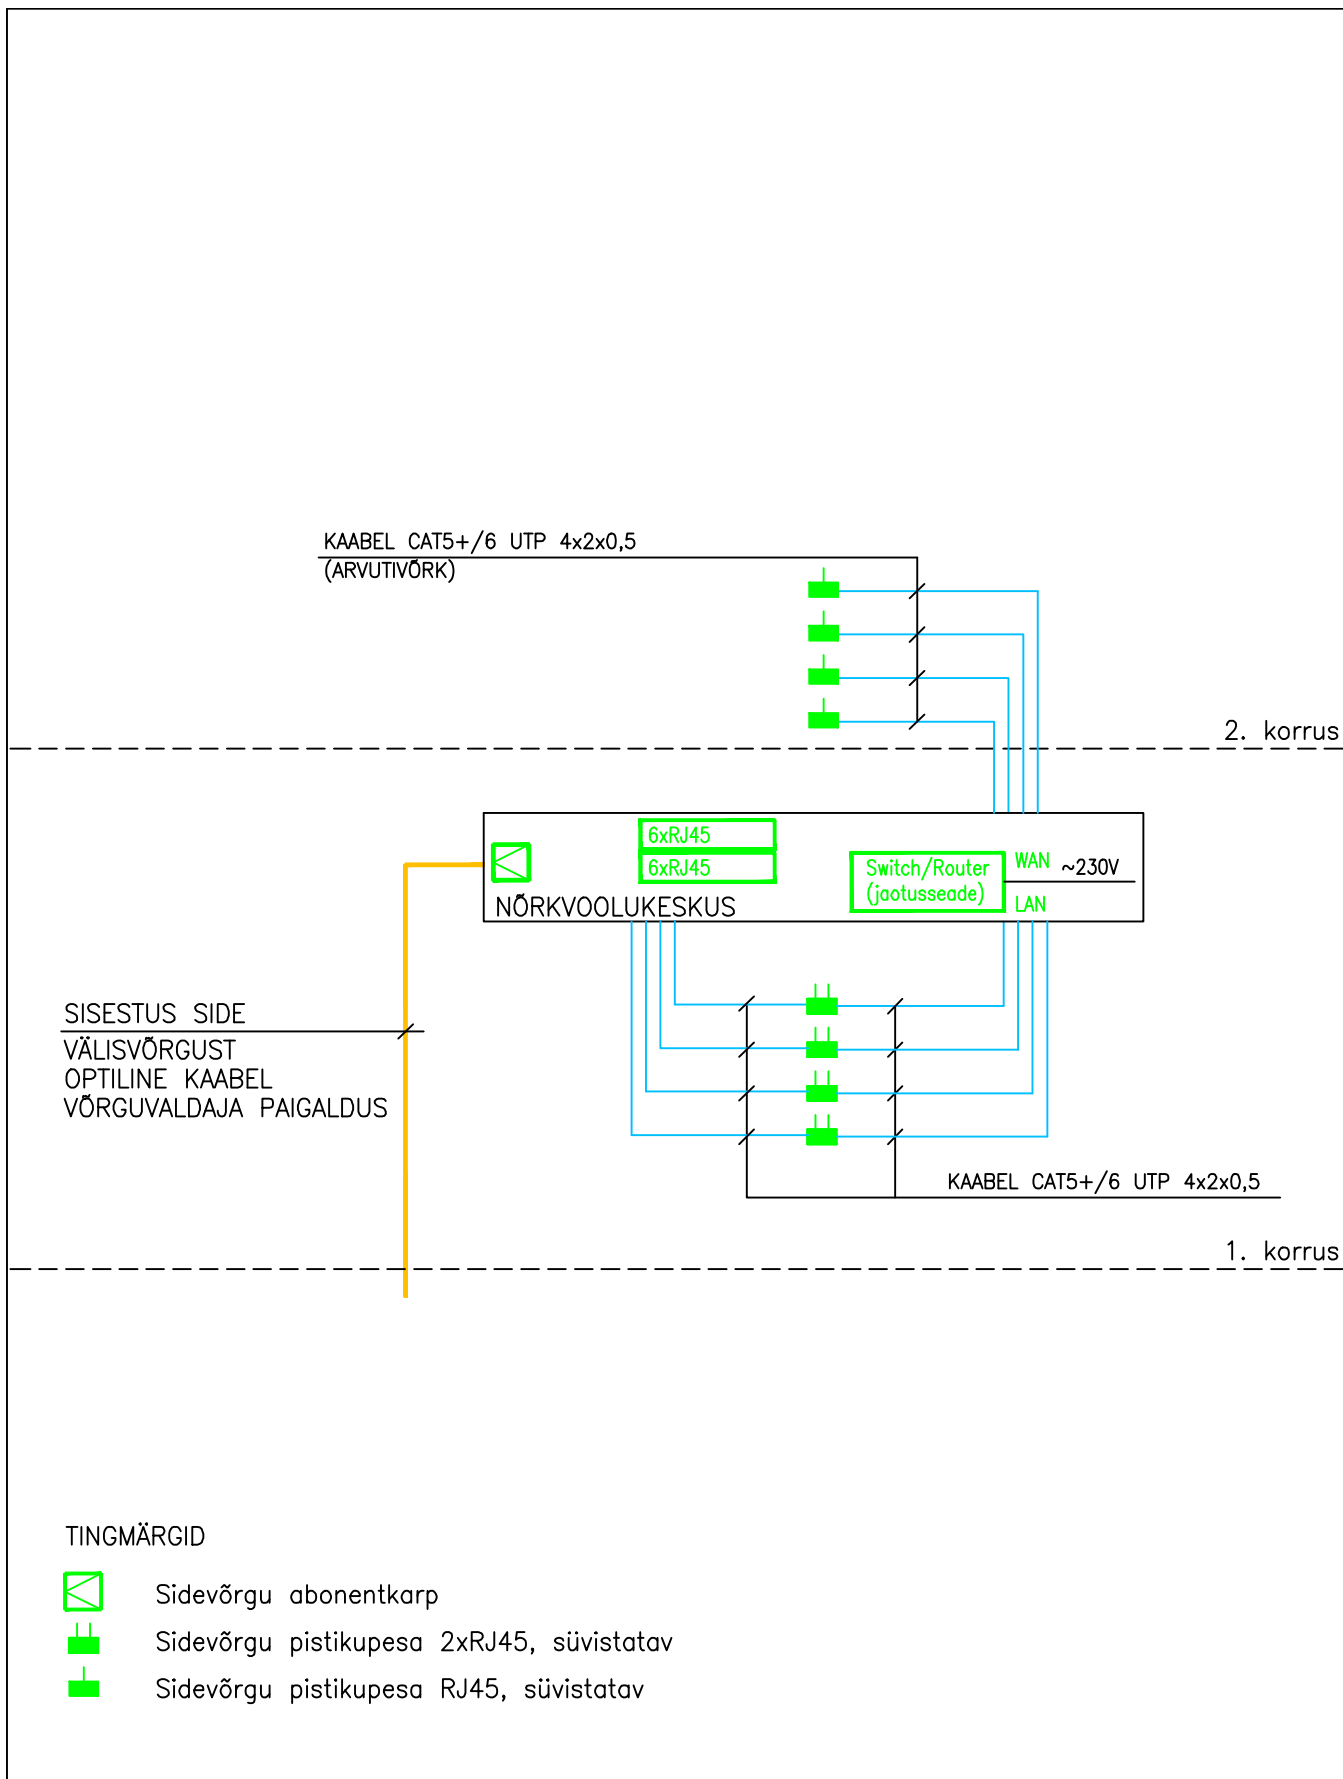

Tellija NOBE OÜ		Töö RIDAELAMU ELEKTRIPAIGALDIS	
Objekt KOMEDI TN. 1, SAKU, SAKU VALD, HARJUMAA			Töö nr. 2418
Joonis BOKS 2 SIDEVÕRGU SKEEM			
Projekteeris: V. RANNAKIVI		Muudatus:	Joonise nr. EN-02
Kontrollis:		Stadium: PÕHIPROJEKT	Leht/lehti: 1/1
Kuupäev: 28.02.2025		Fail: 2418_PP_EN-7-02_v01_Side.sk.boks2	Mõõtka: .