


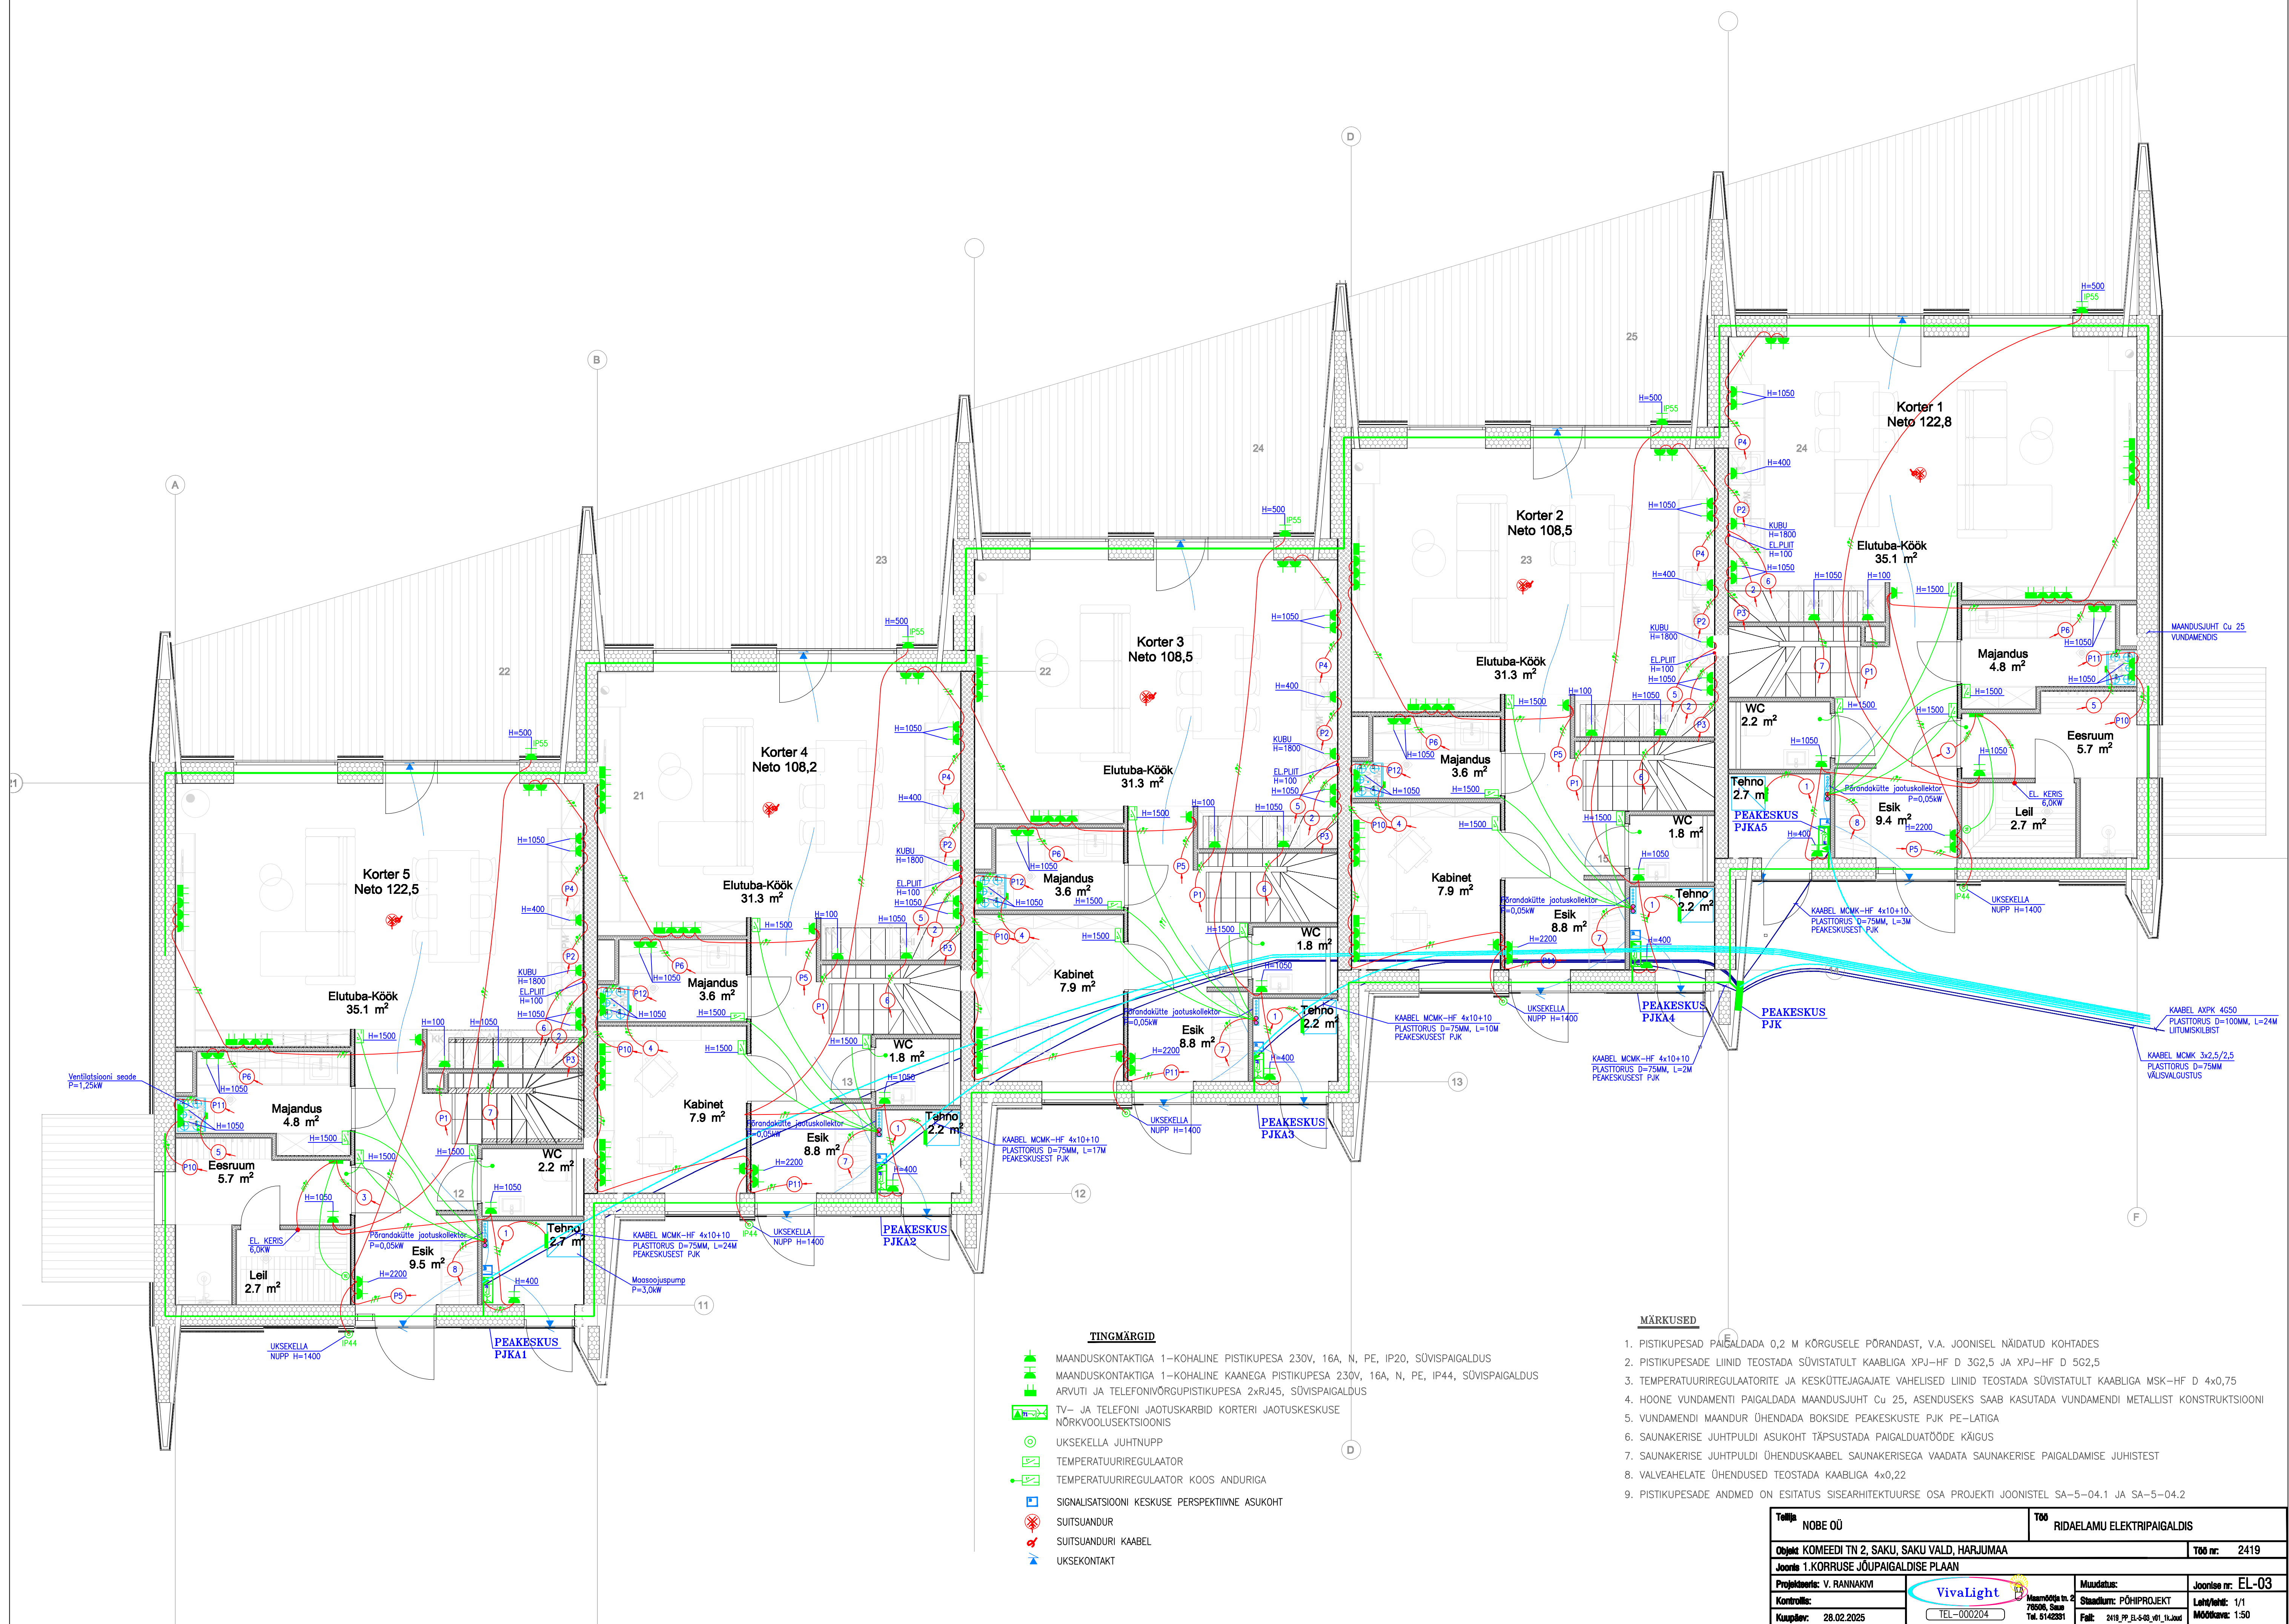

TINGMÄRGID

- MAANDUSKONTAKTIGA 1—KOHALINE PISTIKUPESA 230V, 16A, N, PE, IP20, SÜVISPAGALDUS
- MAANDUSKONTAKTIGA 1—KOHALINE KANEGA PISTIKUPESA 230V, 16A, N, PE, IP44, SÜVISPAGALDUS
- ARVUTI JA TELEFONIVORGUPISTIKUPESA 2xRJ45, SÜVISPAGALDUS
- TV- JA TELEFONI JAOTUSKARPID KORTERI JAOTUSKESKUSE NÕRKVOOLUSEKTSIOONIS
- UKSEKELLA JUHTNUPP
- TEMPERatuurIREGULAATOR
- TEMPERatuurIREGULAATOR KOOS ANDURIGA
- SIGNALISATSIOONI KESKUSE PERSPEKTIVNE ASUKOHT
- SUITSUANDUR
- SUITSUANDURI KAABEL
- UKSEKONTAKT

MÄRKUSED

- PISTIKUPESAD PAIGALDADA 0,2 M KÕRGUSELE PÕRANDAST, V.A. JOONISEL NÄIDATUD KOHTADES
- PISTIKUPESADE LIINID TEOSTADA SÜVISTATULT KAABLIGA XPJ—HF D 3G2,5 JA XPJ—HF D 5G2,5
- TEMPERatuurIREGULAATORITE JA KESKÖTTEJAGAJATE VAHELISED LIINID TEOSTADA SÜVISTATULT KAABLIGA MSK—HF D 4x0,75
- HOONE VUNDAMENTI PAIGALDADA MAANDUSJUHT Cu 25, ASENDUSEKS SAAB KASUTADA VUNDAMENTI METALLIST KONSTRUKTSIOONI
- VUNDAMENTI MAANDUR ÜHENDADA BOKSIDE PEAKESKUSTE PJK PE—LATIGA
- SAUNAKERISE JUHTPULDI ASUKOHT TÄPSUSTADA PAIGALDUÄTÖDE KÄIGUS
- SAUNAKERISE JUHTPULDI ÜHENDUSKAABEL SAUNAKERISEGA VAADATA SAUNAKERISE PAIGALDAMISE JUHISTEST
- VALVEAHELATE ÜHENDUSED TEOSTADA KAABLIGA 4x0,22
- PISTIKUPESADE ANDMED ON ESITATUS SISEARHITEKTUURSE OSA PROJEKTI JOONISTEL SA—5—04.1 JA SA—5—04.2

Tellijä NOBE OÜ		Töö RIDALAMU ELEKTRIPAIGALDIS	
Objekt KOMEDI TN 2, SAKU, SAKU VALD, HARJUMAA		Töö nr: 2419	
Joonis 1.KORRUSE JÕUPAIGALDISE PLAAN			
Projektsuhtaja: V. RAINAKIVI		Muudatus:	Joonise nr: EL-03
Kontrollija:	Staudium: PÕHIPROJEKT	Leht/nr:	1/1
Kuupäev: 28.02.2025	Tel: 000204	Fax: 2419 99 44-03, 011 11 11 11	Mõõtkava: 1:50