


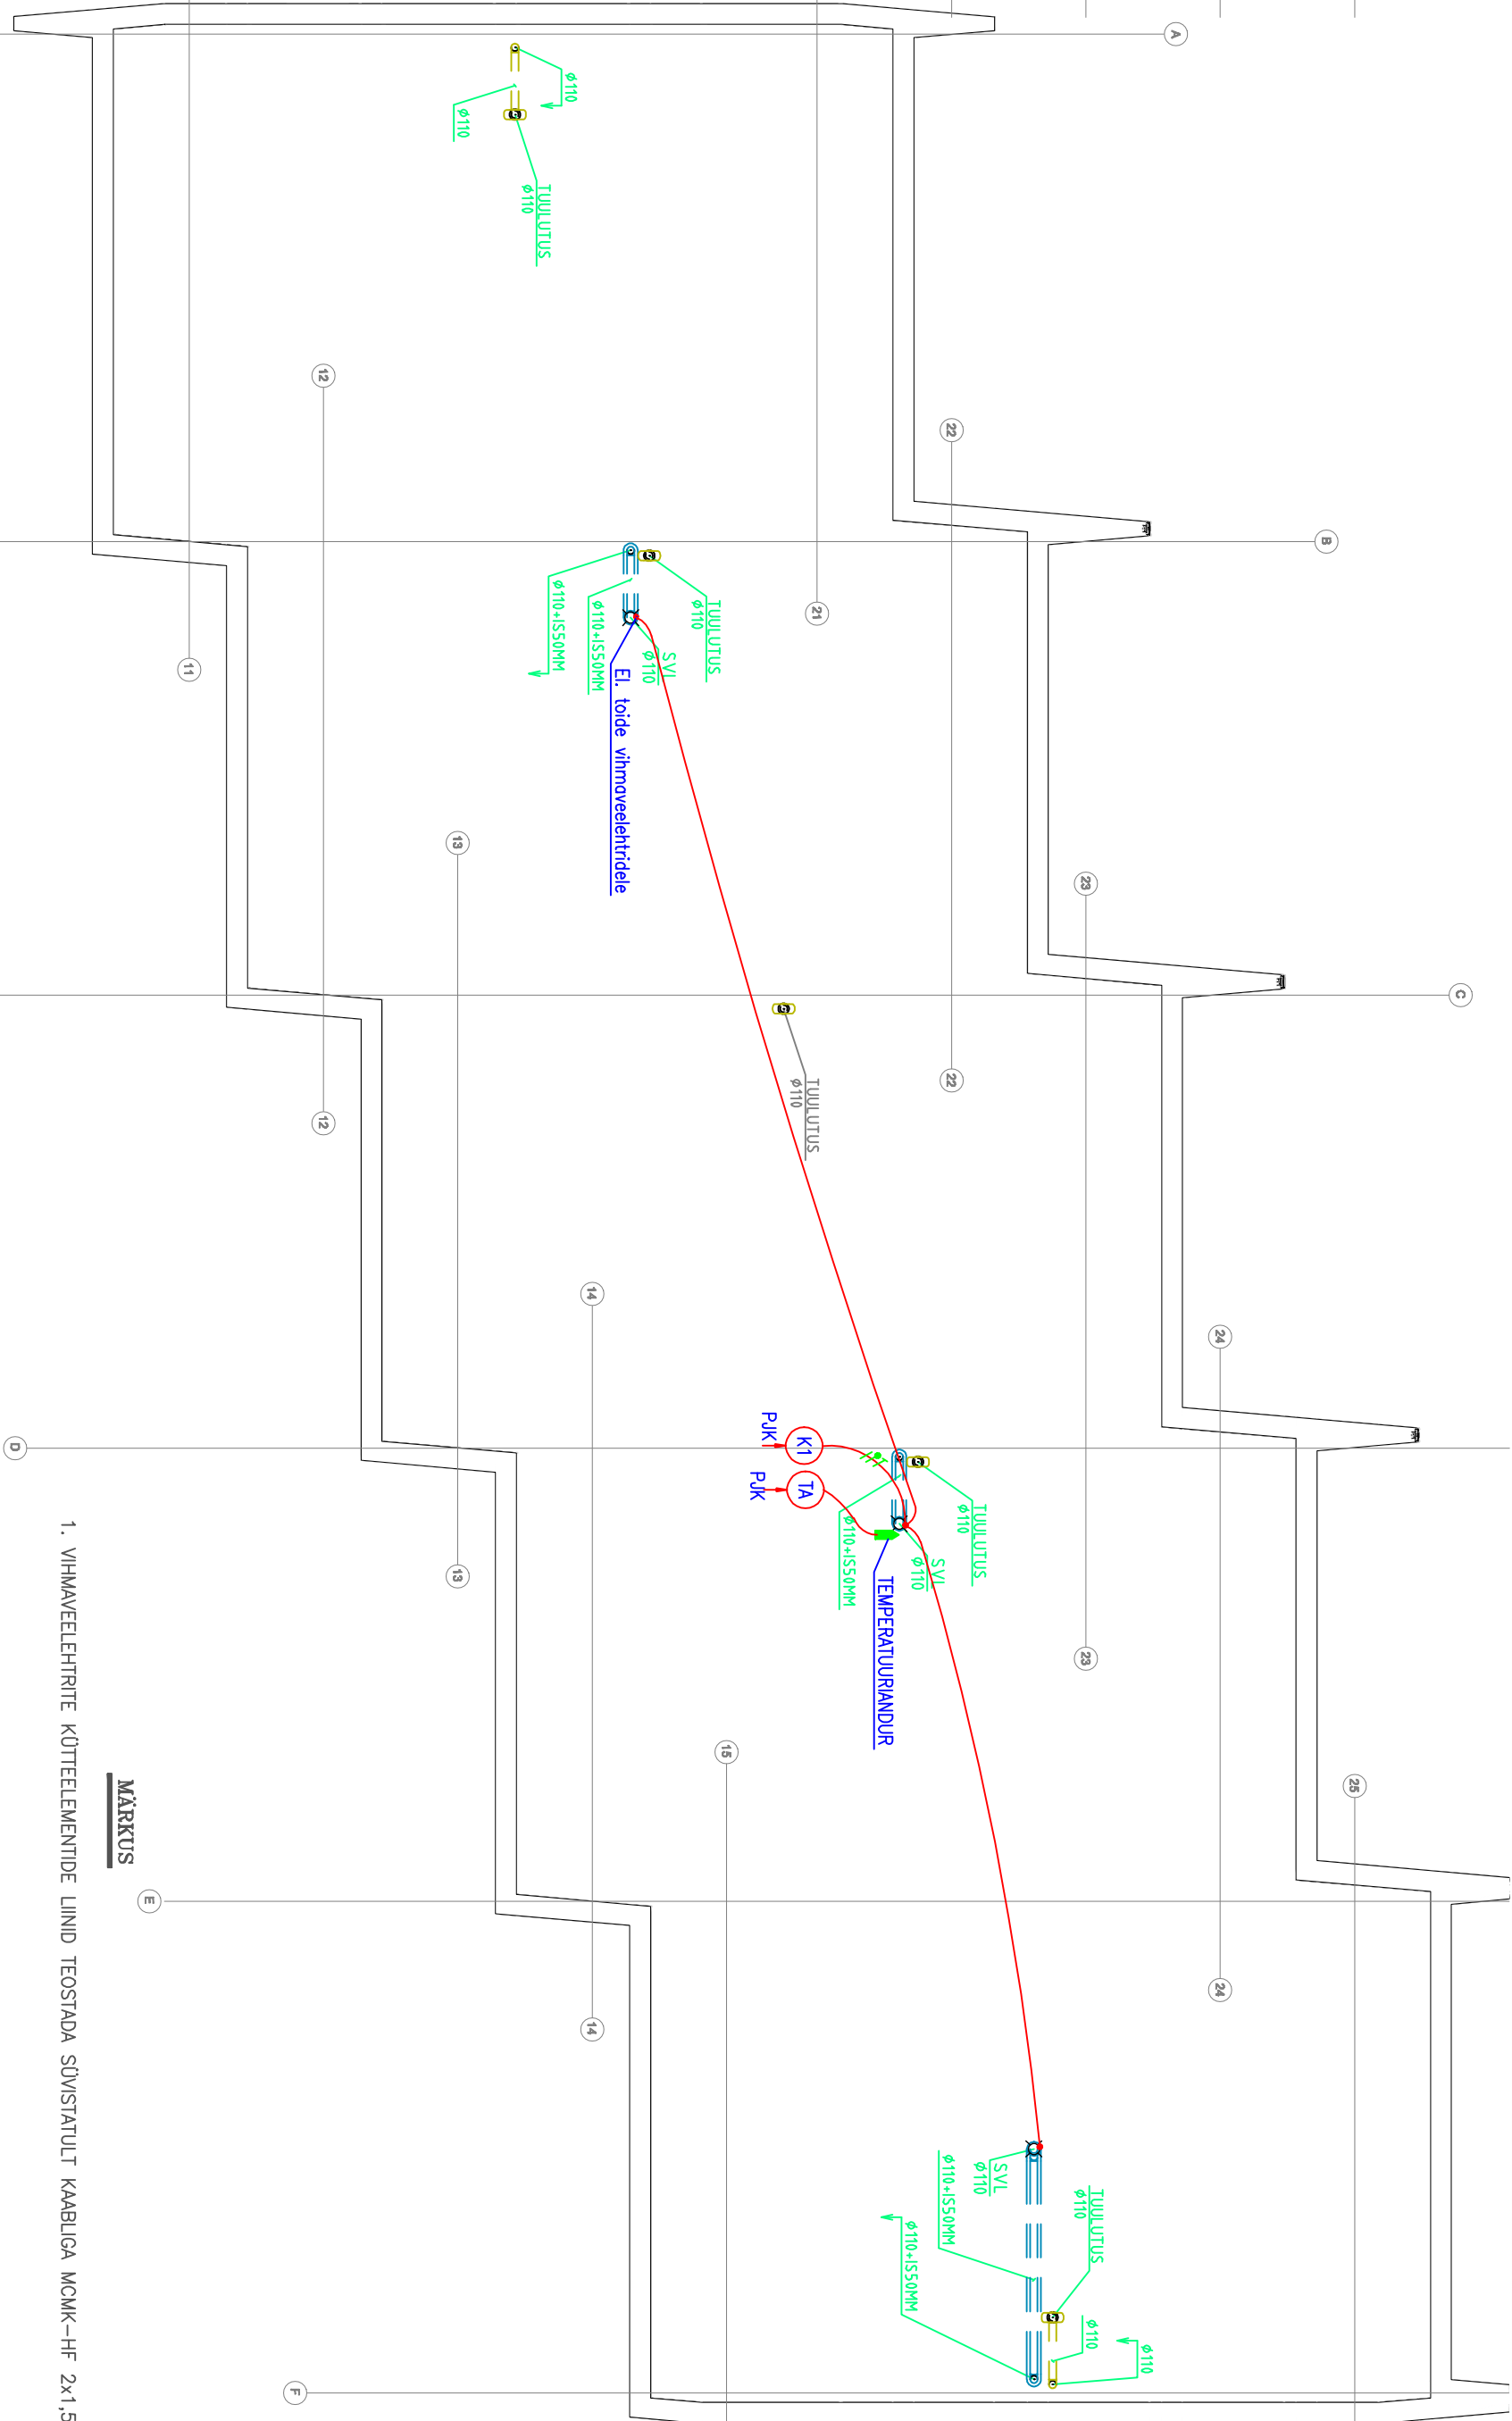

Tellijä NOBE OÜ		Töö RIIÐAELAMU ELEKTRIPAIGALDIS	
Objekt KOMEEDI TN. 2, SAKU, SAKU VALD, HARJUMAA		Töö nr. 2419	
Joonis KATUSE ELEKTRIPAIGALDISSE PLAAN			
Projekteeris: V. RANNAKIVI		Muudatus:	
Kontrollis:		Staadium: PÕHIPROJEKT	
Kujutatud: 28.02.2025		Fail: 2419_PP_EI-5-05_v01_katus.B	
Joonise nr: EL-05		Lõplik: 1/1	
		Mõõtkava: 1:50	

Telija NOBE OÜ

Objekt KOMEEDI TN. 2, SAKU, SAKU VALD, HARJUMAA

Joonis KATUSE ELEKTRIPAIGALDISSE PLAAN

Projekteeris: V. RANNAKIVI

Kontrollis:

Kujutatud: 28.02.2025

Vivalight



Meemõõda tn. 2
76506, Saue
Tel. 5142351

Muudatus:

Staadium: PÕHIPROJEKT

Fail: 2419_PP_EI-5-05_v01_katus.B

Joonise nr: EL-05

Lõplik: 1/1

Mõõtkava: 1:50