



VALGUSTITE TINGMÄRGID		
Tähis	Tingmärk	Nimetus
V-01	✱	Süvisvalgusti
V-02	✱	Süvisvalgusti niiskukindel
V-04	✱	Pinnapealne laevalgusti
V-05	✱	Tehnoruumi laevalgusti
V-06.1	—	Peegel valgustusega
V-07	⊗	Laevalgusti
V-LED	—	LEDriba valgustus mööblis toide

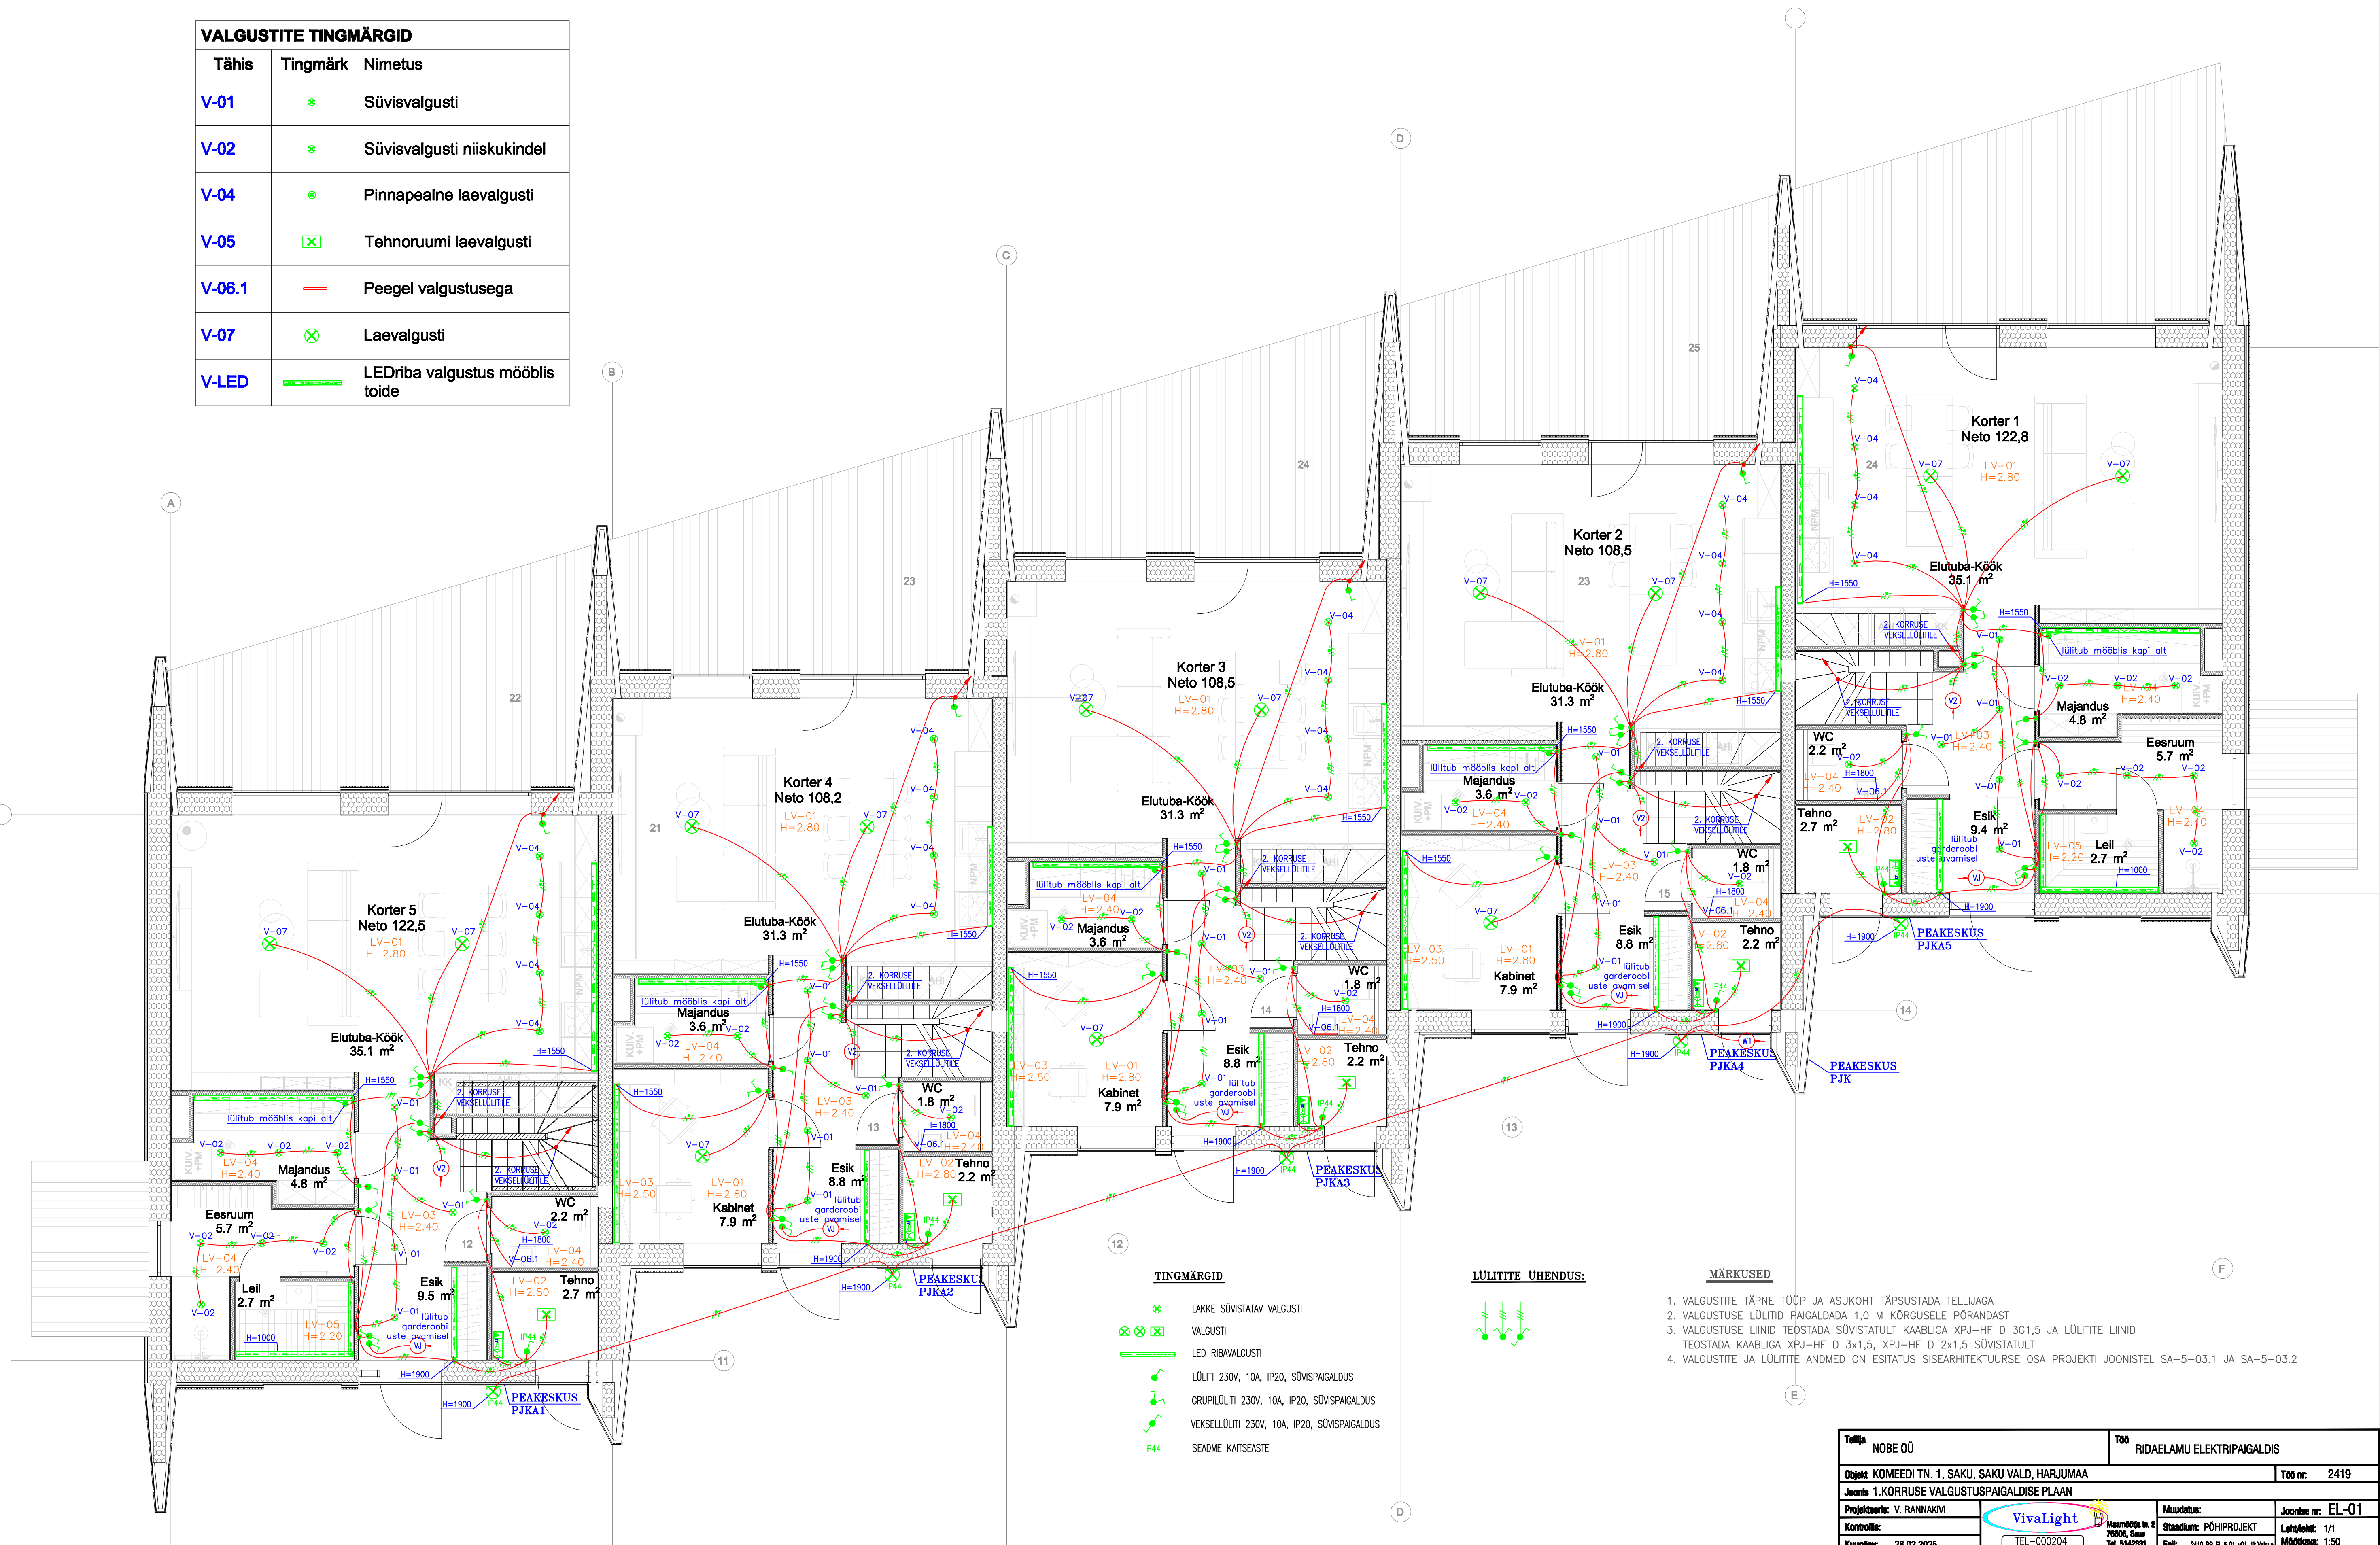

TINGMÄRGID

- ✱ LAKKE SÖVISTATAV VALGUSTI
- ✱ VALGUSTI
- LED RIBAVALGUSTI
- LÜLTI 230V, 10A, IP20, SÖVISPAGALDUS
- GRUPILÜTI 230V, 10A, IP20, SÖVISPAGALDUS
- VEKSELLÜTI 230V, 10A, IP20, SÖVISPAGALDUS
- IP44 SEADME KAITSEASTE

LÜLITITE ÜHENDUS:

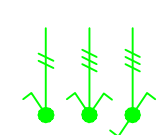

MÄRKUSED

- VALGUSTITE TÄPNE TÖÖP JA ASUKOHT TÄPSUSTADA TELLUAGA
- VALGUSTUSE LÜLTIID PAIGALDADA 1,0 M KÕRGUSELE PÖRANDAST
- VALGUSTUSE LIINID TÕESTADA SÖVISTATULT KAABLIGA XPJ-HF D 3G1,5 JA LÜLITITE LIINID TÕESTADA KAABLIGA XPJ-HF D 3x1,5, XPJ-HF D 2x1,5 SÖVISTATULT
- VALGUSTITE JA LÜLITITE ANDMED ON ESITATUS SISEARHITEKTUURSE OSA PROJEKTI JOONISTEL SA-5-03.1 JA SA-5-03.2

Tööaja NOBE OÜ		Töö RIDAELAMU ELEKTRIPAIGALDIS	
Objekt KOMEDI TN. 1, SAKU, SAKU VALD, HARJUMAA		Töö nr: 2419	
Joonis 1.KÕRRUSE VALGUSTUSPAIGALDISE PLaan			
Projektoris: V. RANNAKVI		Muudatus:	Joonise nr: EL-01
Kontrollis:		Staudium: PÕHIPROJEKT	Lehe/lehti: 1/1
Kuupäev: 28.02.2025		Faht: 2419_PP_EL-01_v01_1x/Valgus	Mööblid: 1:50