
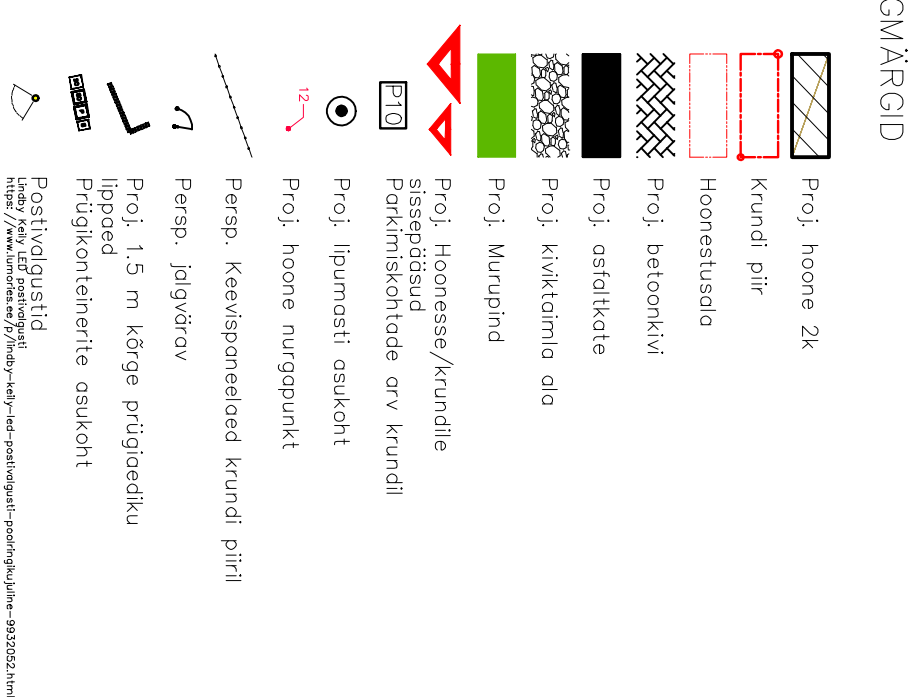


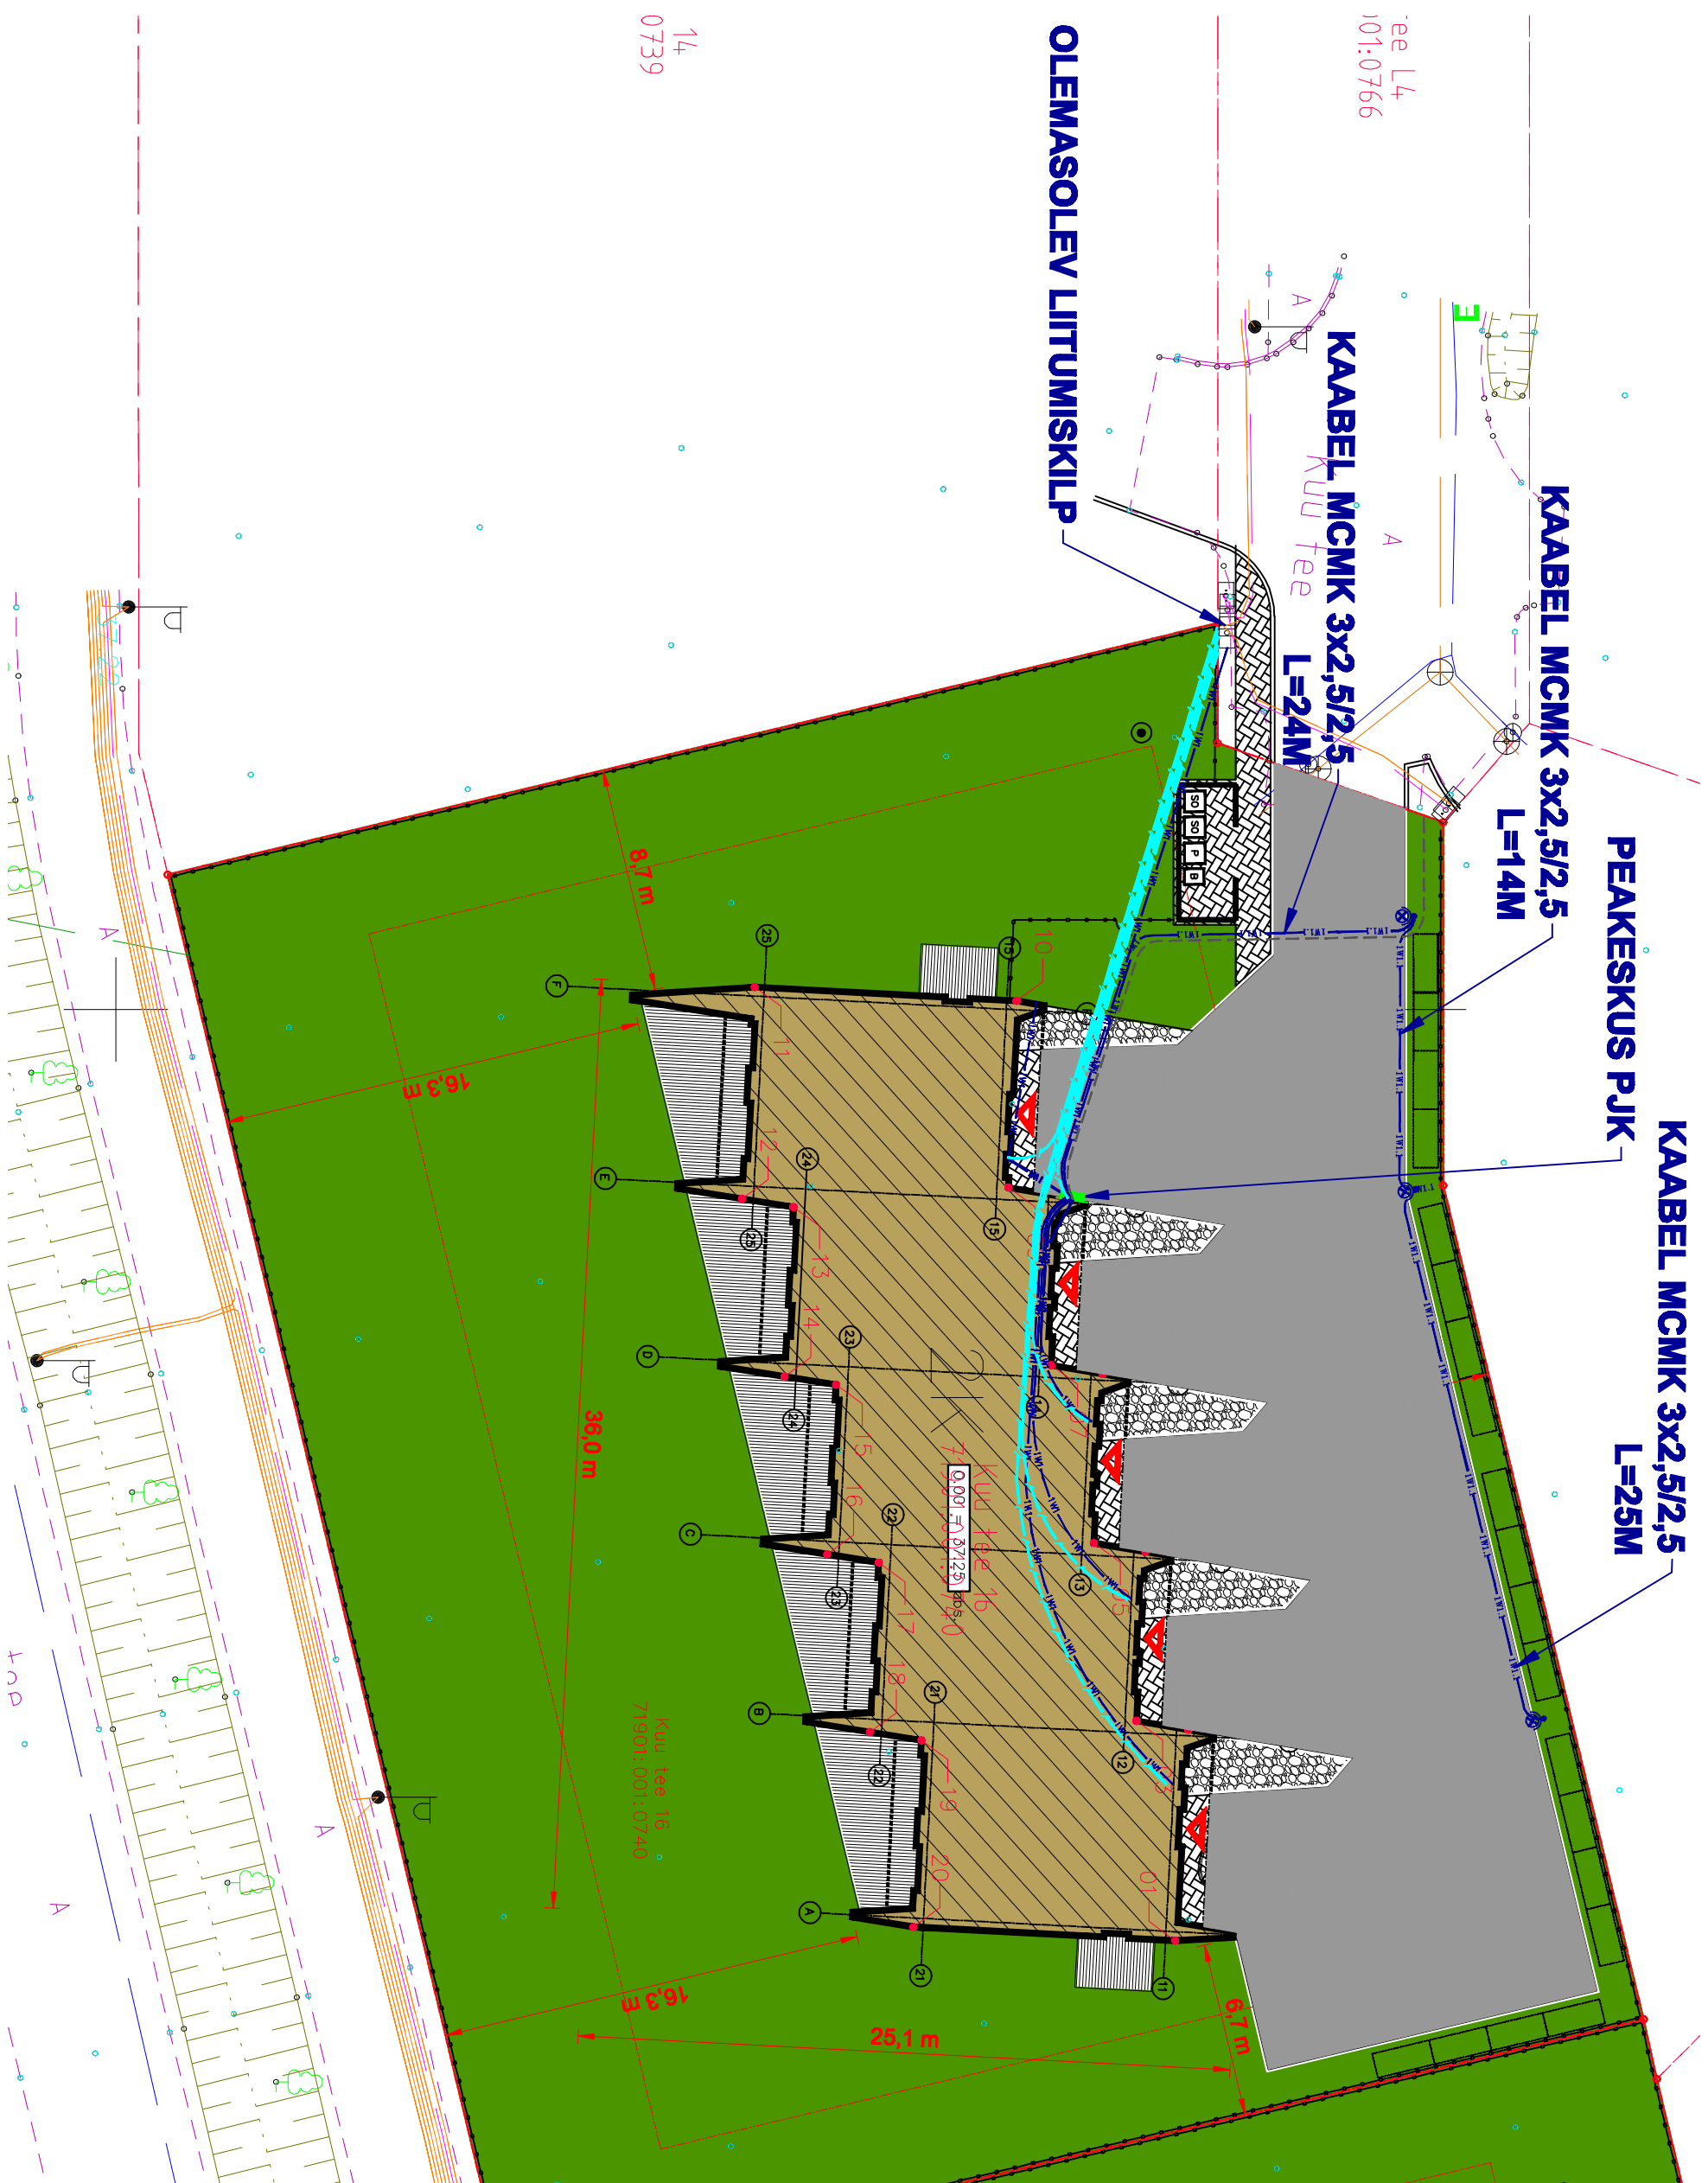

VÄLISPAIGALDISE TINGMÄRGID:

- 
 PROJEKTEERITUD 0,6/1KV, KAABEL MAAS, PLASTTORUS d=100mm, 750N

 PROJEKTEERITUD VALISVALGUSTUSE 0,6/1KV

 KAABEL MAAS, PLASTTORUS d=75mm, 750N

 PROJEKTEERITUD PLASTTORU d=50mm, 750N

 OLEMA SOLEV LITUMISKUP
- 
 PROJEKTEERITUD VALISVALGUSTUSE POSTIL, H=4 M

 PROJEKTEERITUD SIDEKANALISATSIOONI PLASTORU UPOTEL, A d=50mm

Telliisa		Tööb	
NOBE OÜ		RIDAELAMU ELEKTRIPAIGALDIDS	
Objekt KUU TEE 16, SAKU, SAKU VALD, HARJUMAA		Tööd nr. 2417	
Joonis VÄLISPAIGALDISE PLAAK			
Projekteeris: V. RANNAKIVI	Määratlus:		Joonis nr. ELV-01
Kontrollis:	Staadium: Põhiprojekt		Leht/lehti: 1/1
Kuupäev: 28.02.2025	Fotit: 2417 PVLV-501, vnt. Pann		Mõõtkava: 1:500