


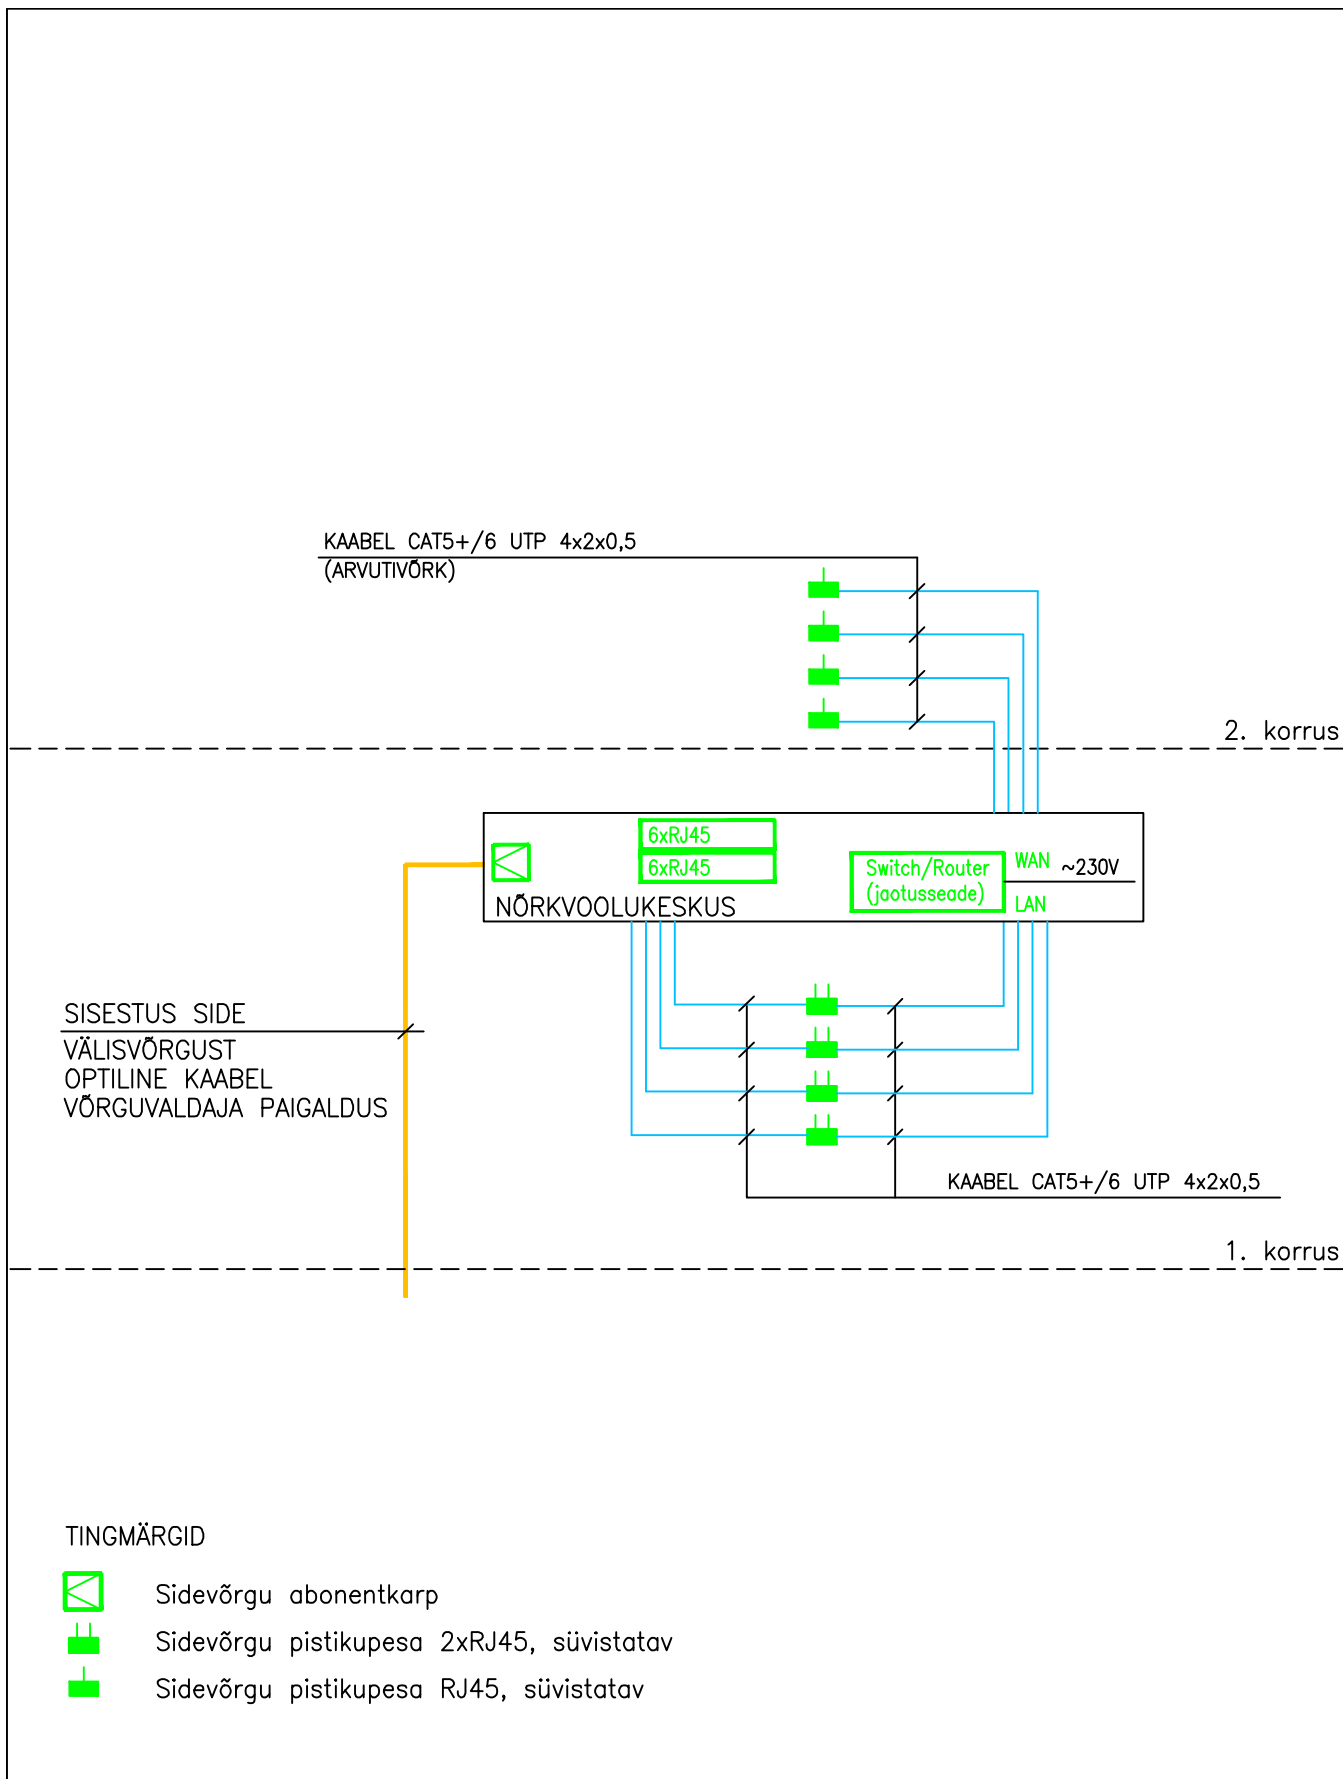

Tellija NOBE OÜ		Töö RIDAELAMU ELEKTRIPAIGALDIS	
Objekt KUU TEE 16, SAKU, SAKU VALD, HARJUMAA			Töö nr. 2417
Joonis BOKS 4 SIDEVÕRGU SKEEM			
Projekteeris: V. RANNAKIVI		Muudatus:	Joonise nr. EN-04
Kontrollis:		Stadium: PÕHIPROJEKT	Leht/lehti: 1/1
Kuupäev: 28.02.2025		Fail: 2417_PP_EN-7-04_v01_Side.sk.boks4	Mõõtka: .