


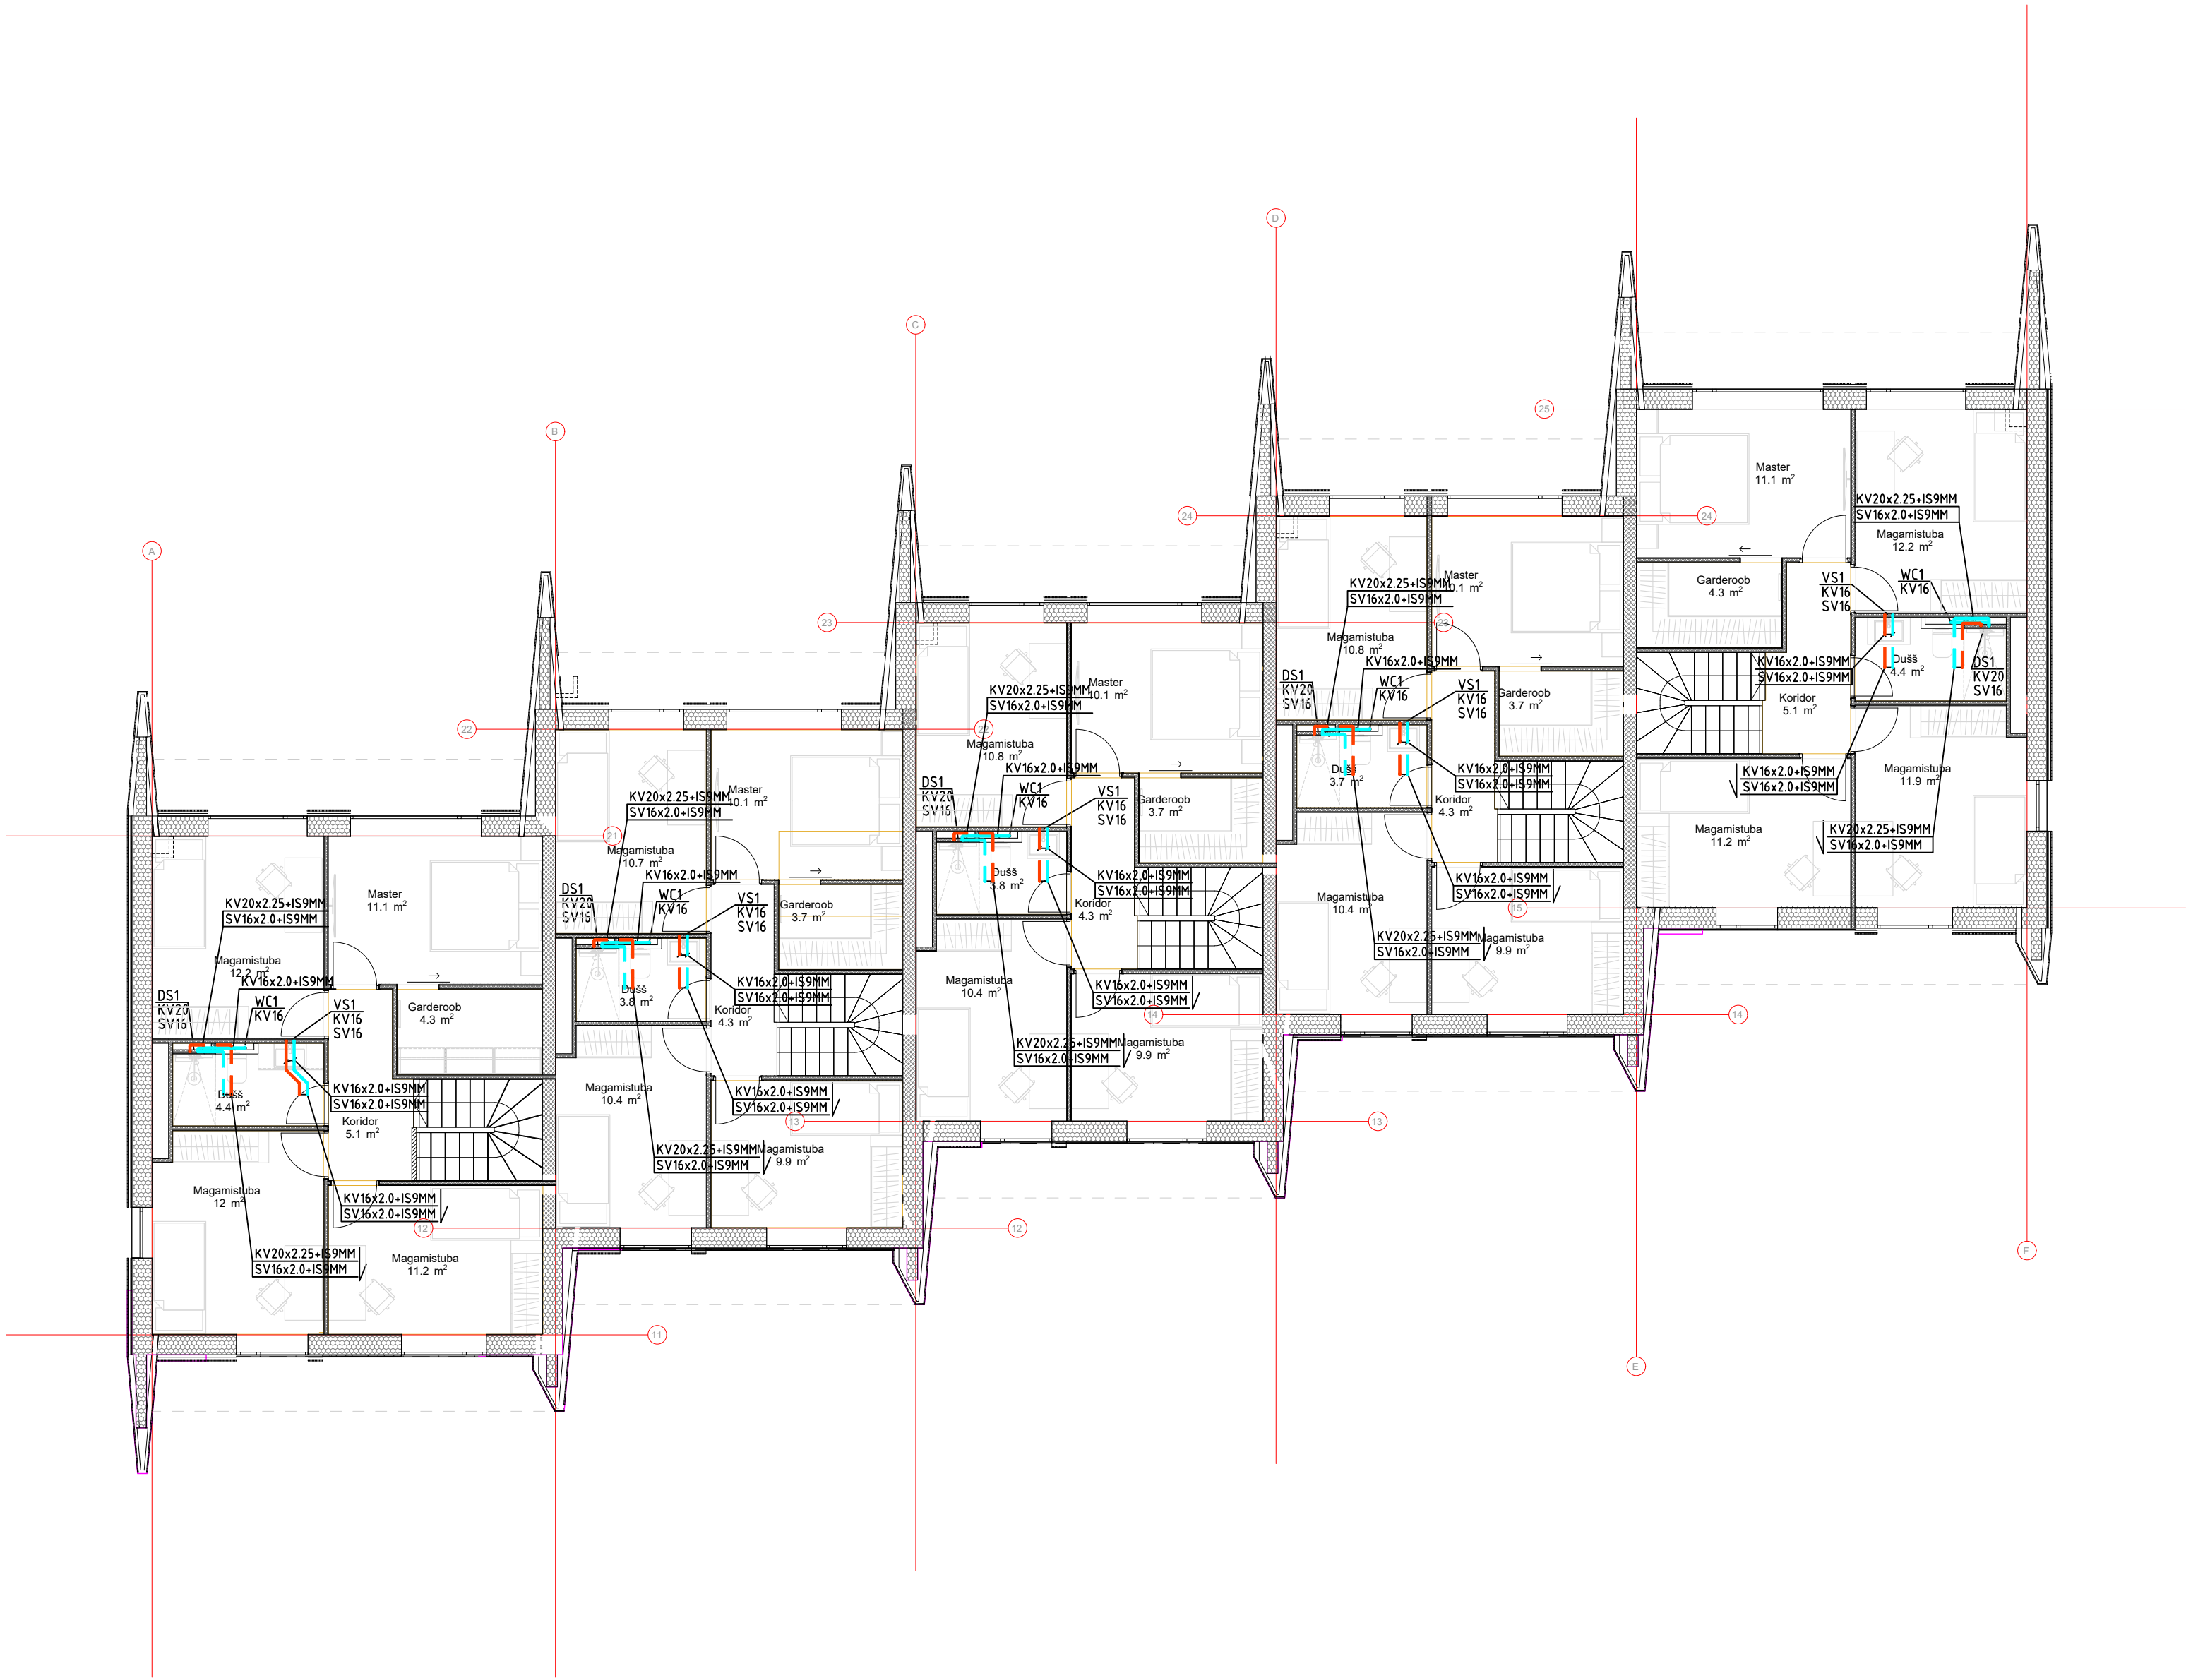

TABEL 1. TORUDE KINNITUSKAUGUSED (+20°C)						
PLASTTORUD de, mm	PVC, PEH, PEM mm		PEX mm		Komposiittoru de, mm	
	HORISONTAAL	VERTIKAAL	HORISONTAAL	VERTIKAAL	HORISONTAAL	VERTIKAAL
<20	700	700	300	300	1200	1500
20	700	800	300	300	1300	1700
25	900	1000	400	400	1300	2000
32	1000	1300	400	400	1400	2100
40	1100	1600	500	500	1400	2200
50	1200	2000	500	500	1500	2600
≥63	1500	2000	600	600	1500	2850

- MÄRKUSED
1. PROJEKTEERITUD MAJANDUS-JOOGIVEESÜSTEEMI VEETORUD MONTEERIDA NT. VEEVARUSTUSE KIHITSEIN-PLASTTORUDEST.
 2. PROJEKTEERITUD VEETORUSTIKUNA KASUTADA EELISOLEERITUD TORUSTIKU.
 3. VEEVÕTUSEADMETE ÜHENDUSED TEHA TORUGA Ø16x2.0 (DUŠSIDE KÜLMAVEE ÜHENDUSED TORUGA Ø20x2.25)
 4. VEETORUSTIKUD PAIGALDADA RIPPLAE PEALE, KUI JOONISEL EI OLE TEISITI NÄIDATUD.
 5. ÜHENDUSTORUSTIKUD SANITAARSEADMETEGA PAIGALDADA SÜVISTATULT HÜLSIS PÖRANDA VÕI SEINAKONSTRUKTSIOONI SISSE.
 6. PLASTTORUDE LÄBIVIIGUD TULETÖKKETARINDIST VARUSTADA TULETÖKKEMANSETTIDEGA, TULETÖKKEMÄHISTEGA VÕI TORUD KUNI Ø50 mm SPETSIAALSE TULETÖKKE SILIKOONIGA.
 7. TORUSTIKU LÄBIVIIGUDE TEGEMISEL TULEB JÄLGIDA KONSTRUKTIIVSE JA ARHITEKTUURSE OSA JOONISEID.
 8. TORUSTIKE PAIGALDAMISEL ARVESTADA TEISTE ERISADEGA.
 9. KÖÖGIVALAMU KÕRVAL PAIKNEVA NÕUDEPESUMASINA VEEÜHENDUS TEOSTADA KÖÖGIVALAMU KRAANIPÕLVEST.
 10. PRESSITUD LIITMIKEGA TORUSTIKE PUHL KASUTADA LEKKETUVASTUSSÜSTEEMIGA LIITMIKKE (LEAK BEFORE PRESS FUNCTION), MIS TUVASTAVAD LEKKE, KUI LIITMIK POLE PRESSITUD.

- TINGMÄRGID
- PROJEKTEERITUD KÜLMAVEE TORUSTIK PÖRANDAS (KV)
 - PROJEKTEERITUD SOOJAVEE TORUSTIK PÖRANDAS (SV)
 - PROJEKTEERITUD KÜLMAVEE TORUSTIK LAE ALL (KV)
 - PROJEKTEERITUD SOOJAVEE TORUSTIK LAE ALL (SV)
 - VS1 – VALAMU SEGISTI
 - DS1 – DUSHISEGISTI
 - WC1 – WC-POTI ÜHENDUS

Tähis	Muudatus	Teostaja	Kuupäev
TÖÖ NIMETUS RIDAELAMU		TELLUA SAKU ARENDUS OÜ	
Aadress KOMEEDI TN 1, SAKU, SAKU VALD, HARJUMAA		JOONIS VEEVARUSTUS. 2-KORRUS	
Smart Pipes OÜ Registrikood 11975396 tel +372 628 8802 info@smartpipes.ee Majaka tn 44-9, Tallinn, Harjumaa, 11412 MTR EEP001966, EPE000622		VASTUTAV SPETSIALIST V.LOORENTS PROJEKTEERUA V.LOORENTS OSA VK	kuupäev 16.03.2025
FAILI NIMI 24060_VK_2-korrus-bind.dwg		TÖÖ NR 24060-2	MOOTKAVA 1:100
		JOONISE NR VK-2	JOONISTE ARV