


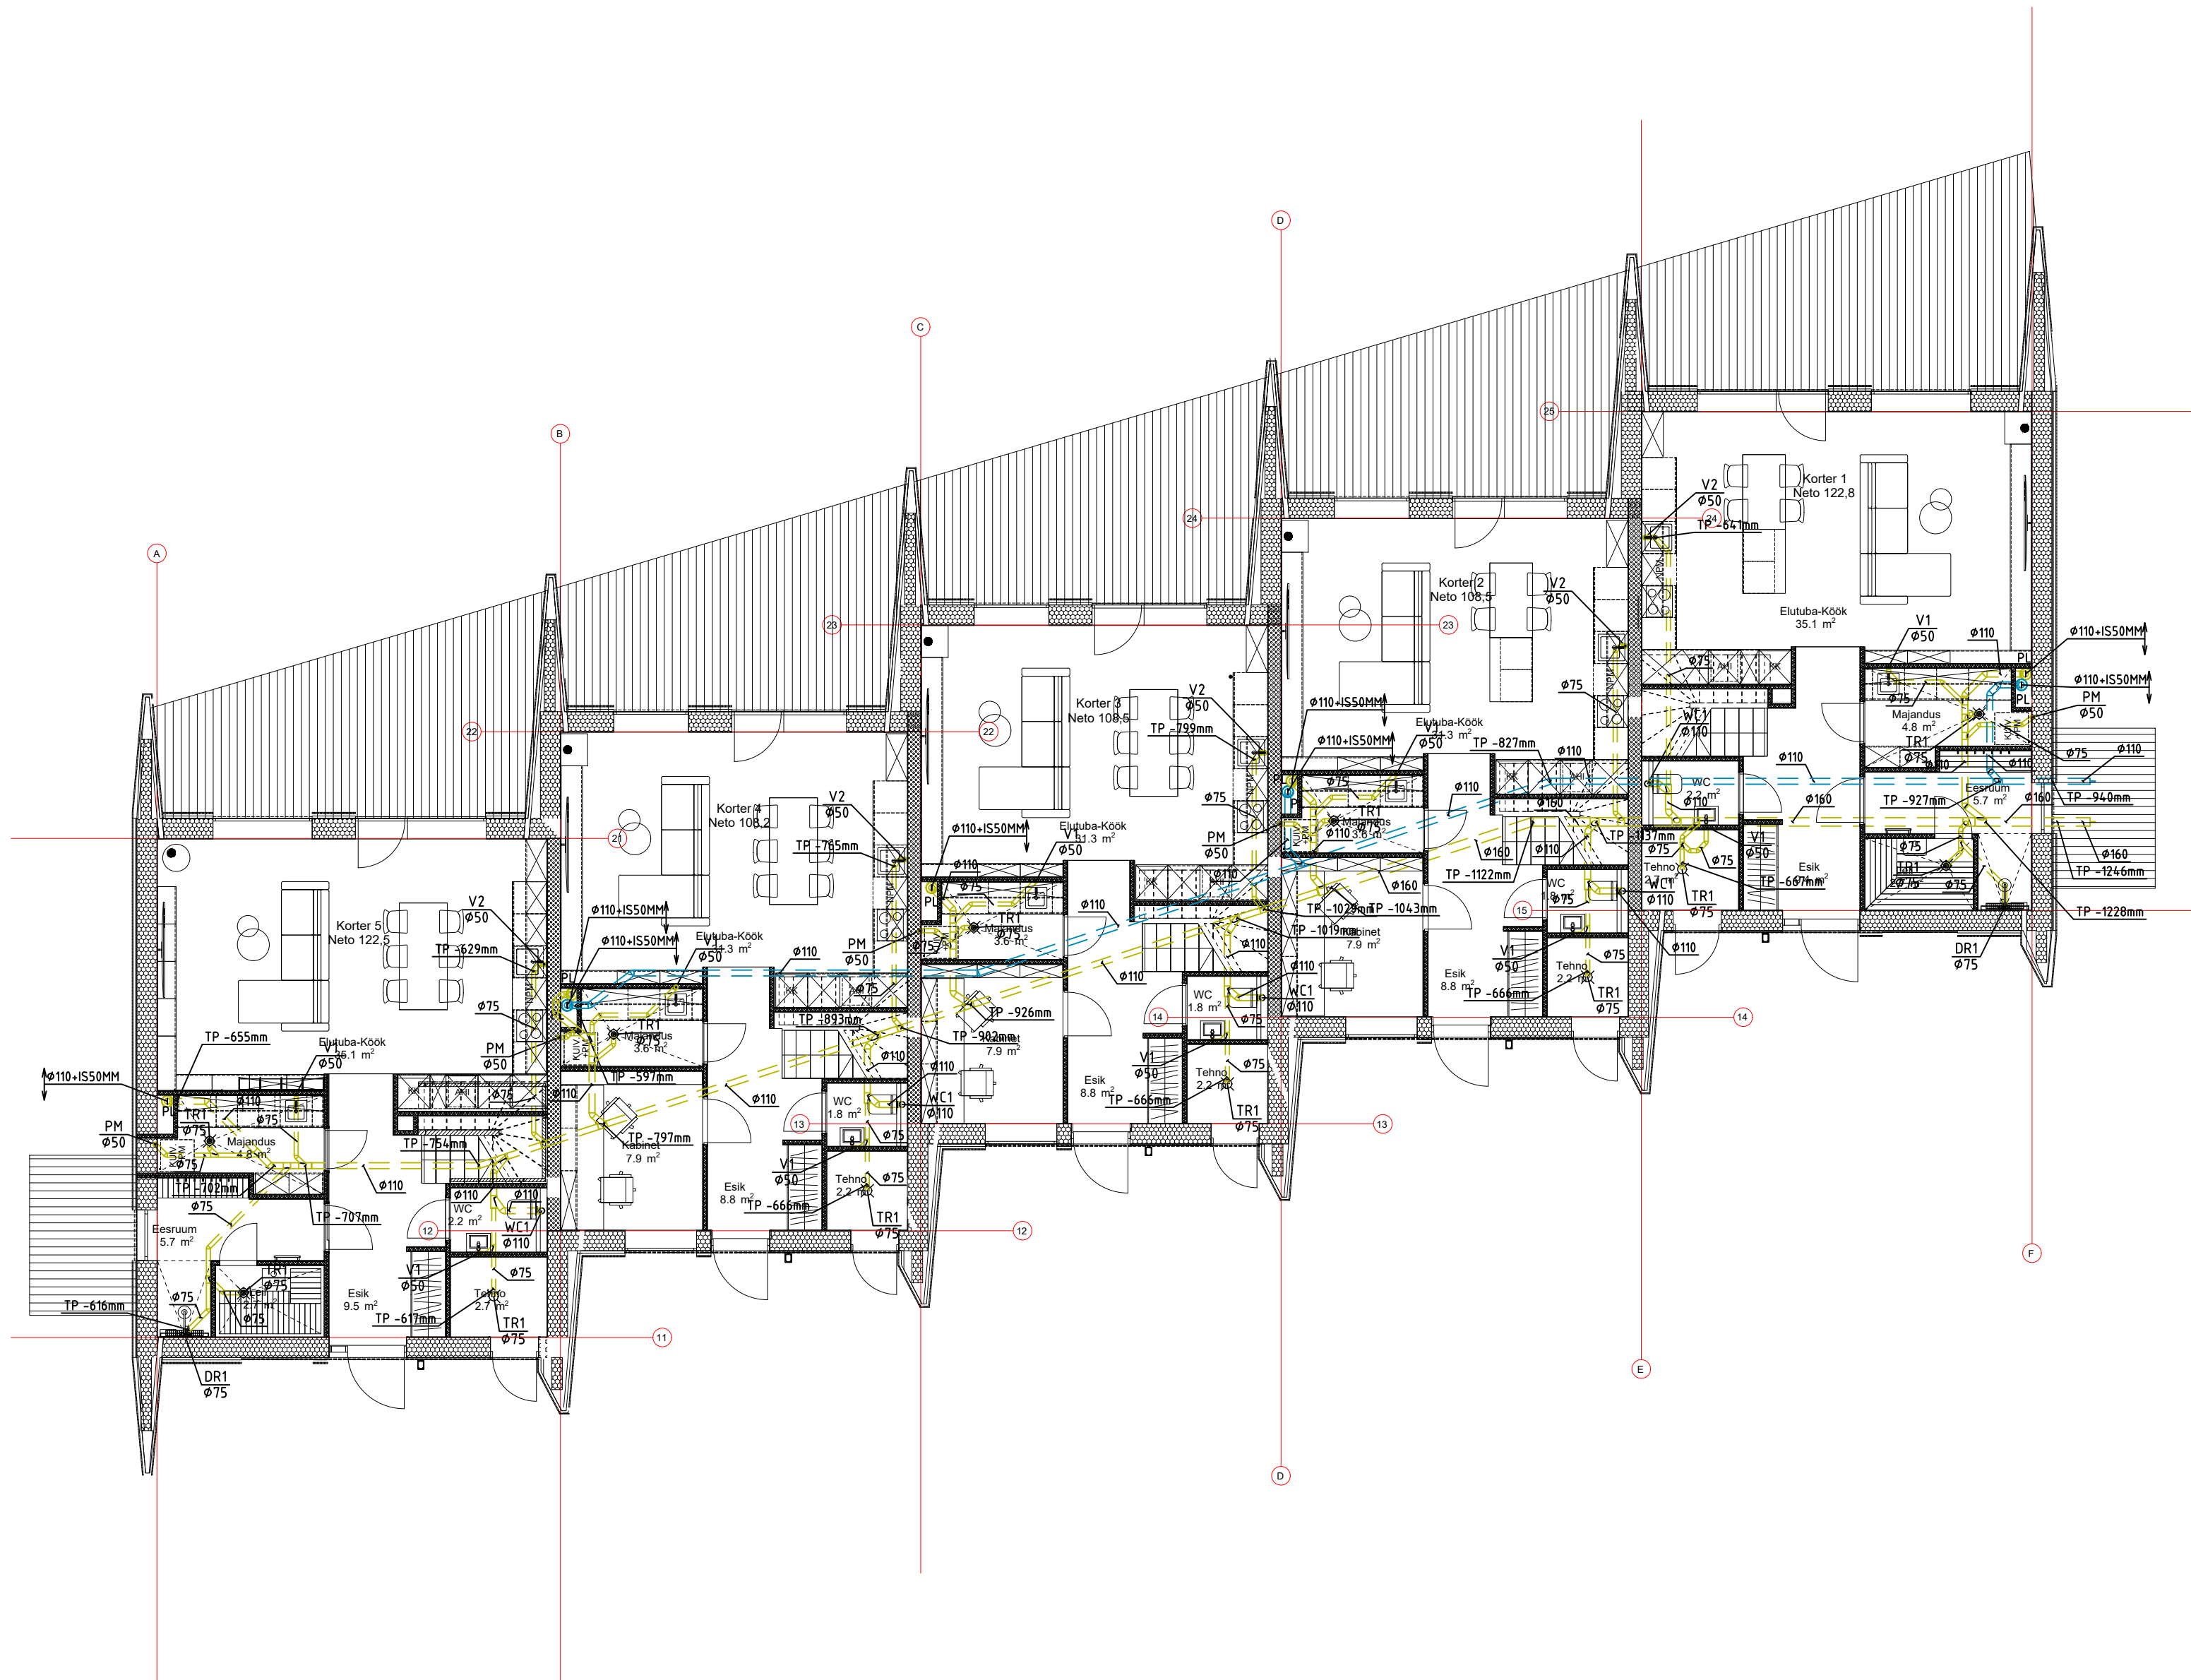

- TINGMÄRGID
- REOVEEKANALISATSIIOONI TORUSTIK PÕRANDAS (K1)
  - SADEMEVEEKANALISATSIIOONI TORUSTIK PÕRANDAS (K2)
  - REOVEEKANALISATSIIOONI TORUSTIK LAE ALL (K1)
  - SADEMEVEEKANALISATSIIOONI TORUSTIK LAE ALL (K2)
- TR1 TRAPP R/V TERASEST RESTIGA  
DR1 DUSHIRENN R/V TERASEST RESTIGA  
V1 VALAMU  
V2 KÖÖGIVALAMU  
WC1 WC-POTT  
PM PESUMASIN  
TP TORU PÕHJA KÕRGUSMÄRK  
PL PUHATUSLUUK, +1.0m PÕRANDA PINNAST

- MÄRKUSED
- HOONE SISENE REOVEE KANALISATSIIOONITORUSTIK MONTEERIDA PLASTIST (PP/PVC) KANALISATSIIOONITORUDEST Ø32-Ø160.
  - KÕIK KANALISATSIIOONIPÜSTIKUD JA LAELUSED TORUSTIKUD ISOLEERIDA 50MM PAKSUSE ALFOOLIUMKATTEGA KIVIVILLAST TORUISOLATSIOONI KOORIKUTEGA (TIHEDUS ≤100 KG/M3), KUI EI OLE JOONISEL NÄIDATUD TEISITI. TORUISOLATSIOONI SÜTTIMISTUNDLIKUS-TULELEVIMISKLASS ON B-S1, D0.
  - KANALISATSIIOONIPÜSTIKUD LÕPETADA KATUSEL UV-KINDLA TUULUTUSOTSIKUTEGA, UV-KINDLATE TUULUTUSOTSIKUTE MINIMAALNE PAIGALDUSKÕRGUS +0,7 M KATUSEPINNAST.
  - KANALISATSIIOONIPÜSTIKUTE KÕIGE ALUMISELE KORRUSELE TULEB PAIGALDADA PUHASTUSLUUGID 1,0M KÕRGUSELE PÕRANDAST JA PUHASTUSLUUKIDE HOOLDUSLUUGID PEAVAD VASTAMA KONSTRUKTSIOONI TULEKAITSEASTMELE.
  - KÕIK PLASTTORUDE LÄBIVIIGUD TULETÕKKE TARINDIDEST VARUSTADA TULETÕKKEMANSETTIDEGA, TULETÕKKEMÄHISTEGA VÕI TORUDELE KUINI Ø50 MM SPESTIAALSE PAISUVA TULETÕKKESILUKOONIGA.
  - TORUSTIKU LÄBIVIIGUDE TEGEMISEL TULEB JÄLGIDA KONSTRUKTIIVSE JA ARHITEKTUURSE OSA JOONISEID. TORUSTIKE LÄBIVIIGUD VUNDAMENTIDEST JA VUNDAMENTIDE ALT TEHA HÜLSIS ÜKS MÕOT TORUST SUUREM.
  - KÖÖGIVALAMU KÕRVAL PAKNEVAD NÕUDEPESUMASINAD KANALISEERIDA LÄBI KÖÖGIVALAMU SIFOONI.
  - TORUSTIKE PAIGALDAMISEL ARVESTADA TEISTE ERIOSADEGA.

|   |                                                                                 |                             |   |
|---|---------------------------------------------------------------------------------|-----------------------------|---|
| Tähis   | Muudatus                                                                        | Teostaja                    | Kuupäev   |
| TÖÖ NIMETUS   | RIDAELAMU                                                                       | TELLUA                      | SAKU ARENDUS OÜ   |
| ADRESS   | KOMEEDI TN 2, SAKU, SAKU VALD, HARJUMAA                                         | JOONIS                      | KANALISATSIIOON. 1-KORRUS                                                                                           |
| Smart Pipes OÜ<br>Registrikood 11975398<br>tel +372 628 8802<br>info@smartpipes.ee<br>Majaka tn 44-9, Tallinn, Harjumaa, 11412<br>MTR EEP001986, EPE000622 | VASTUTAV SPETSIALIST<br>V.LOORENTS<br>PROJEKTEERIJAL<br>V.LOORENTS<br>OSA<br>VK | KLUPÄEV<br>PP<br>16.03.2025 | FAILI NIMI<br>24060_VK_1-korrus.dwg<br>TÖÖ NR<br>24060-3<br>MÕÖTKAVA<br>1:100<br>JOONISE NR<br>VK-3<br>JOONISTE ARV |