


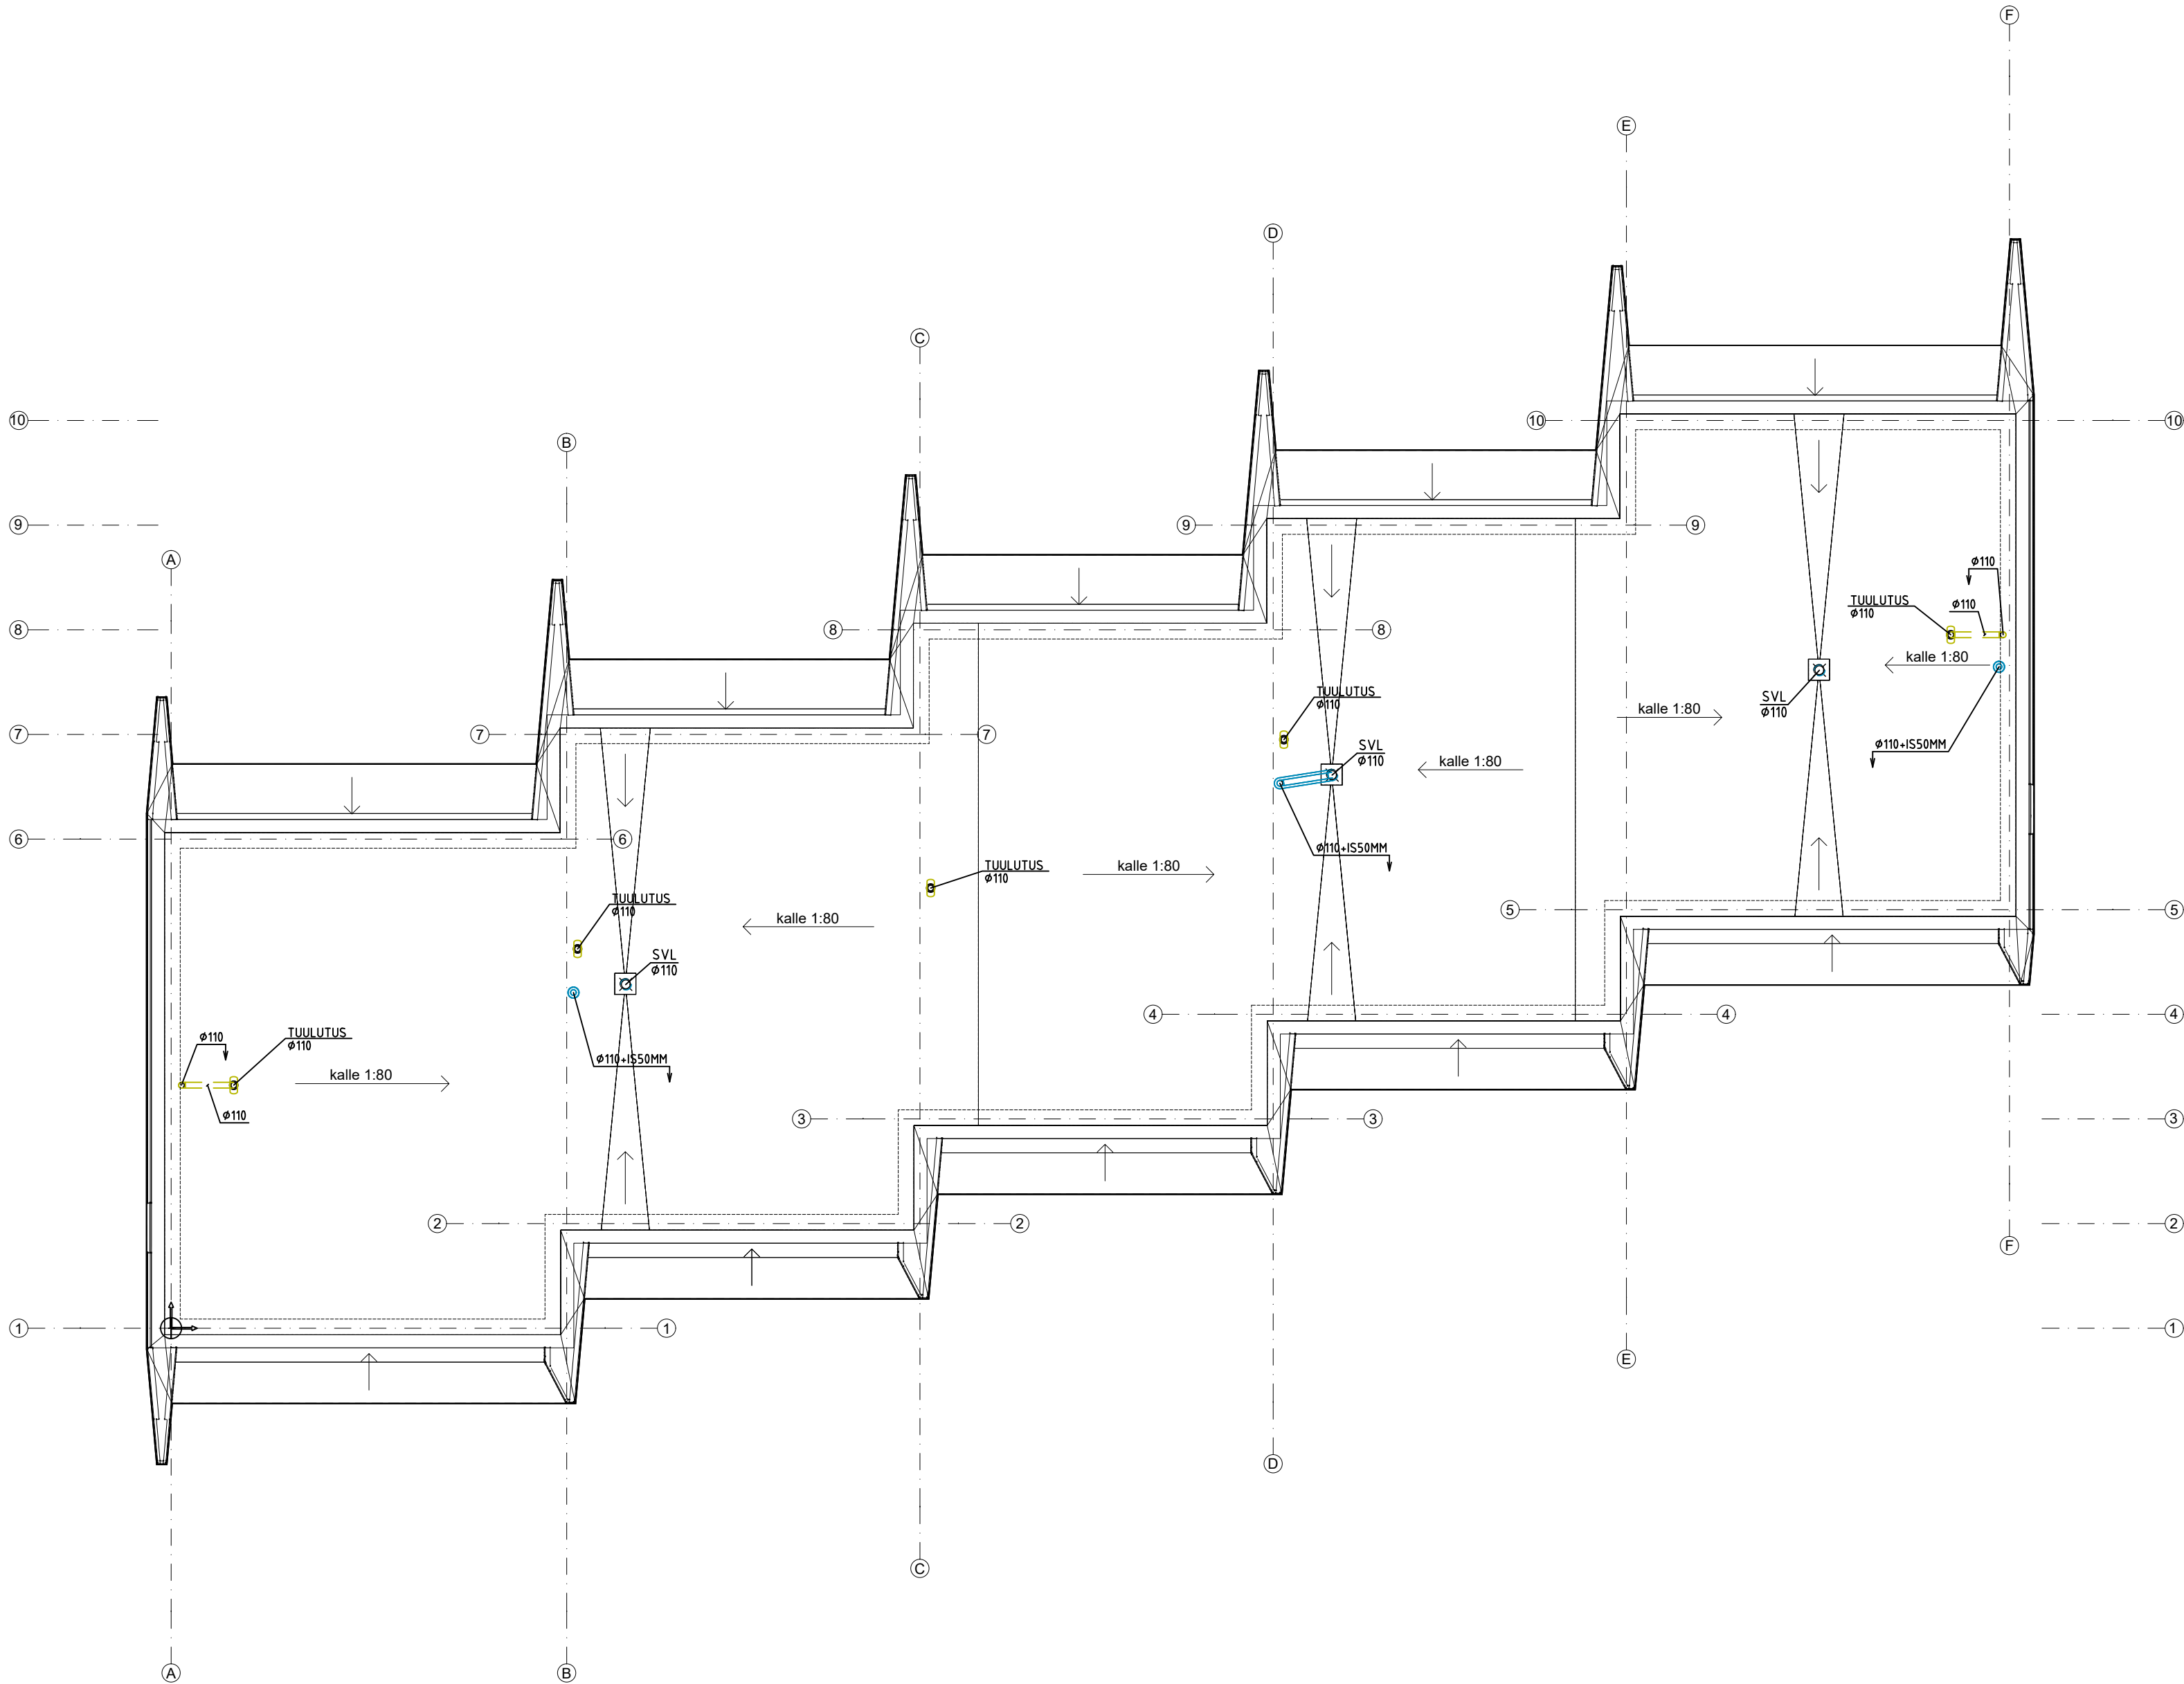

TINGMÄRGID
SVL EL.KÜTTEKAABLAGI SADEMEVEELEHTER

- MÄRKUSED
- HOONE SISENE REOVEE KANALISATSIOONITORUSTIK MONTEERIDA PLASTIST (PP/PVC) KANALISATSIOONITORUDEST Ø32-Ø160.
 - KÕIK KANALISATSIOONIPÜSTIKUD JA LAEALUSED TORUSTIKUD ISOLEERIDA 50MM PAKSUSE AL.FOOLIUMKATTEGA KIVIVILLAST TORUISOLATSIOONI KOORIKUTEGA (TIHEDUS ≤100 KG/M3), KUI EI OLE JOONISEL NÄIDATUD TEISITI. TORUISOLATSIOONI SÜTTIMISTUNDLIKKUS-TULELEVIMISKLASS ON B-S1, D0.
 - KANALISATSIOONIPÜSTIKUD LÕPETADA KATUSEL UV-KINDLA TUULUTUSOTSIKUTEGA, UV-KINDLATE TUULUTUSOTSIKUTE MINIMAALNE PAIGALDUSKÕRGUS +0,7 M KATUSEPINNAST.
 - KANALISATSIOONIPÜSTIKUTE KÕIGE ALUMISELE KORRUSELE TULEB PAIGALDADA PUHASTUSLUUGID 1,0M KÕRGUSELE PÖRANDAST JA PUHASTUSLUUKIDE HOOLDUSLUUGID PEAVAD VASTAMA KONSTRUKTSIOONI TULEKAITSEASTMELE.
 - KÕIK PLASTTORUDE LÄBIVIIGUD TULETÕKKE TARINDIDEST VARUSTADA TULETÕKKEMANSETTIDEGA, TULETÕKKEMÄHISTEGA VÕI TORUDELE KUNI Ø50 MM SPETIAALSE PAISUVA TULETÕKKESILUKOONIGA.
 - TORUSTIKU LÄBIVIIGUDE TEGEMISEL TULEB JÄLGIDA KONSTRUKTIIVSE JA ARHITEKTUURSE OSA JOONISEID. TORUSTIKE LÄBIVIIGUD VUNDAMENTIDEST JA VUNDAMENTIDE ALT TEHA HÜLSIS (ÜKS MÕÖT TORUST SUUREM).
 - KÕÕGIVALAMU KÕRVAL PAKNEVAD NÕUDEPESUMASINAD KANALISEERIDA LÄBI KÕÕGIVALAMU SIFOONI.
 - TORUSTIKE PAIGALDMISEL ARVESTADA TEISTE ERIOSADEGA.

01	Muutunud katuse läbiviikude asukohad	V.Loorents	08.05.2025
Tähis	Muudatus	Teostaja	Kuupäev
TÖÖ NIMETUS RIDAEELAMU		TELLUA SAKU ARENDUS OÜ	
Aadress KOMEEDI TN 1, SAKU, SAKU VALD, HARJUMAA		JOONIS KANALISATSIOON. KATUS	
Smart Pipes OÜ Registrikood 11975398 tel +372 628 8802 info@smartpipes.ee Majaka tn 44-9, Tallinn, Harjumaa, 11412 MTR EEP001966, EPE000622		VASTUTAV SPETSIALIST V.LOORENTS PROJEKTEERIJAL V.LOORENTS OSA VK	STADIUM PP KUIUPÄEV 16.03.2025
FAILI NIMI 24060_VK_katus.dwg		TÖÖ NR 24060-2	MOOTKAVA 1:100
JOONISE NR VK-5		JOONISTE ARV	