



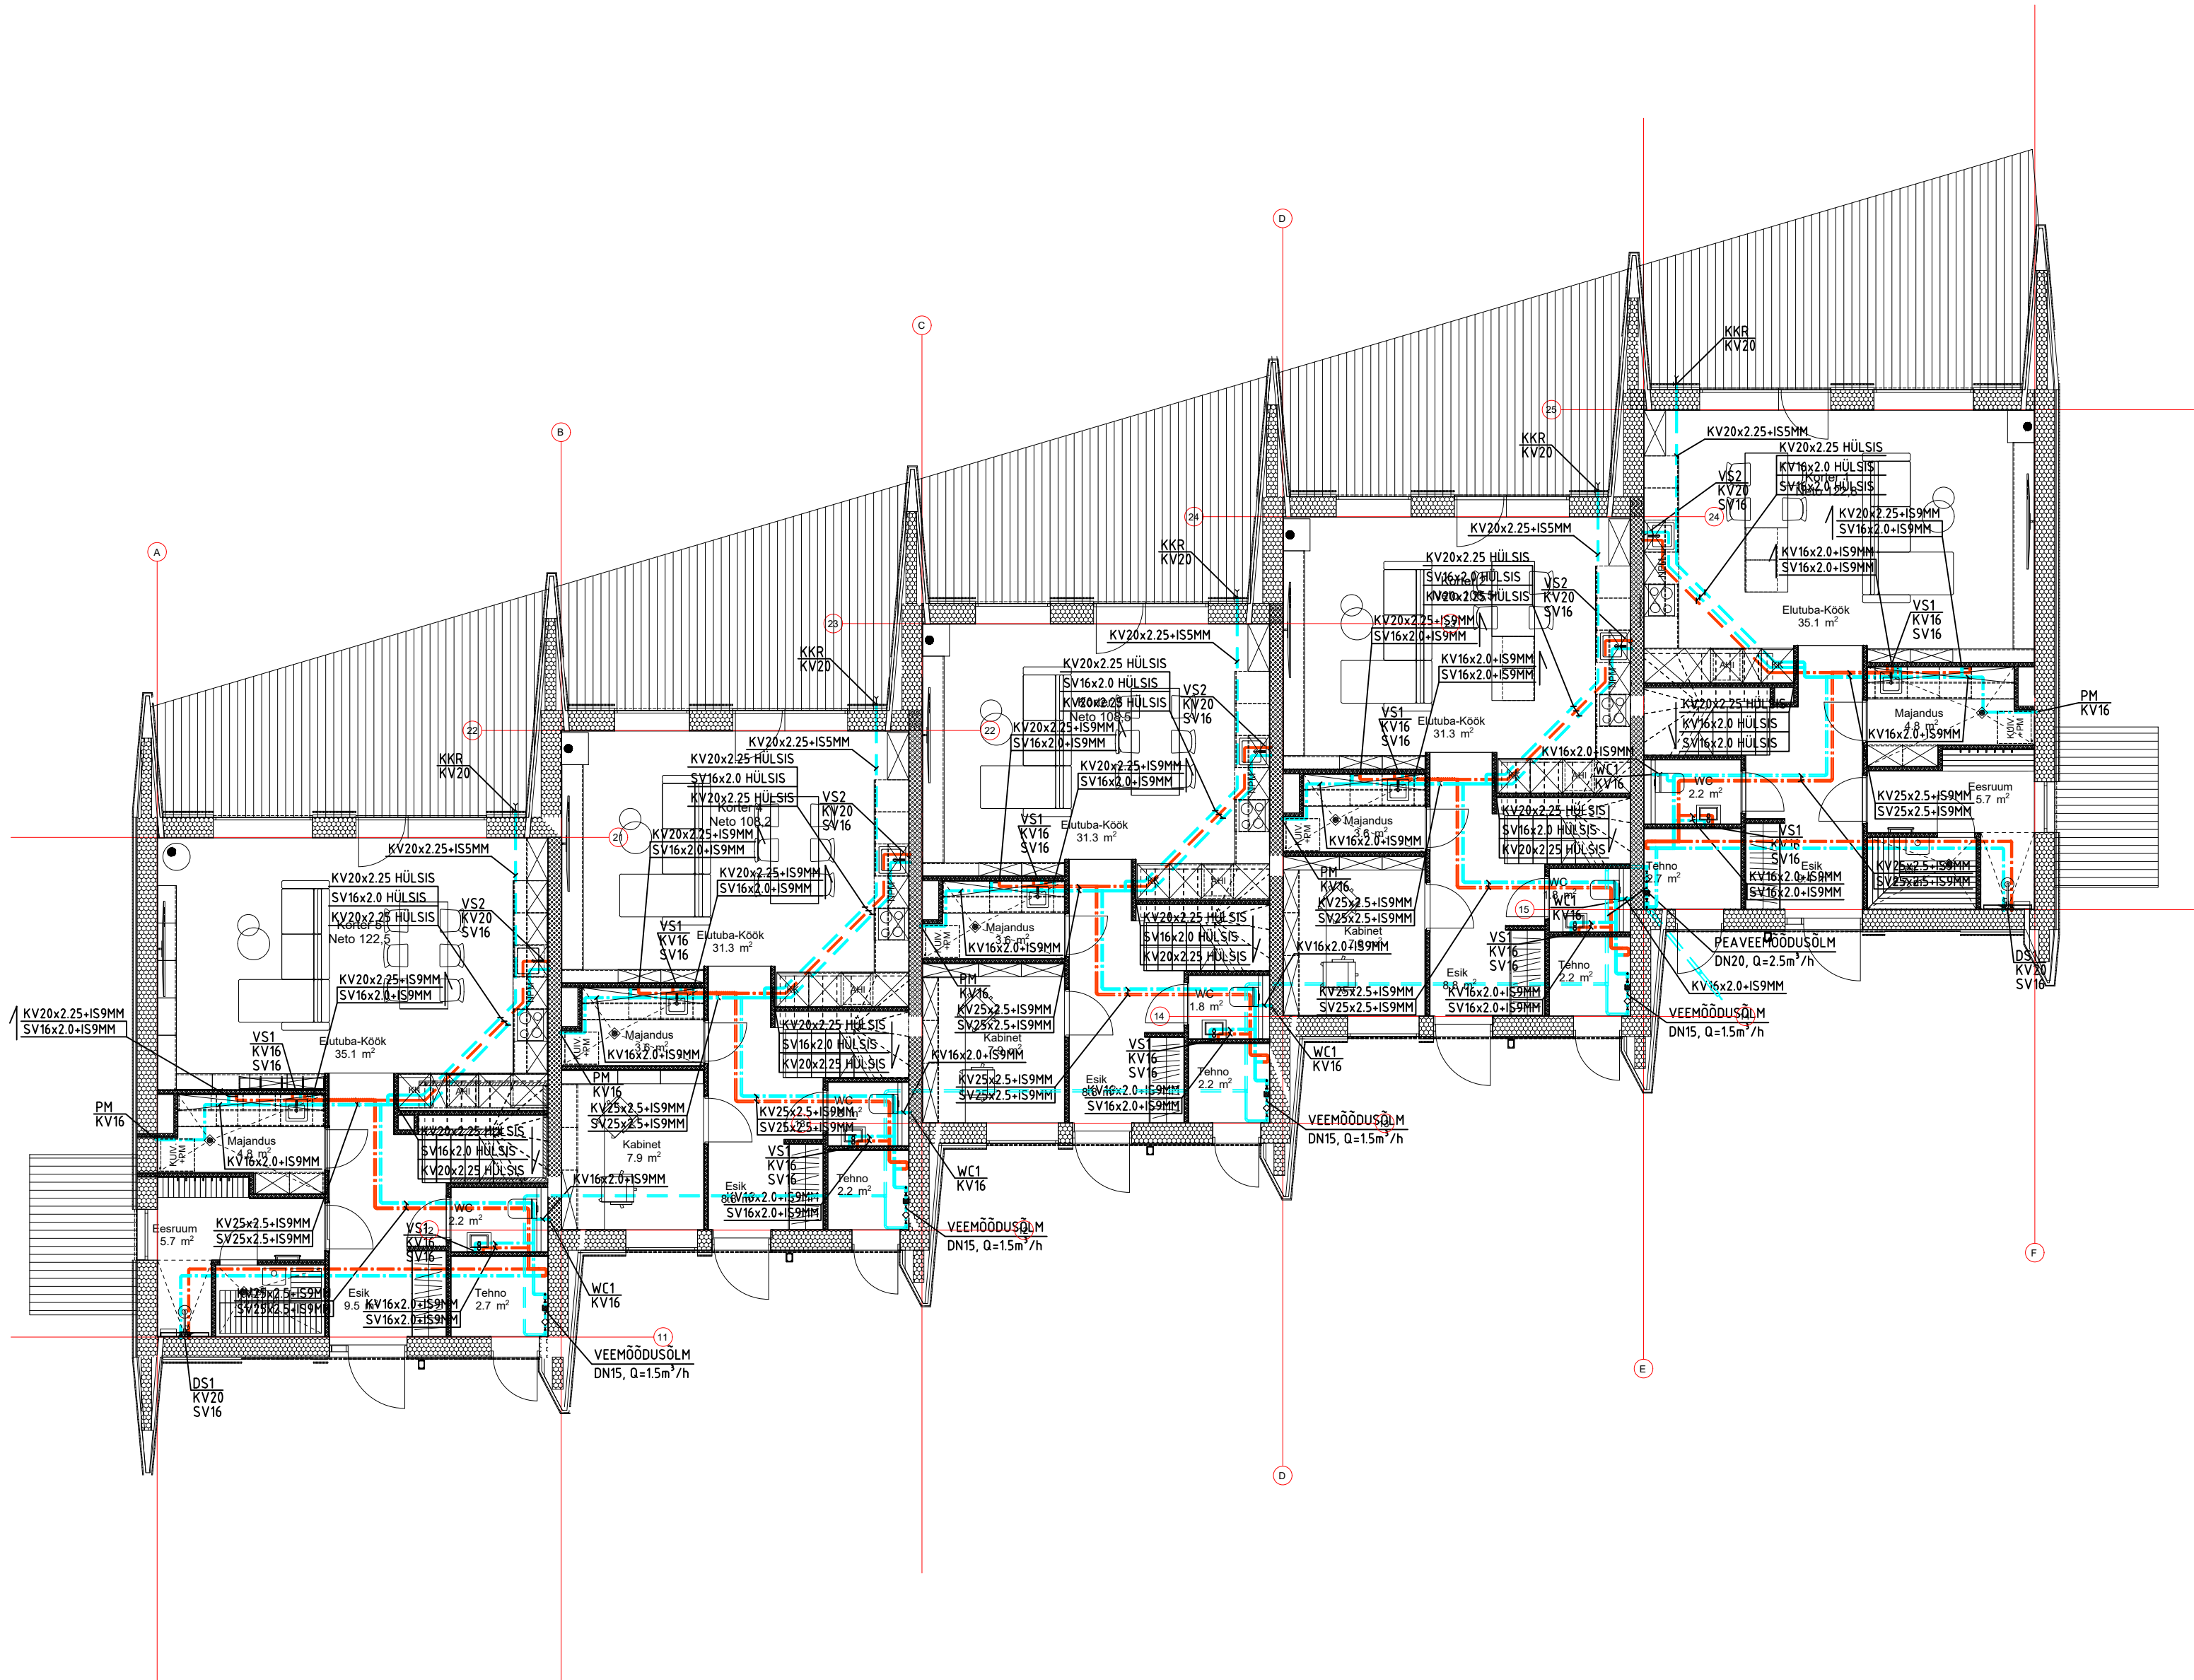

| TABEL 1. TORUDE KINNITUSKAUGUSED (+20°C) |                     |           |             |           |                         |           |
|------------------------------------------|---------------------|-----------|-------------|-----------|-------------------------|-----------|
| PLASTTORUD<br>de, mm                     | PVC, PEH, PEM<br>mm |           | PEX<br>mm   |           | Komposiittoru<br>de, mm |           |
|                                          | HORISONTAAL         | VERTIKAAL | HORISONTAAL | VERTIKAAL | HORISONTAAL             | VERTIKAAL |
| 20                                       | 700                 | 700       | 300         | 300       | 1200                    | 1500      |
| 25                                       | 700                 | 800       | 300         | 300       | 1300                    | 1700      |
| 32                                       | 900                 | 1000      | 400         | 400       | 1300                    | 2000      |
| 40                                       | 1000                | 1300      | 400         | 400       | 1400                    | 2100      |
| 50                                       | 1100                | 1600      | 500         | 500       | 1400                    | 2200      |
| 63                                       | 1200                | 2000      | 500         | 500       | 1500                    | 2600      |
| 75                                       | 1500                | 2000      | 600         | 600       | 1500                    | 2850      |

- MÄRKUSED
- PROJEKTEERITUD MAJANDUS-JOOGIVEESÜSTEEMI VEETORUD MONTEERIDA NT. VEEVARUSTUSE KIHITSEIN-PLASTTORUDEST.
  - PROJEKTEERITUD VEETORUSTIKUNA KASUTADA EELISOLEERITUD TORUSTIKU.
  - VEEVÕTUSEADMETE ÜHENDUSED TEHA TORUGA Ø16x2.0 (DUŠSIDE KÜLMAVEE ÜHENDUSED TORUGA Ø20x2.5)
  - VEETORUSTIKUD PAIGALDADA RIPPLAE PEALE, KUI JOONISEL EI OLE TEISITI NÄIDATUD.
  - ÜHENDUSTORUSTIKUD SANITAARSEADMETEGA PAIGALDADA SÜVISTATULT HÜLSIS PÕRANDA VÕI SEINAKONSTRUKTSIOONI SISSE.
  - PLASTTORUDE LÄBIVIIGUD TULETÖKKETARINDIST VARUSTADA TULETÖKKEMANSETTIDEGA, TULETÖKKEMÄHISTEGA VÕI TORUD KUNI Ø50 mm SPETSIAALSE TULETÖKKE SILIKOONIGA.
  - TORUSTIKU LÄBIVIIGUDE TEGEMISEL TULEB JÄLGIDA KONSTRUKTIIVSE JA ARHITEKTUURSE OSA JOONISEID.
  - TORUSTIKE PAIGALDAMISEL ARVESTADA TEISTE ERIOSEADEGA.
  - KÕÕGIVALAMU KÕRVAL PAIKNEVA NÕUDEPESUMASINA VEEÜHENDUS TEOSTADA KÕÕGIVALAMU KRAANIPÕLVEST.
  - PRESSITUD LIITMIKEGA TORUSTIKE PUHUL KASUTADA LEKKETUVASTUSSÜSTEEMIGA LIITMIKKE (LEAK BEFORE PRESS FUNCTION), MIS TUVASTAVAD LEKKE, KUI LIITMIK POLE PRESSITUD.

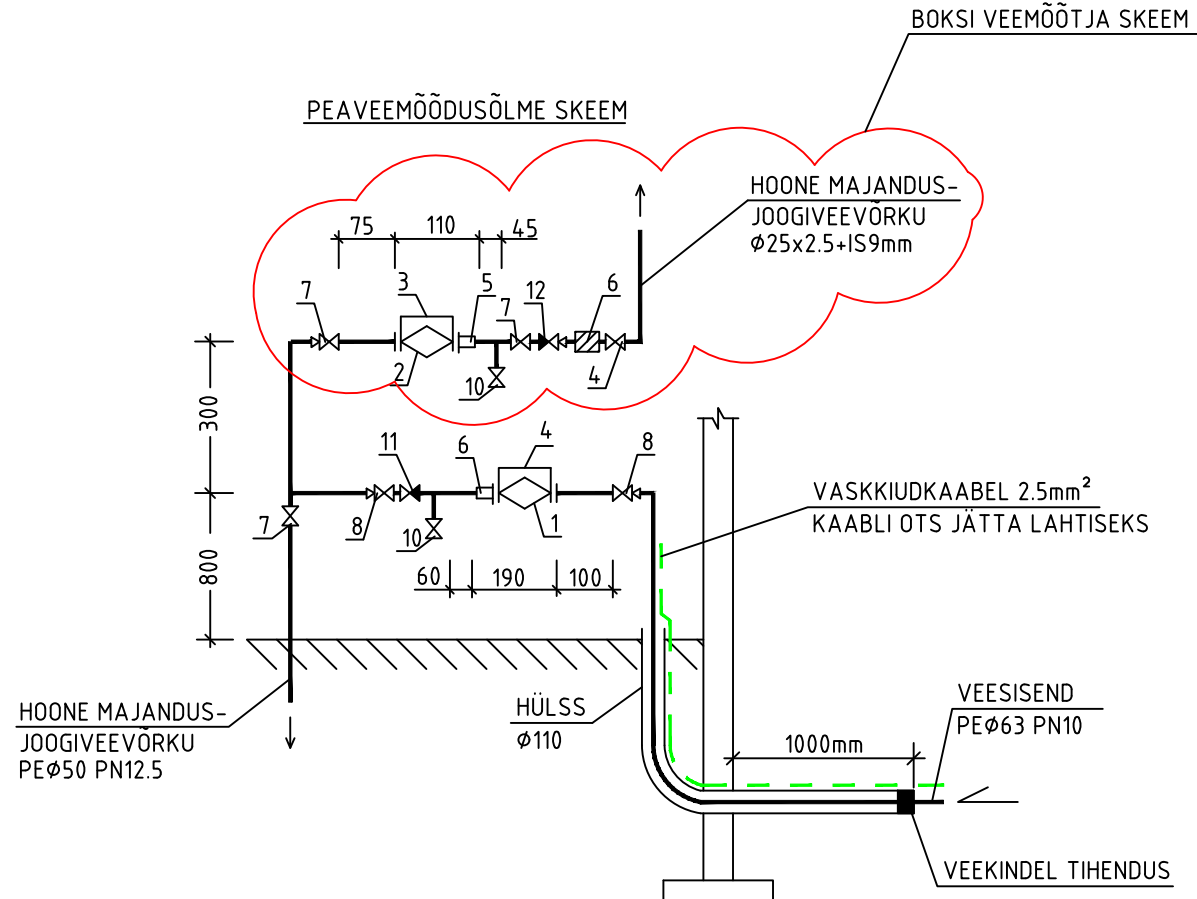

- MÄRKUS
- KAUGLOETAV VEEARVESTI DN20, (Q=2.5m³/h)
  - VEEARVESTI DN15, (Q=1.5m³/h)
  - VEEARVESTI DN15 KONSOOL, L=110mm (maandada)
  - VEEARVESTI DN20 KONSOOL, L=190mm (maandada)
  - LIIGUTATAVA HÜLSIGA LIIDES DN15
  - LIIGUTATAVA HÜLSIGA LIIDES DN20
  - KUULVENTIIL DN15
  - KUULVENTIIL DN20
  - TAGASIPESUGA MEHAANILINE FILTER DN20
  - TÜHJENDUSKRAAN DN15
  - TAGASILOOGIKLAPP DN20
  - TAGASILOOGIKLAPP DN15

#### TINGMÄRGID

- PROJEKTEERITUD KÜLMAVEE TORUSTIK PÕRANDAS (KV)
- PROJEKTEERITUD SOOJAVEE TORUSTIK PÕRANDAS (SV)
- PROJEKTEERITUD KÜLMAVEE TORUSTIK LAE ALL (KV)
- PROJEKTEERITUD SOOJAVEE TORUSTIK LAE ALL (SV)
- VS1 - VALAMU SEGISTI
- VS2 - KÕÕGIVALAMU SEGISTI
- DS1 - DUSHISEGISTI
- WC1 - WC-POTI ÜHENDUS
- PM - PESUMASIN
- KK - KÜLMKRAAN

|                                                    |          |          |         |
|----------------------------------------------------|----------|----------|---------|
| Tähis                                              | Muudatus | Teostaja | Kuupäev |
| TOO NIMETUS<br>RIDAEALAMU                          |          |          |         |
| ADDRESS<br>KOMEEDI TN 2, SAKU, SAKU VALD, HARJUMAA |          |          |         |
| TOO NR<br>24060                                    |          |          |         |
| MÕÕTKAVA<br>1:100                                  |          |          |         |
| JOONIS<br>VEEVARUSTUS. 1-KORRUS                    |          |          |         |
| FAILI NIMI<br>24060_VK_1-korrus.dwg                |          |          |         |
| JOONISTE ARV<br>VK-1                               |          |          |         |