


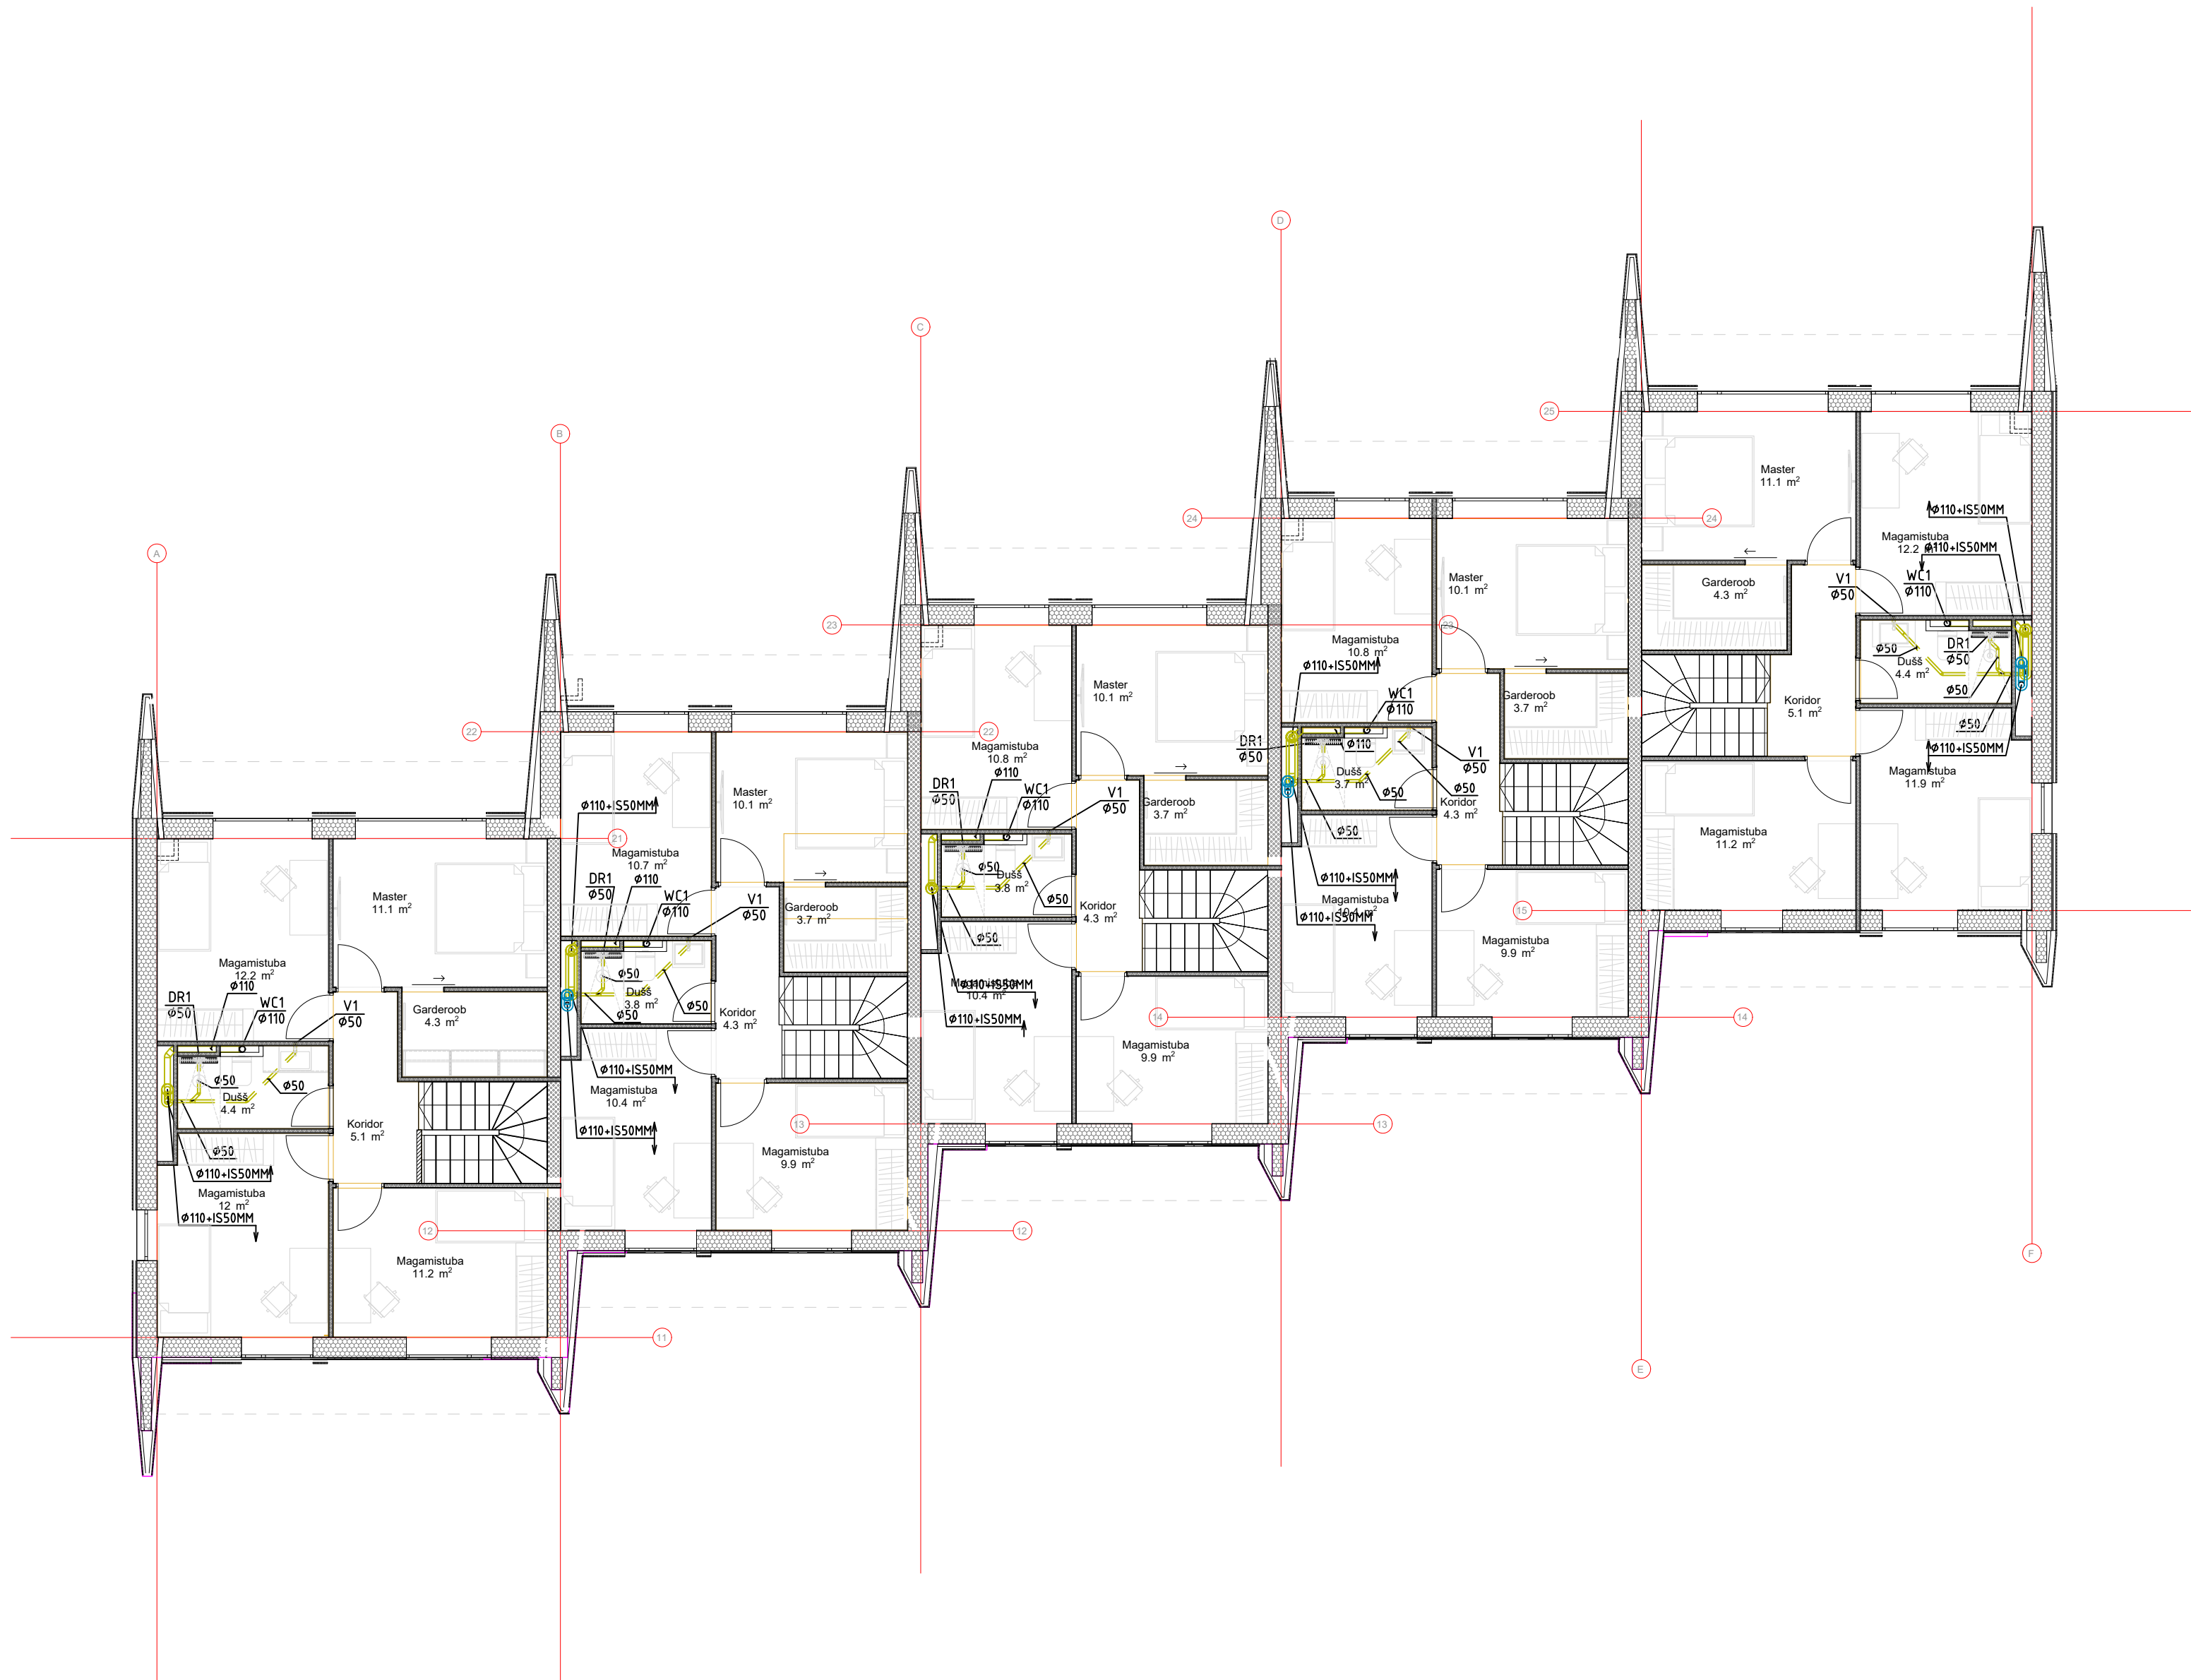

- TINGMÄRGID
- REOVEEKANALISATSIiooni TORUSTIK PÕRANDAS (K1)
 - SADEMEVEEKANALISATSIiooni TORUSTIK PÕRANDAS (K2)
 - REOVEEKANALISATSIiooni TORUSTIK LAE ALL (K1)
 - SADEMEVEEKANALISATSIiooni TORUSTIK LAE ALL (K2)
 - DR1 DUSHIRENN R/V TERASEST RESTIGÄ
 - V1 VALAMU
 - WC1 WC-POTT

- MÄRKUSED
- HOONE SISENE REOVEE KANALISATSIOONITORUSTIK MONTEERIDA PLASTIST (PP/PVC) KANALISATSIOONITORUDEST Ø32-Ø160.
 - KÕIK KANALISATSIOONIPÜSTIKUD JA LAELASED TORUSTIKUD ISOLEERIDA 50MM PAKSUSE ALFOOLIUMKATTEGA KIVIVILLAST TORUISOLATSIOONI KOORIKUTEGA (TIHEDUS ≤100 KG/M3), KUI EI OLE JOONISEL NÄIDATUD TEISITI. TORUISOLATSIOONI SÜTTIMISTUNDLIKUS-TULELEVIMISKLASS ON B-S1, D0.
 - KANALISATSIOONIPÜSTIKUD LÕPETADA KATUSEL UV-KINDLA TUULUTUSOTSIKUTEGA, UV-KINDLATE TUULUTUSOTSIKUTE MINIMAALNE PAIGALDUSKÕRGUS +0,7 M KATUSEPINNAST.
 - KANALISATSIOONIPÜSTIKUTE KÕIGE ALUMISELE KORRUSELE TULEB PAIGALDADA PUHASTUSLUUGID 1,0M KÕRGUSELE PÕRANDAST JA PUHASTUSLUUKIDE HOOLDUSLUUGID PEAVAD VASTAMA KONSTRUKTSIOONI TULEKAITSEASTMELE.
 - KÕIK PLASTTORUDE LÄBIVIIGUD TULETÕKKE TARINDIDEST VARUSTADA TULETÕKKEMANSETTIDEGA, TULETÕKKEMÄHISTEGA VÕI TORUDELE KUNI Ø50 MM SPETIAALSE PAISUVA TULETÕKKESILUKOONIGA.
 - TORUSTIKU LÄBIVIIGUDE TEGEMISEL TULEB JÄLGIDA KONSTRUKTIIVSE JA ARHITEKTUURSE OSA JOONISEID. TORUSTIKE LÄBIVIIGUD VUNDAMENTIDEST JA VUNDAMENTIDE ALT TEHA HÜLSIS (ÜKS MÕÖT TORUST SUUREM).
 - KÕOGIVALAMU KÕRVAL PAKNEVAD NÕUDEPESUMASINAD KANALISEERIDA LÄBI KÕOGIVALAMU SIFOONI.
 - TORUSTIKE PAIGALDAMISEL ARVESTADA TEISTE ERIOSADEGA.

01	Muutunud katuse läbiviikude asukohad	V.Loorents	08.05.2025
Tähis	Muudatus	Teostaja	Kuupäev
TÖÖ NIMETUS RIDAEELAMU		TELLUA SAKU ARENDUS OÜ	
Aadress KOMEEDI TN 2, SAKU, SAKU VALD, HARJUMAA		JOONIS KANALISATSIOON. 2-KORRUS	
Smart Pipes OÜ Registrikood 11975398 tel +372 628 8802 info@smartpipes.ee Majaka tn 44-9, Tallinn, Harjumaa, 11412 MTR EEP001966, EPE000622		VASTUTAV SPETSIALIST V.LOORENTS PROJEKTEERIJAL V.LOORENTS OSA VK	STADIUM PP KUIIPÄEV 16.03.2025
FAILI NIMI 24060_VK_2.korrus.dwg		TÖÖ NR 24060-3	MÕÖTKAVA 1:100
		JOONISE NR VK-4	JOONISTE ARV