
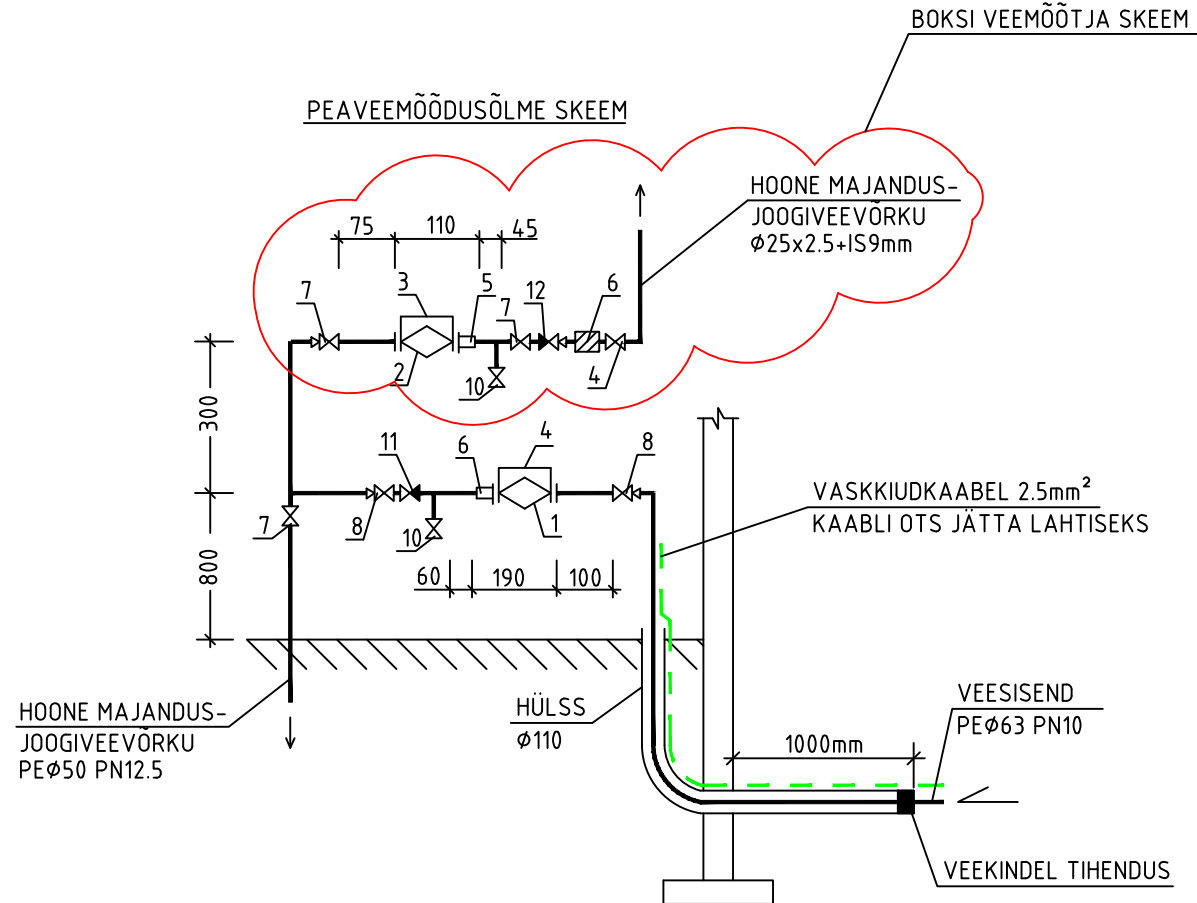


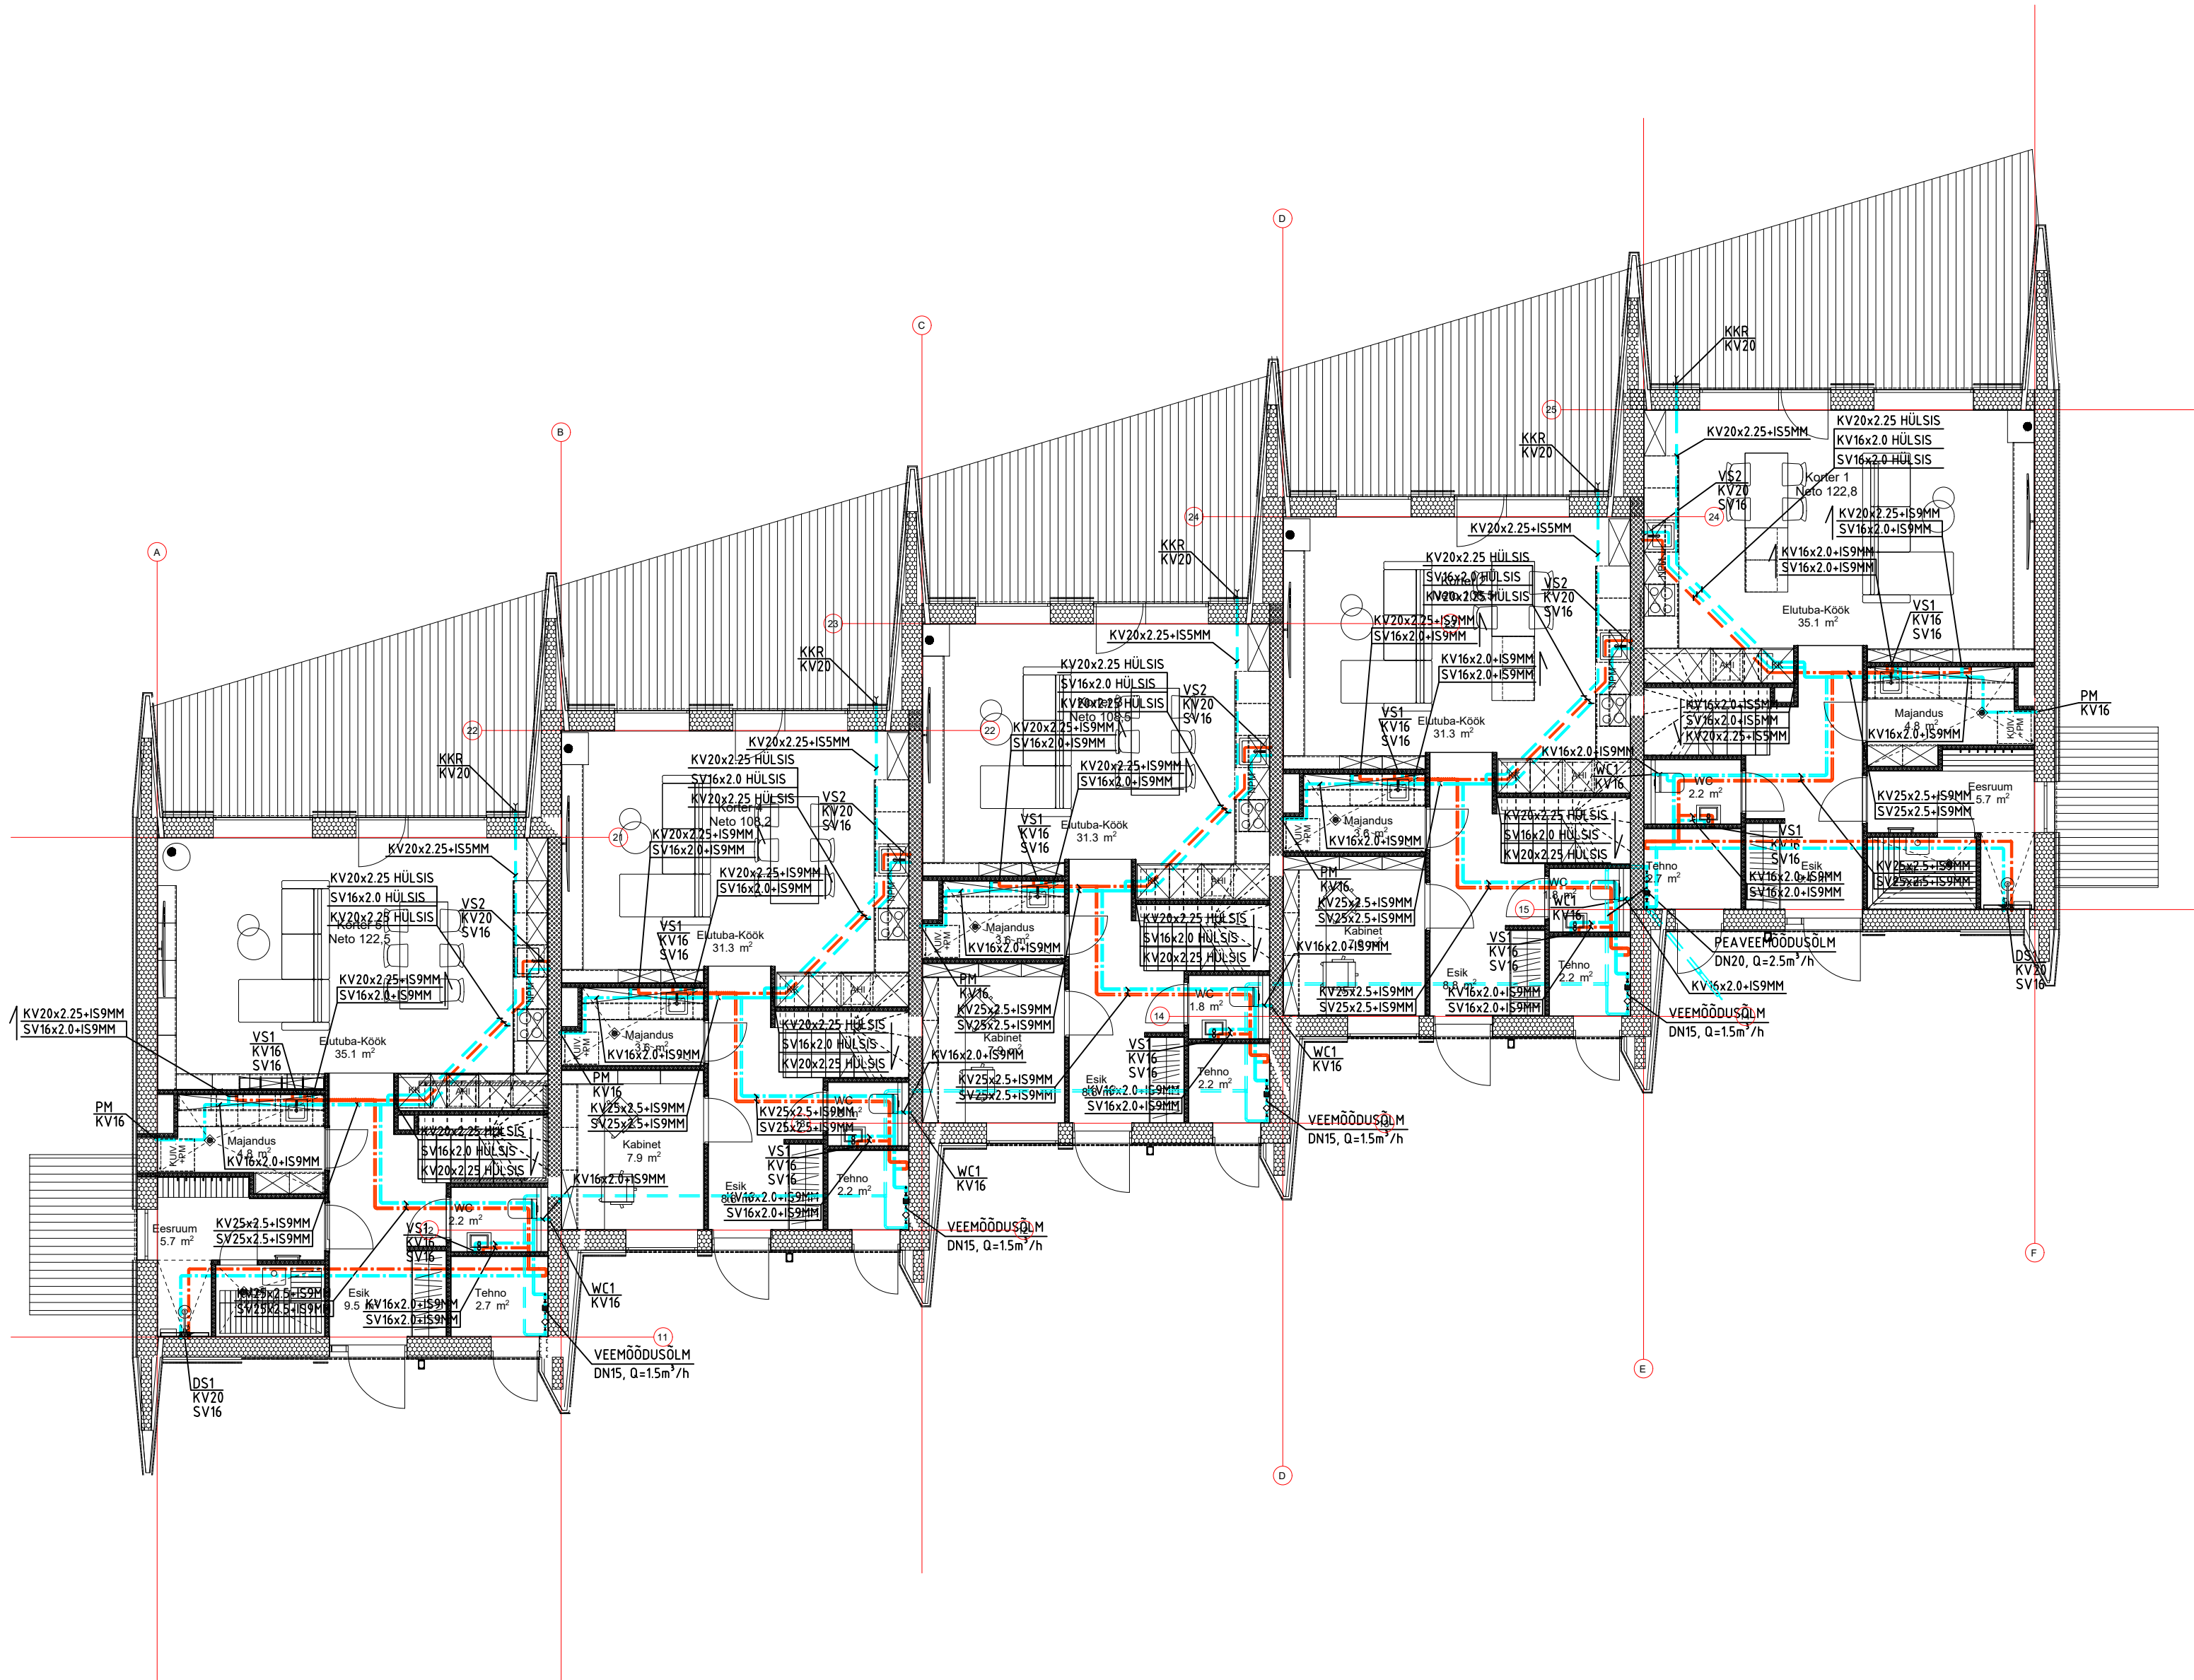

- MÄRKUS
1. KAUGLOETAV VEEARVESTI DN20, (Q=2.5m³/h)
 2. VEEARVESTI DN15, (Q=1.5m³/h)
 3. VEEARVESTI DN15 KONSOOL, L=110mm (maandada)
 4. VEEARVESTI DN20 KONSOOL, L=190mm (maandada)
 5. LIIGUTATAVA HÜLSIGA LIIDES DN15
 6. LIIGUTATAVA HÜLSIGA LIIDES DN20
 7. KUULVENTIIL DN15
 8. KUULVENTIIL DN20
 9. TAGASIPESUGA MEHAANILINE FILTER DN20
 10. TÜHJENDUSKRAAN DN15
 11. TAGASILOOGIKLAPP DN20
 12. TAGASILOOGIKLAPP DN15

TINGMÄRGID

- PROJEKTEERITUD KÜLMAVEE TORUSTIK PÕRANDAS (KV)
 - PROJEKTEERITUD SOOJAVEE TORUSTIK PÕRANDAS (SV)
 - PROJEKTEERITUD KÜLMAVEE TORUSTIK LAE ALL (KV)
 - PROJEKTEERITUD SOOJAVEE TORUSTIK LAE ALL (SV)
- VS1 - VALAMU SEGISTI
VS2 - KÖÖGIVALAMU SEGISTI
DS1 - DUSHISEGISTI
WC1 - WC-POTI ÜHENDUS
PM - PESUMASIN
KK - KÜLKRAN

MÄRKUSED

1. PROJEKTEERITUD MAJANDUS-JOOGIVEESÜSTEEMI VEETORUD MONTEERIDA NT. VEEVARUSTUSE KIHITSEIN-PLASTTORUDEST.
2. PROJEKTEERITUD VEETORUSTIKUNA KASUTADA EELISOLEERITUD TORUSTIKU.
3. VEEVÕTUSEADMETE ÜHENDUSED TEHA TORUGA Ø16x2.0 (DUŠSIDE KÜLMAVEE ÜHENDUSED TORUGA Ø20x2.25)
4. VEETORUSTIKUD PAIGALDADA RIPPLAE PEALE, KUI JOONISEL EI OLE TEISITI NÄIDATUD.
5. ÜHENDUSTORUSTIKUD SANITAARSEADMETEGA PAIGALDADA SÜVISTATULT HÜLSIS PÕRANDA VÕI SEINAKONSTRUKTSIOONI SISSE.
6. PLASTTORUDE LÄBIVIIGUD TULETÖKKETARINDIST VARUSTADA TULETÖKKEMANSETTIDEGA, TULETÖKKEMÄHISTEGA VÕI TORUD KUNI Ø50 mm SPETSIAALSE TULETÖKKE SILIKOONIGA.
7. TORUSTIKU LÄBIVIIGUDE TEGEMISEL TULEB JÄLGIDA KONSTRUKTIIVSE JA ARHITEKTUURSE OSA JOONISEID.
8. TORUSTIKE PAIGALDAMISEL ARVESTADA TEISTE ERIOSEDEGA.
9. KÖÖGIVALAMU KÕRVAL PAIKNEVA NÕUDEPESUMASINA VEEÜHENDUS TEOSTADA KÖÖGIVALAMU KRAANIPÕLVEST.
10. PRESSITUD LIITMIKEGA TORUSTIKE PUHUL KASUTADA LEKKETUVASTUSSÜSTEEMIGA LIITMIKKE (LEAK BEFORE PRESS FUNCTION), MIS TUVASTAVAD LEKKE, KUI LIITMIK POLE PRESSITUD.

TABEL 1. TORUDE KINNITUSKAUGUSED (+20°C)

PLASTTORUD de, mm	PVC, PEH, PEM mm		PEX mm		Komposiittoru de, mm	
	HORISONTAAL	VERTIKAAL	HORISONTAAL	VERTIKAAL	HORISONTAAL	VERTIKAAL
20	700	700	300	300	1200	1500
25	700	800	300	300	1300	1700
32	900	1000	400	400	1300	2000
40	1000	1300	400	400	1400	2100
50	1100	1600	500	500	1400	2200
63	1200	2000	500	500	1500	2600
75	1500	2000	600	600	1500	2850

Tähis	Muudatus	Teostaja	Kuupäev
TOO NIMETUS RIDAEELAMU			
ADDRESS KUJ TEE 16, SAKU, SAKU VALD, HARJUMAA			
TOO NR 24060_VK_1.korrus.dwg			
MÕÕTKAVA 1:100			
JOONISTE ARV VK-1			
VASTUTAV SPETSIALIST V.LOORENTS			
PROJEKTEERUA V.LOORENTS			
OSA VK			
STADIUM PP			
KUIPÄEV 16.03.2025			
TEOSTAJA SAKU ARENDUS OÜ			
KUIPÄEV 24060_VK_1.korrus.dwg			
MÕÕTKAVA 1:100			
JOONISTE ARV VK-1			
VASTUTAV SPETSIALIST V.LOORENTS			
PROJEKTEERUA V.LOORENTS			
OSA VK			
STADIUM PP			
KUIPÄEV 16.03.2025			