


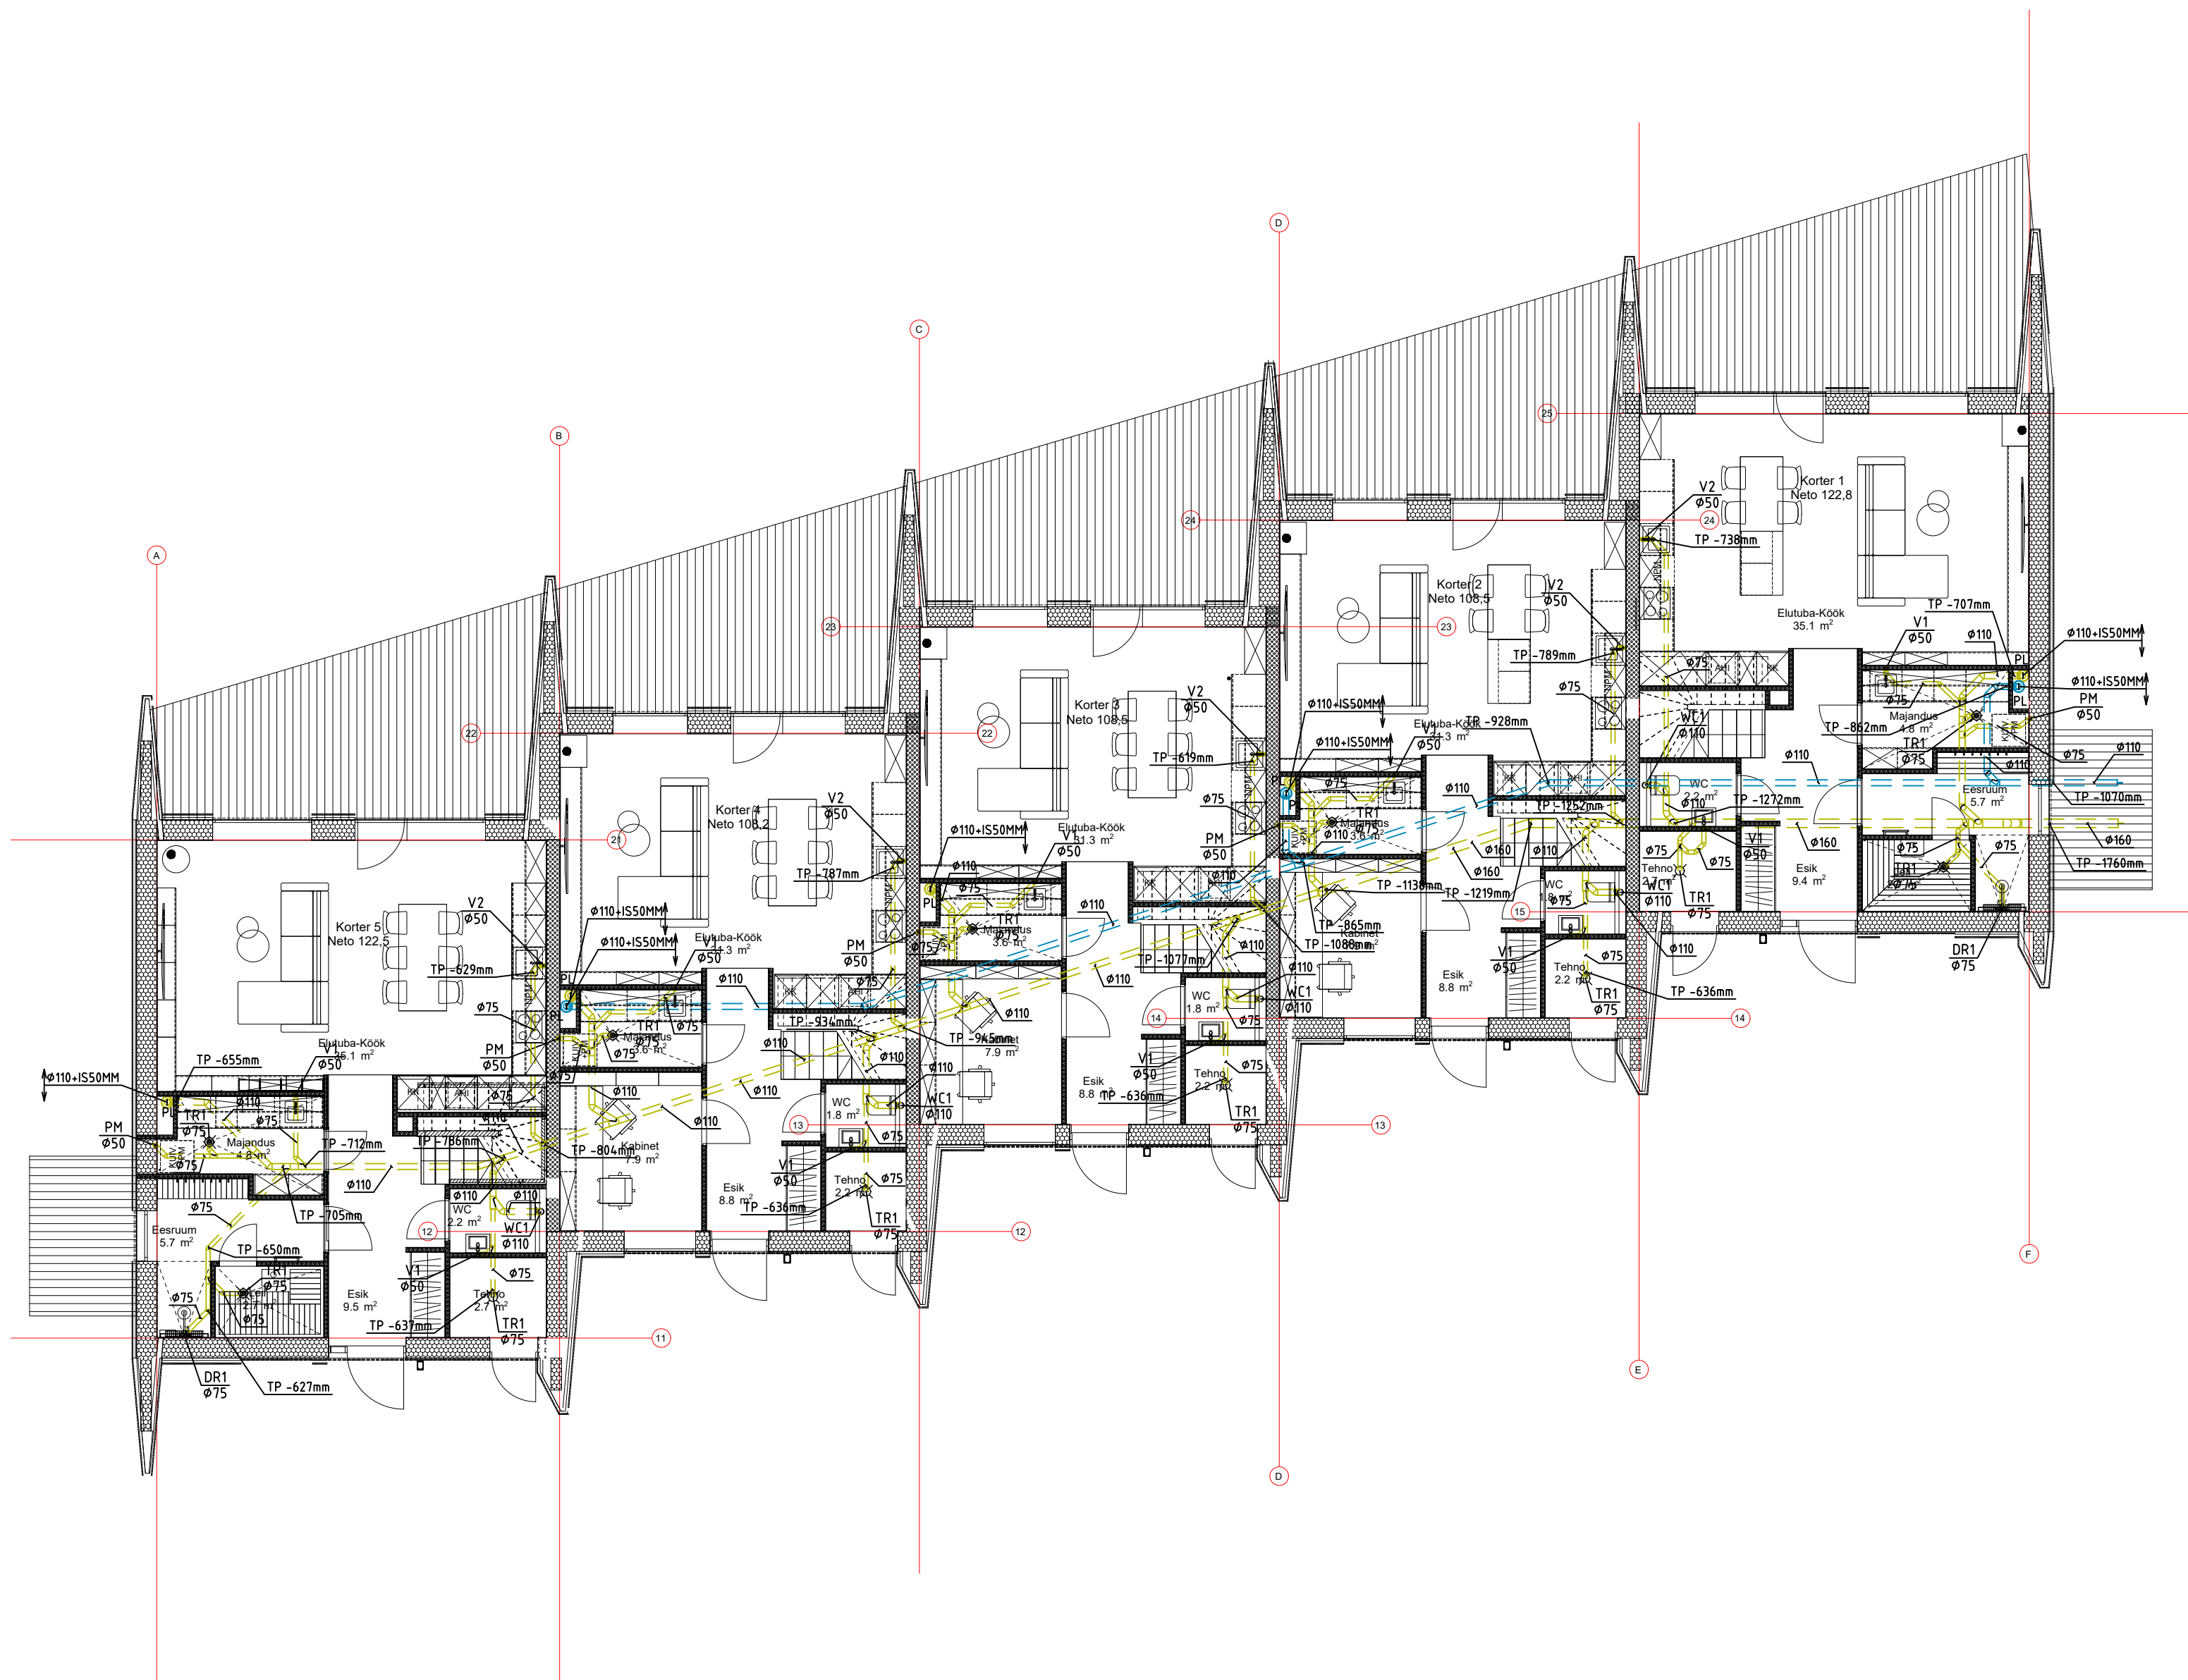

- TINGMÄRGID
- REOVEEKANALISATSIiooni TORUSTIK PÕRANDAS (K1)
 - SADEMEVEEKANALISATSIiooni TORUSTIK PÕRANDAS (K2)
 - REOVEEKANALISATSIiooni TORUSTIK LAE ALL (K1)
 - SADEMEVEEKANALISATSIiooni TORUSTIK LAE ALL (K2)
 - TR1 TRAPP R/V TERASEST RESTIGA
 - DR1 DUSHIRENN R/V TERASEST RESTIGA
 - V1 VALAMU
 - V2 KÖÖGIVALAMU
 - WC1 WC-POTT
 - PM PESUMASIN
 - TP TORU PÕHJA KÕRGUSMÄRK
 - PL PUHATUSLUUK, +1.0m PÕRANDA PINNAST

- MÄRKUSED
- HOONE SISENE REOVEE KANALISATSIOONITORUSTIK MONTEERIDA PLASTIST (PP/PVC) KANALISATSIOONITORUSTE Ø32-Ø160.
 - KÕIK KANALISATSIOONIPÜSTIKUD JA LAELUSED TORUSTIKUD ISOLEERIDA 50MM PAKSUSE ALFOOLIUMKATTEGA KIVIVILLAST TORUISOLATSIOONI KOORIKUTEGA (TIHEDUS ≤100 KG/M3), KUI EI OLE JOONISEL NÄIDATUD TEISITI. TORUISOLATSIOONI SÜTTIMISTUNDLIKUS-TULELEVIMISKLASS ON B-S1, D0.
 - KANALISATSIOONIPÜSTIKUD LÕPETADA KATUSEL UV-KINDLA TUULUTUSOTSIKUTEGA, UV-KINDLATE TUULUTUSOTSIKUTE MINIMAALNE PAIGALDUSKÕRGUS +0,7 M KATUSEPINNAST.
 - KANALISATSIOONIPÜSTIKUTE KÕIGE ALUMISELE KORRUSELE TULEB PAIGALDADA PUHASTUSLUUGID 1,0M KÕRGUSELE PÕRANDAST JA PUHASTUSLUUKIDE HOOLDUSLUUGID PEAVAD VASTAMA KONSTRUKTSIOONI TULEKAITSEASTMELE.
 - KÕIK PLASTTORUDE LÄBIVIIGUD TULETÕKKE TARINDIDEST VARUSTADA TULETÕKKEMANSETTIDEGA, TULETÕKKEMÄHISTEGA VÕI TORUDELE KUINI Ø50 MM SPESTIAALSE PAISUVA TULETÕKKESILUKOONIGA.
 - TORUSTIKU LÄBIVIIGUDE TEGEMISEL TULEB JÄLGIDA KONSTRUKTIIVSE JA ARHITEKTUURSE OSA JOONISEID. TORUSTIKE LÄBIVIIGUD VUNDAMENTIDEST JA VUNDAMENTIDE ALT TEHA HÜLSIS (ÜKS MÕOT TORUST SUUREM).
 - KÖÖGIVALAMU KÕRVAL PAKNEVAD NÕUDEPESUMASINAD KANALISEERIDA LÄBI KÖÖGIVALAMU SIFOONI.
 - TORUSTIKE PAIGALDAMISEL ARVESTADA TEISTE ERIOSADEGA.

Tähis	Muudatus	Teostaja	Kuupäev
TÖÖ NIMETUS	RIDAELAMU	TELLUA	SAKU ARENDUS OÜ
ADRESS	KUU TEE 16, SAKU, SAKU VALD, HARJUMAA	JOONIS	KANALISATSIOON. 1-KORRUS
Smart Pipes OÜ Registrikood 119753996 tel +372 628 8802 info@smartpipes.ee Majaka tn 44-9, Tallinn, Harjumaa, 11412 MTR EEP001986, EPE000622	VASTUTAV SPETSIALIST V.LOORENTS PROJEKTEERUA V.LOORENTS OSA VK	kuupäev 16.03.2025	FAILI NIMI 24060_VK_1-korrus.dwg TÖÖ NR 24060-1 MÕÖTKAVA 1:100 JOONISE NR VK-3 JOONISTE ARV