


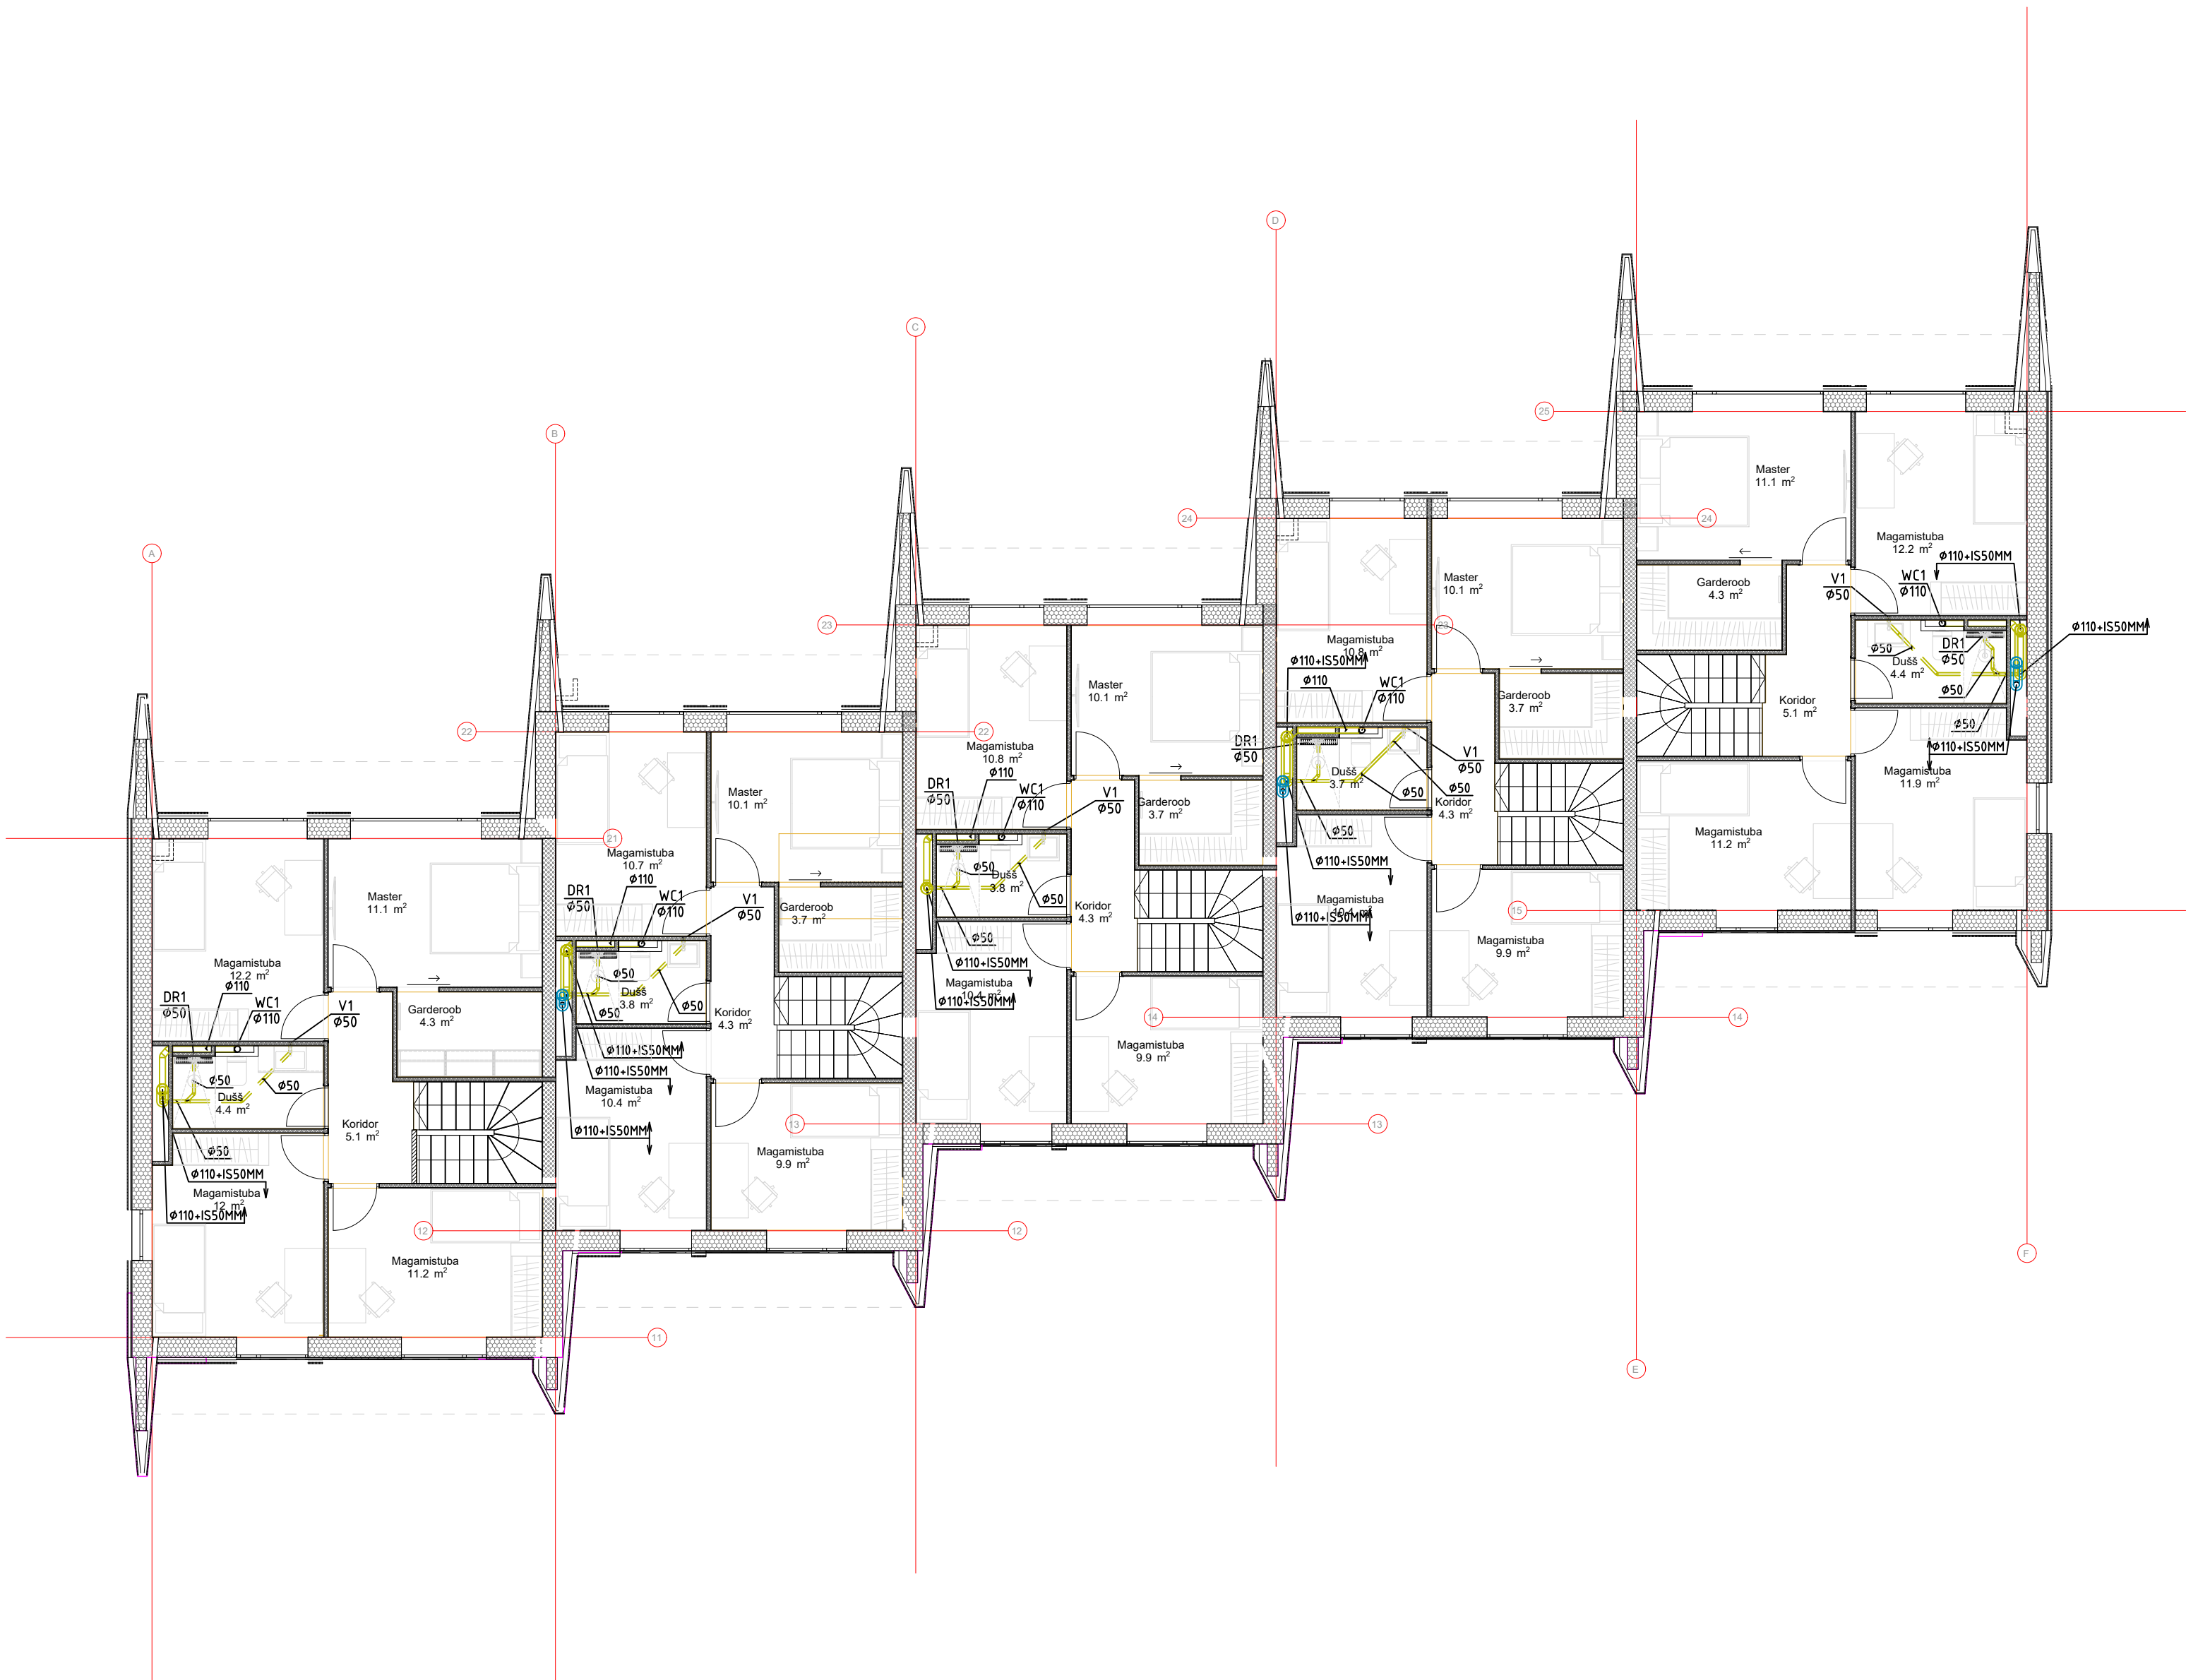

- TINGMÄRGID
- REOVEEKANALISATSIiooni TORUSTIK PÕRANDAS (K1)
 - SADEMEVEEKANALISATSIiooni TORUSTIK PÕRANDAS (K2)
 - REOVEEKANALISATSIiooni TORUSTIK LAE ALL (K1)
 - SADEMEVEEKANALISATSIiooni TORUSTIK LAE ALL (K2)
 - DR1 DUSHIRENN R/V TERASEST RESTIGÄ
 - V1 VALAMU
 - WC1 WC-POTT

- MÄRKUSED
- HOONE SISENE REOVEE KANALISATSIIONITORUSTIK MONTEERIDA PLASTIST (PP/PVC) KANALISATSIIONITORUDEST Ø32-Ø160.
 - KÕIK KANALISATSIIONIPÜSTIKUD JA LAELASED TORUSTIKUD ISOLEERIDA 50MM PAKSUSE ALFOOLIUMKATTEGA KIVIVILLAST TORUISOLATSIIONI KOORIKUTEGA (TIHEDUS ≤100 KG/M3), KUI EI OLE JOONISEL NÄIDATUD TEISITI. TORUISOLATSIIONI SÜTTIMISTUNDLIKUS-TULELEVIMISKLASS ON B-S1, D0.
 - KANALISATSIIONIPÜSTIKUD LÕPETADA KATUSEL UV-KINDLA TUULUTUSOTSIKUTEGA, UV-KINDLATE TUULUTUSOTSIKUTE MINIMAALNE PAIGALDUSKÕRGUS +0,7 M KATUSEPINNAST.
 - KANALISATSIIONIPÜSTIKUTE KÕIGE ALUMISELE KORRUSELE TULEB PAIGALDADA PUHASTUSLUUGID 1,0M KÕRGUSELE PÕRANDAST JA PUHASTUSLUUKIDE HOOLDUSLUUGID PEAVAD VASTAMA KONSTRUKTSIOONI TULEKAITSEASTMELE.
 - KÕIK PLASTTORUDE LÄBIVIIGUD TULETÕKKE TARINDIDEST VARUSTADA TULETÕKKEMANSETTIDEGA, TULETÕKKEMÄHISTEGA VÕI TORUDELE KUNI Ø50 MM SPETIAALSE PAISUVA TULETÕKKESILUKOONIGA.
 - TORUSTIKU LÄBIVIIGUDE TEGEMISEL TULEB JÄLGIDA KONSTRUKTIIVSE JA ARHITEKTUURSE OSA JOONISEID. TORUSTIKE LÄBIVIIGUD VUNDAMENTIDEST JA VUNDAMENTIDE ALT TEHA HÜLSIS (ÜKS MÕÖT TORUST SUUREM).
 - KÕÕGIVALAMU KÕRVAL PAKNEVAD NÕUDEPESUMASINAD KANALISEERIDA LÄBI KÕÕGIVALAMU SIFOONI.
 - TORUSTIKE PAIGALDAMISEL ARVESTADA TEISTE ERISADEGA.

01	Muutunud katuse läbiviikude asukohad	V.Loorents	08.05.2025
Tähis	Muudatus	Teostaja	Kuupäev
TÖÖ NIMETUS RIDAEELAMU		TELLUA SAKU ARENDUS OÜ	
Aadress KUU TEE 16, SAKU, SAKU VALD, HARJUMAA		JOONIS KANALISATSIIOON. 2-KORRUS	
Smart Pipes OÜ Registrikood 11975398 tel +372 628 8802 info@smartpipes.ee Majaka tn 44-9, Tallinn, Harjumaa, 11412 MTR EEP001986, EPE000622		VASTUTAV SPETSIALIST V.LOORENTS PROJEKTEERUA V.LOORENTS OSA VK	FAILI NIMI 24060_VK_2-korrus.dwg TÖÖ NR 24060-1 MÕÖTKAVA 1:100 JOONISE NR VK-4 JOONISTE ARV