



VALGUSTITE TINGMÄRGID		
Tähis	Tingmärk	Nimetus
V-01	⊗	Süvisvalgusti
V-02	⊗	Süvisvalgusti niiskukindel
V-03	↔	Pinnapealne laevalgusti
V-04	⊗	Pinnapealne laevalgusti
V-06.1	—	Peegel valgustusega
V-06.2	—	Peegel valgustusega
V-07	⊗	Laevalgusti
V-LED	—	LEDriba valgustus mööblis toide

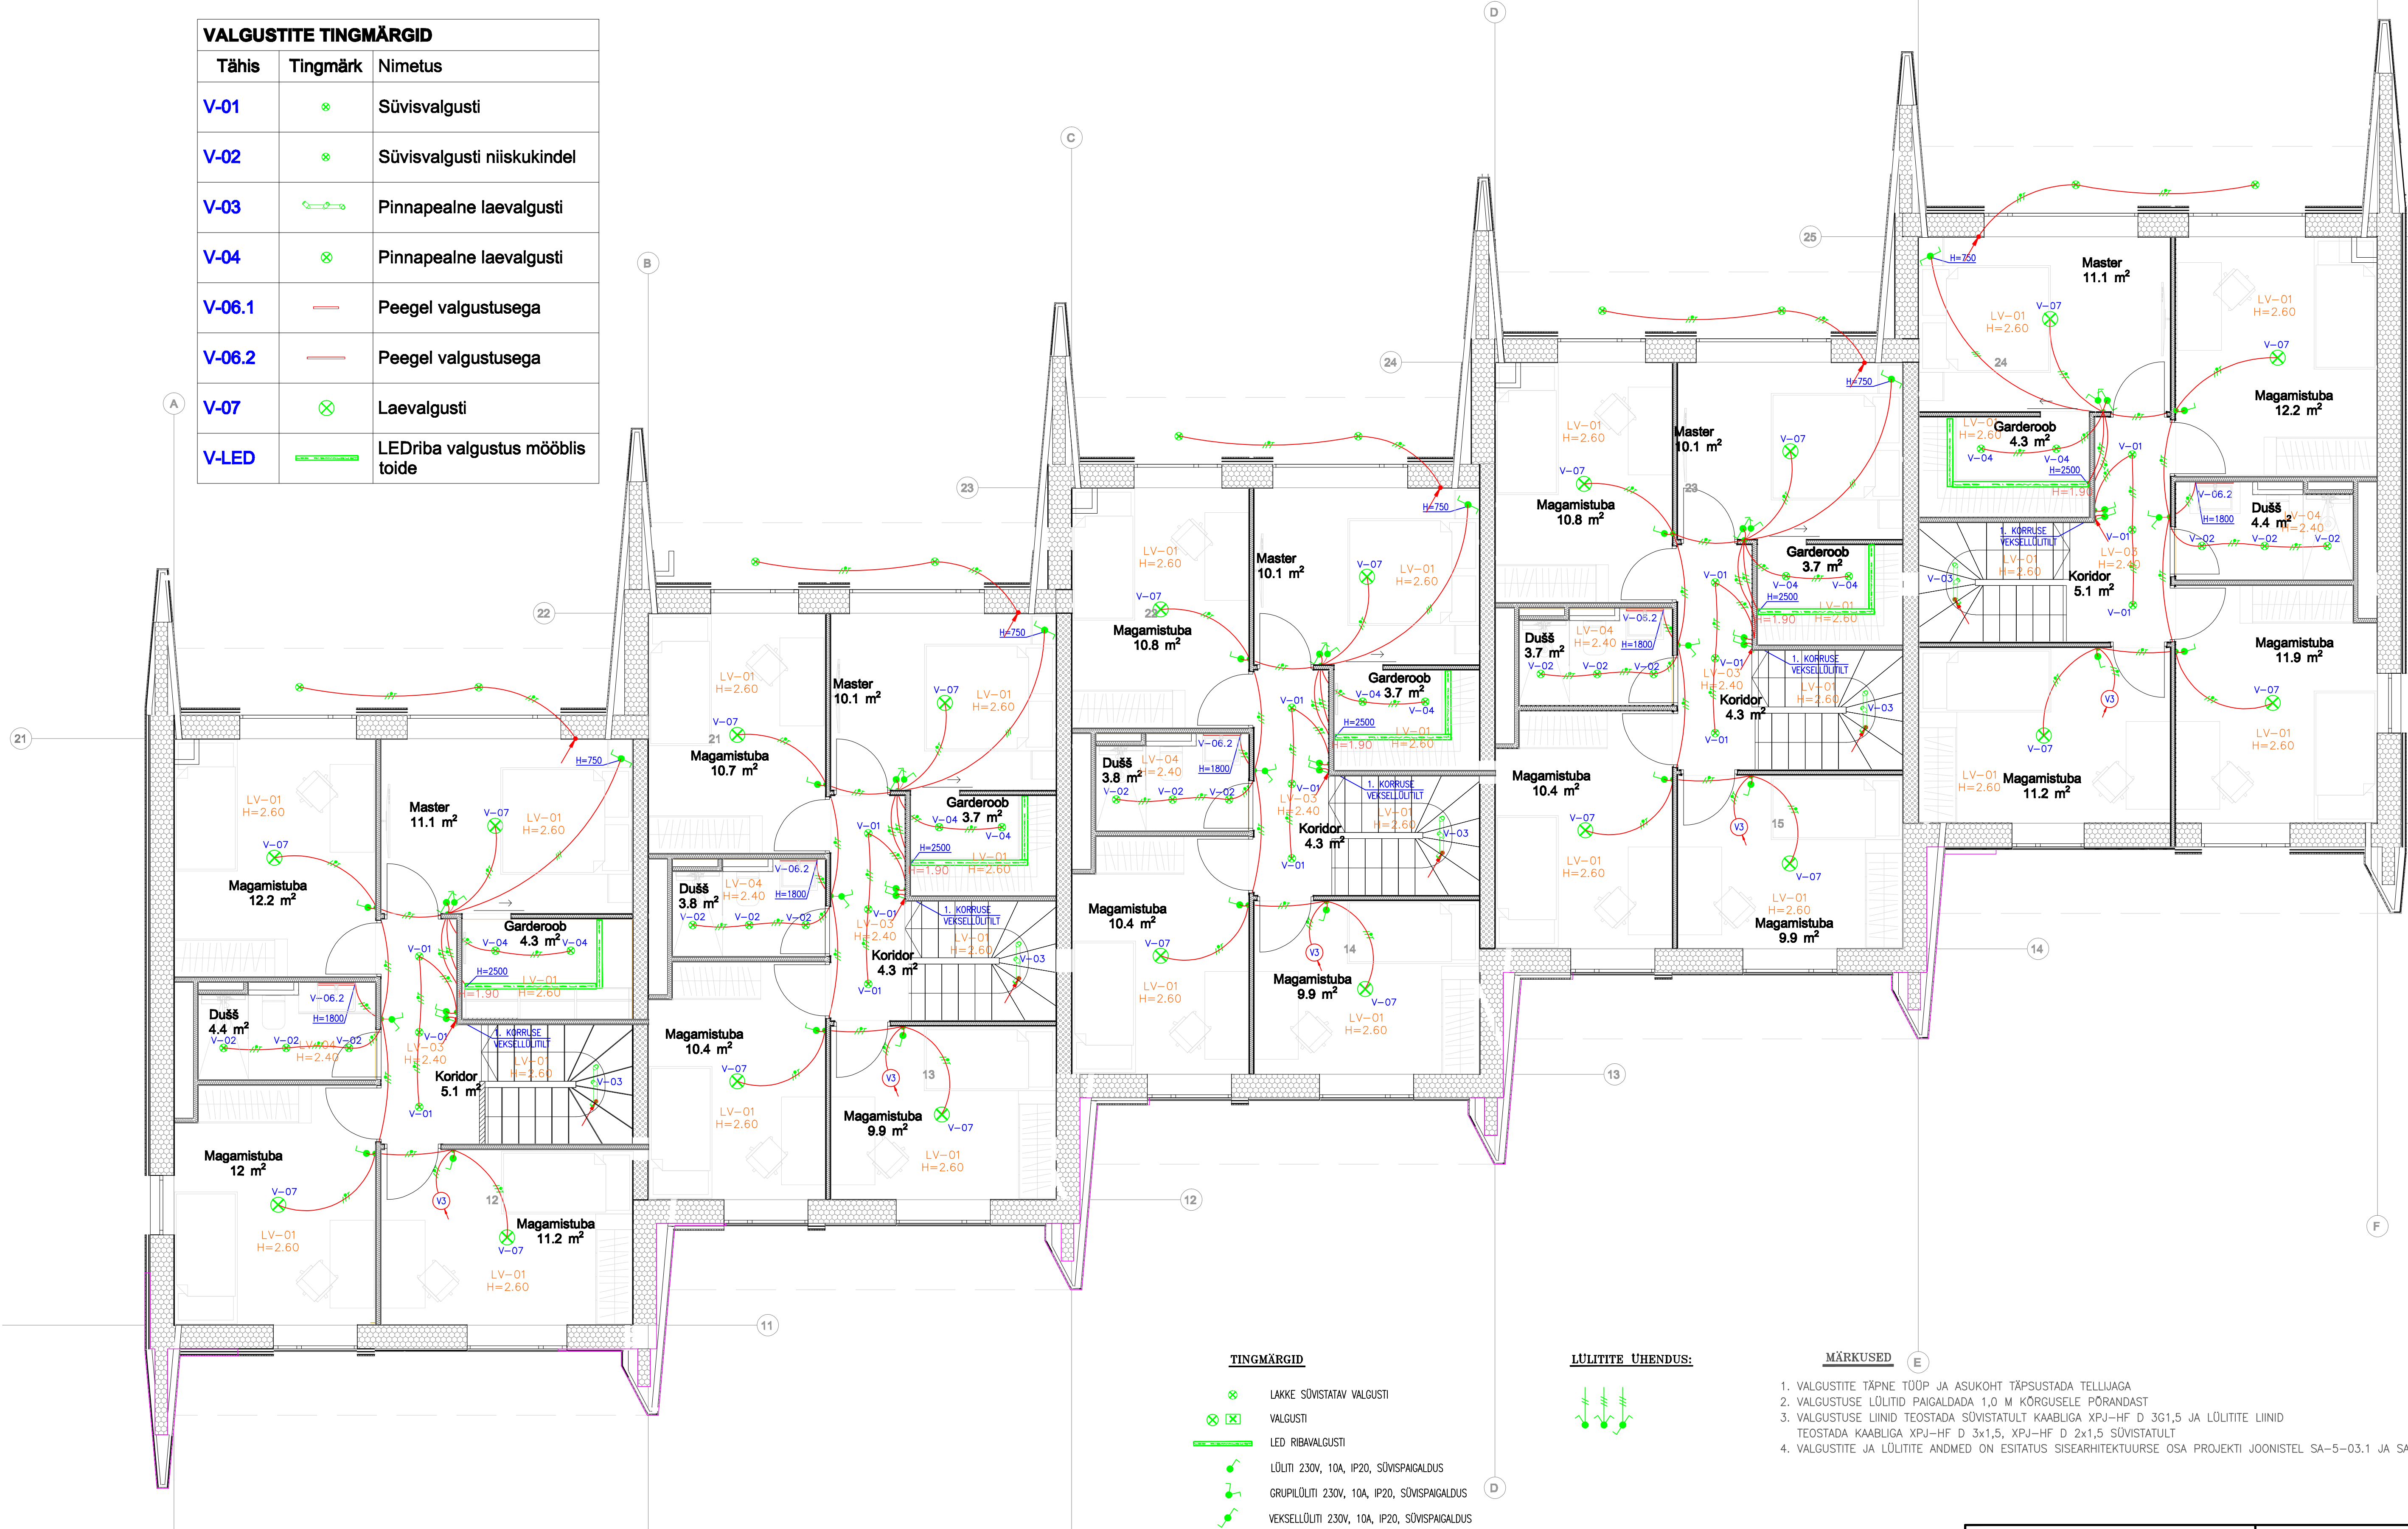

TINGMÄRGID

- ⊗ LAKKE SÖVISTATAV VALGUSTI
- ⊗ VALGUSTI
- LED RIBAVALGUSTI
- ↔ LÖLITI 230V, 10A, IP20, SÖVISPAIGALDUS
- ↔ GRUPILOLITI 230V, 10A, IP20, SÖVISPAIGALDUS
- ↔ VEKSELLÖLITI 230V, 10A, IP20, SÖVISPAIGALDUS

LÜLITITE ÜHENDUS:

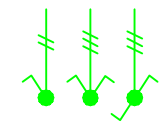

MÄRKUSED

- VALGUSTITE TÄPNE TÖÖP JA ASUKOHT TÄPSUSTADA TELLIJAGA
- VALGUSTUSE LÖLITID PAIGALDADA 1,0 M KÕRGUSELE PÕRANDAST
- VALGUSTUSE LIINID TEOSTADA SÖVISTATULT KAABLIGA XPJ-HF D 3G1,5 JA LÖLITITE LIINID TEOSTADA KAABLIGA XPJ-HF D 3x1,5, XPJ-HF D 2x1,5 SÖVISTATULT
- VALGUSTITE JA LÖLITITE ANDMED ON ESITATUS SISEARHITEKTUURSE OSA PROJEKTI JOONISTEL SA-5-03.1 JA SA-5-03.2

Tellija NOBE OÜ		Töö RIDAELAMU ELEKTRIPAIGALDIS	
Objekt KOMEEDI TN. 2, SAKU, SAKU VALD, HARJUMAA		Töö nr: 2419	
Joonis 2.KORRUSE VALGUSTUSPAIGALDISE PLAAN			
Projekteeris: V. RANNAKIVI	 VivaLight	Muudatus: Staudium: PÕHIPROJEKT	Joonise nr: EL-02
Kontrollis:	TEL-000204	Falt: 2419_PP_E-4-02_V01_2c.külg	Leht/Neli: 1/1
Kuupäev: 28.02.2025		Tel. 5142331	Mööblit: 1:50