


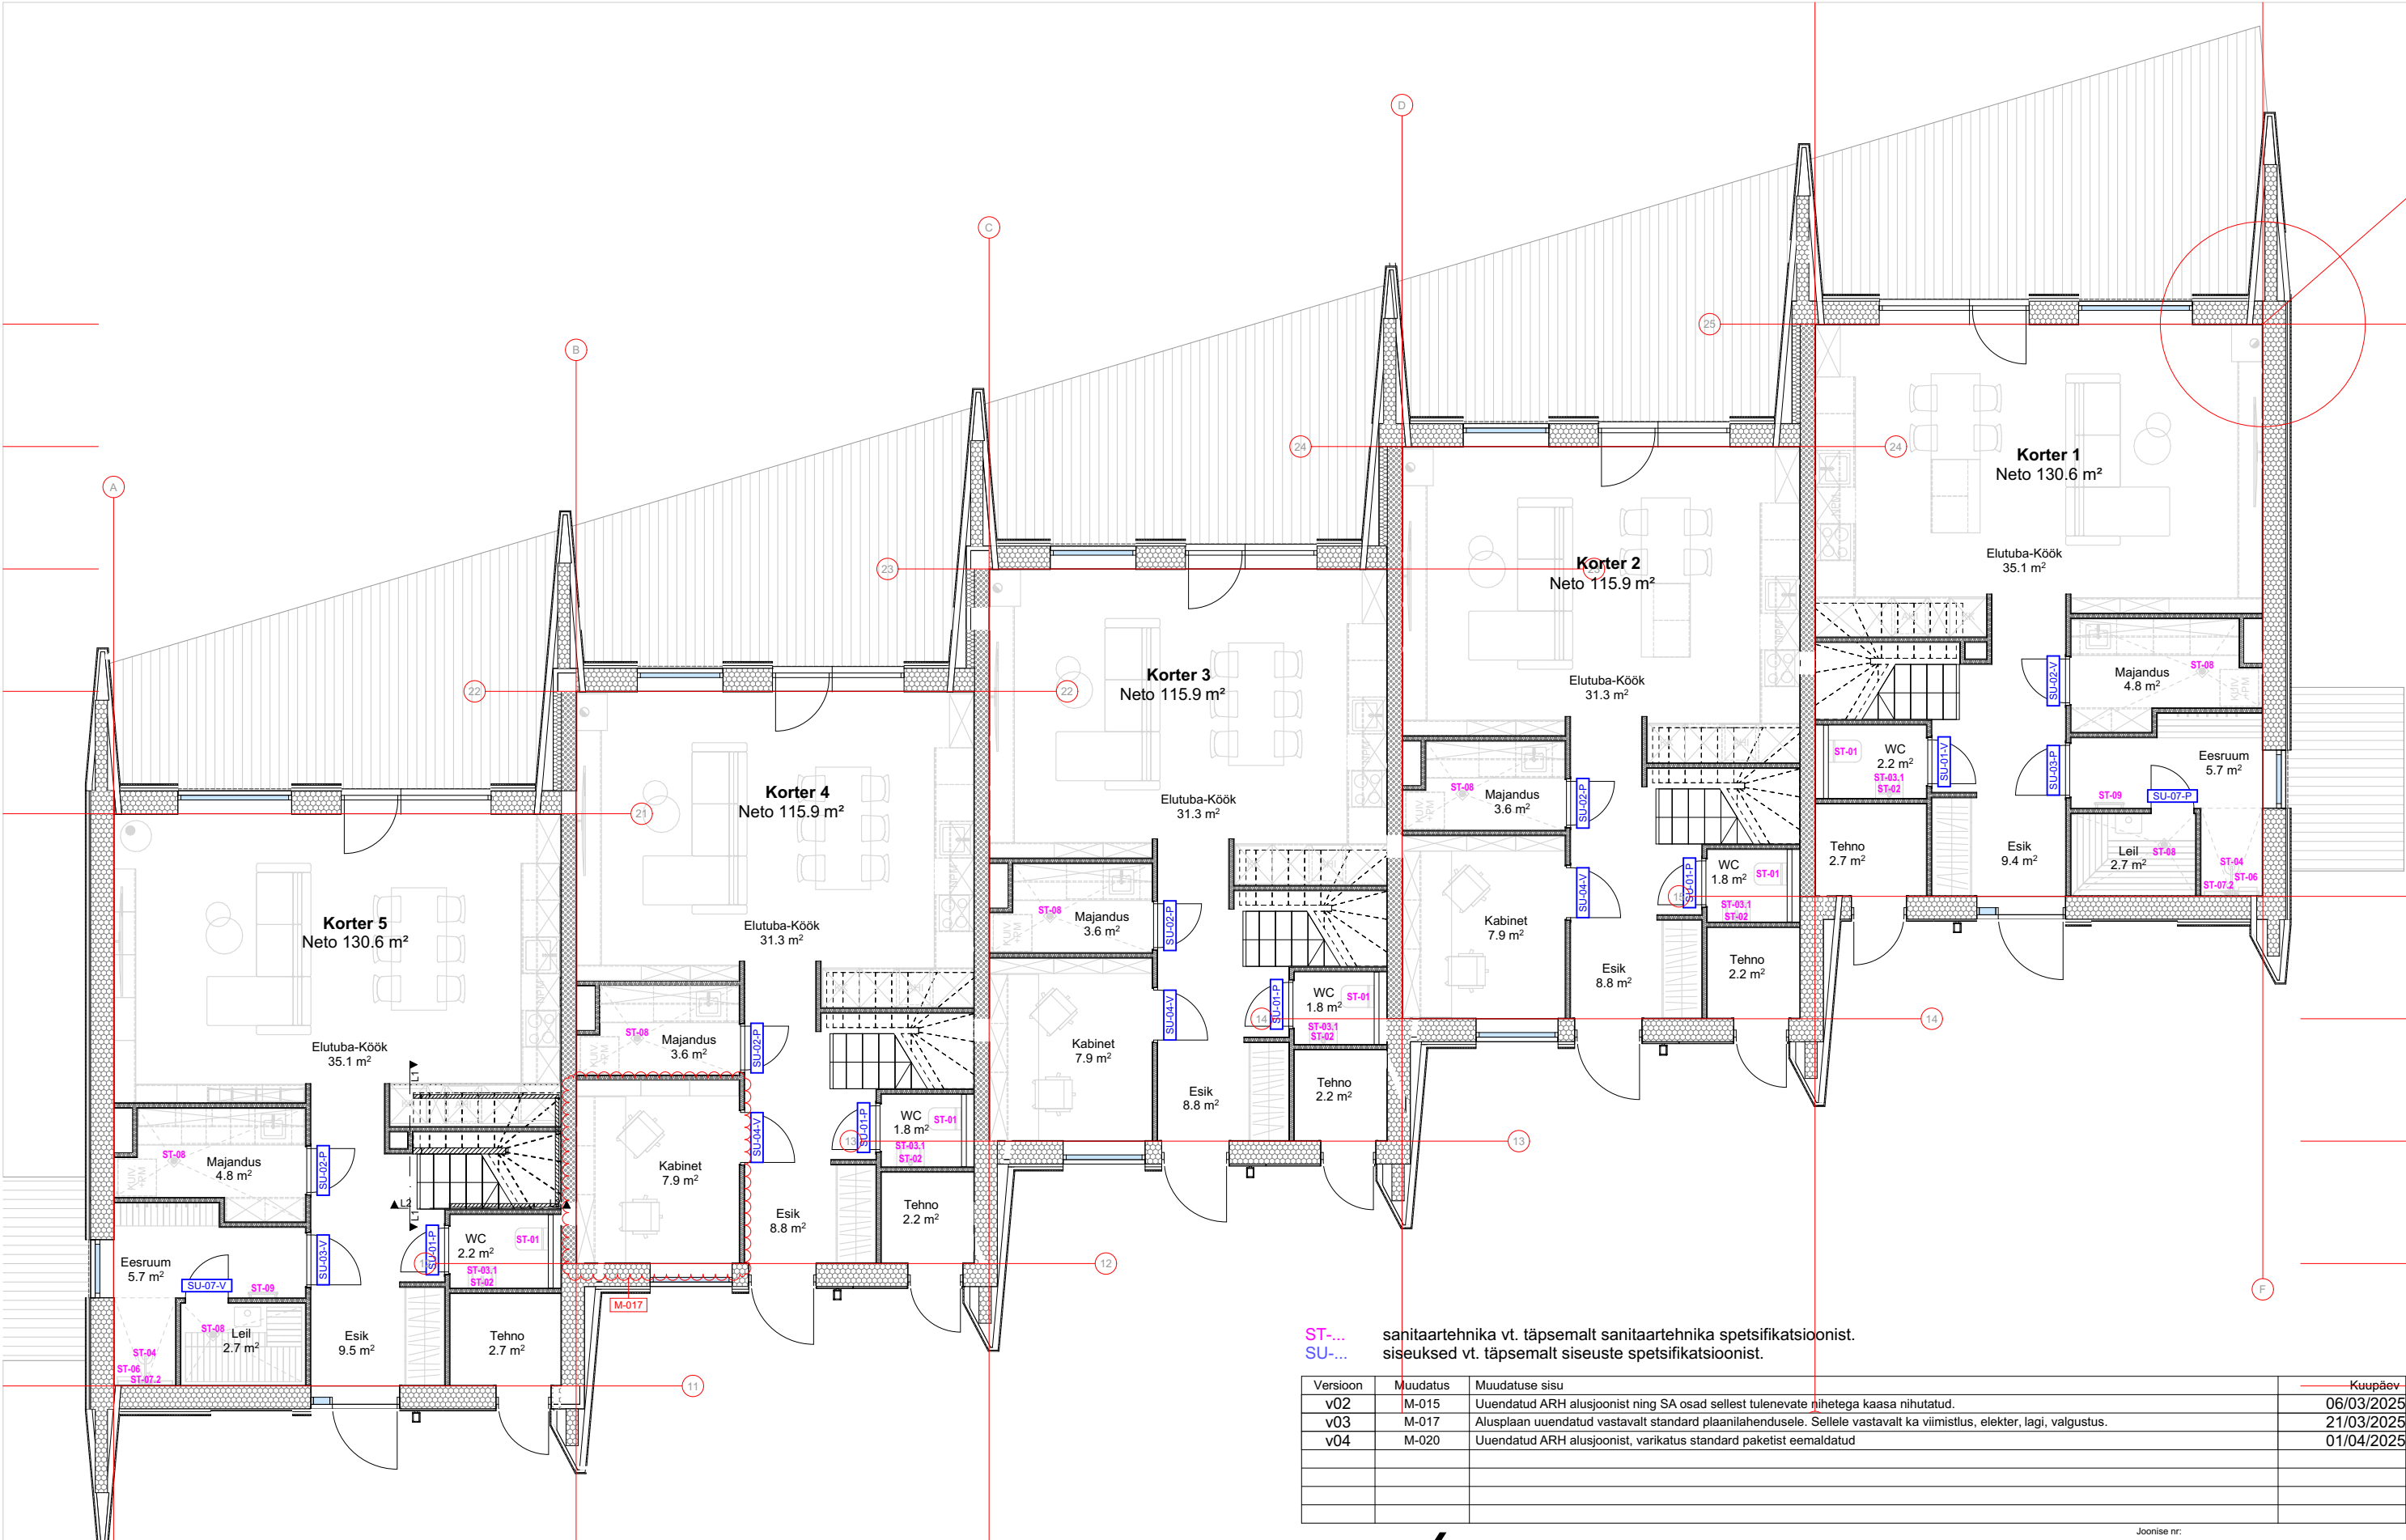

ÜLDMÄRKUSED:

- Käesolevat joonist käsitleda koos teiste projektiosadega. Vastuolude ilmnemisel võtta ühendust projekteerijaga.
- Kõikide materjalide ja ehitustööde kvaliteet peab vastama Eesti Vabariigis kehtivate seadusandlike aktide järgi kehtestatud nõuetele ja olema kooskõlas hea ehitustavaga.
- Kõik ehitusega seotud muudatused konstruktsioonide, mõõtude, materjalide, avatäidete, piirete, detailide jms. osas kooskõlastada kõigepealt projekteerijaga, seejärel tellijaga.
- Enne uste, akende, piirete, detailide ja muude sarnaste elementide valmistamist kontrollida eelnevalt avade ja karkassi tegelikud mõõtmed, avanemissuunad ja kogused.
- **Tootejoonised kooskõlastada enne valmistamist projekti sisearhitektiga.**
- **Kõik mõõdud tuleb kohapeal üle mõõta ja kontrollida reaalsel olukorda platsil. Vastuolude ilmnemisel võtta ühendust sisearhitektiga.**

ST-... sanitaartechnika vt. täpsemalt sanitaartechnika spetsifikatsioonist.
SU-... siseüksed vt. täpsemalt siseuste spetsifikatsioonist.

Versioon	Muudatus	Muudatuse sisu	Kuupäev
v02	M-015	Uuendatud ARH alusjoonist ning SA osad sellest tulenevate nihetega kaasa nihutatud.	06/03/2025
v03	M-017	Alusplaan uuendatud vastavalt standard plaanilahendusele. Sellele vastavalt ka viimistlus, elekter, lagi, valgustus.	21/03/2025
v04	M-020	Uuendatud ARH alusjoonist, varikatus standard paketest eemaldatud	01/04/2025

ARHITEKT

Objekt:

Saku Ridaelamu

Address:

Kuu tee 16 Saku

Joonis:

1K pohlplan

Projekteeris:

Tiiu Rull

Arhitekt11 OÜ, reg nr 12190827; Joa 2/1, 10127 Tallinn, Eesti; info@arhitekt11.ee; KMKR EE101499183

Joonise nr:

SA-5-01.1

Esm. väljaandmise kp:

17/01/2025

Kuupäev:

01/04/2025

Versioon:

v04

Mõõkava:

1:100

Formaat:

A3

Stadium:

PP

Töö nr:

2024-11-01

Projekti juht:

Rita Ratušnaja

+372 512 4858; rita.ratushnaja@arhitekt11.ee