


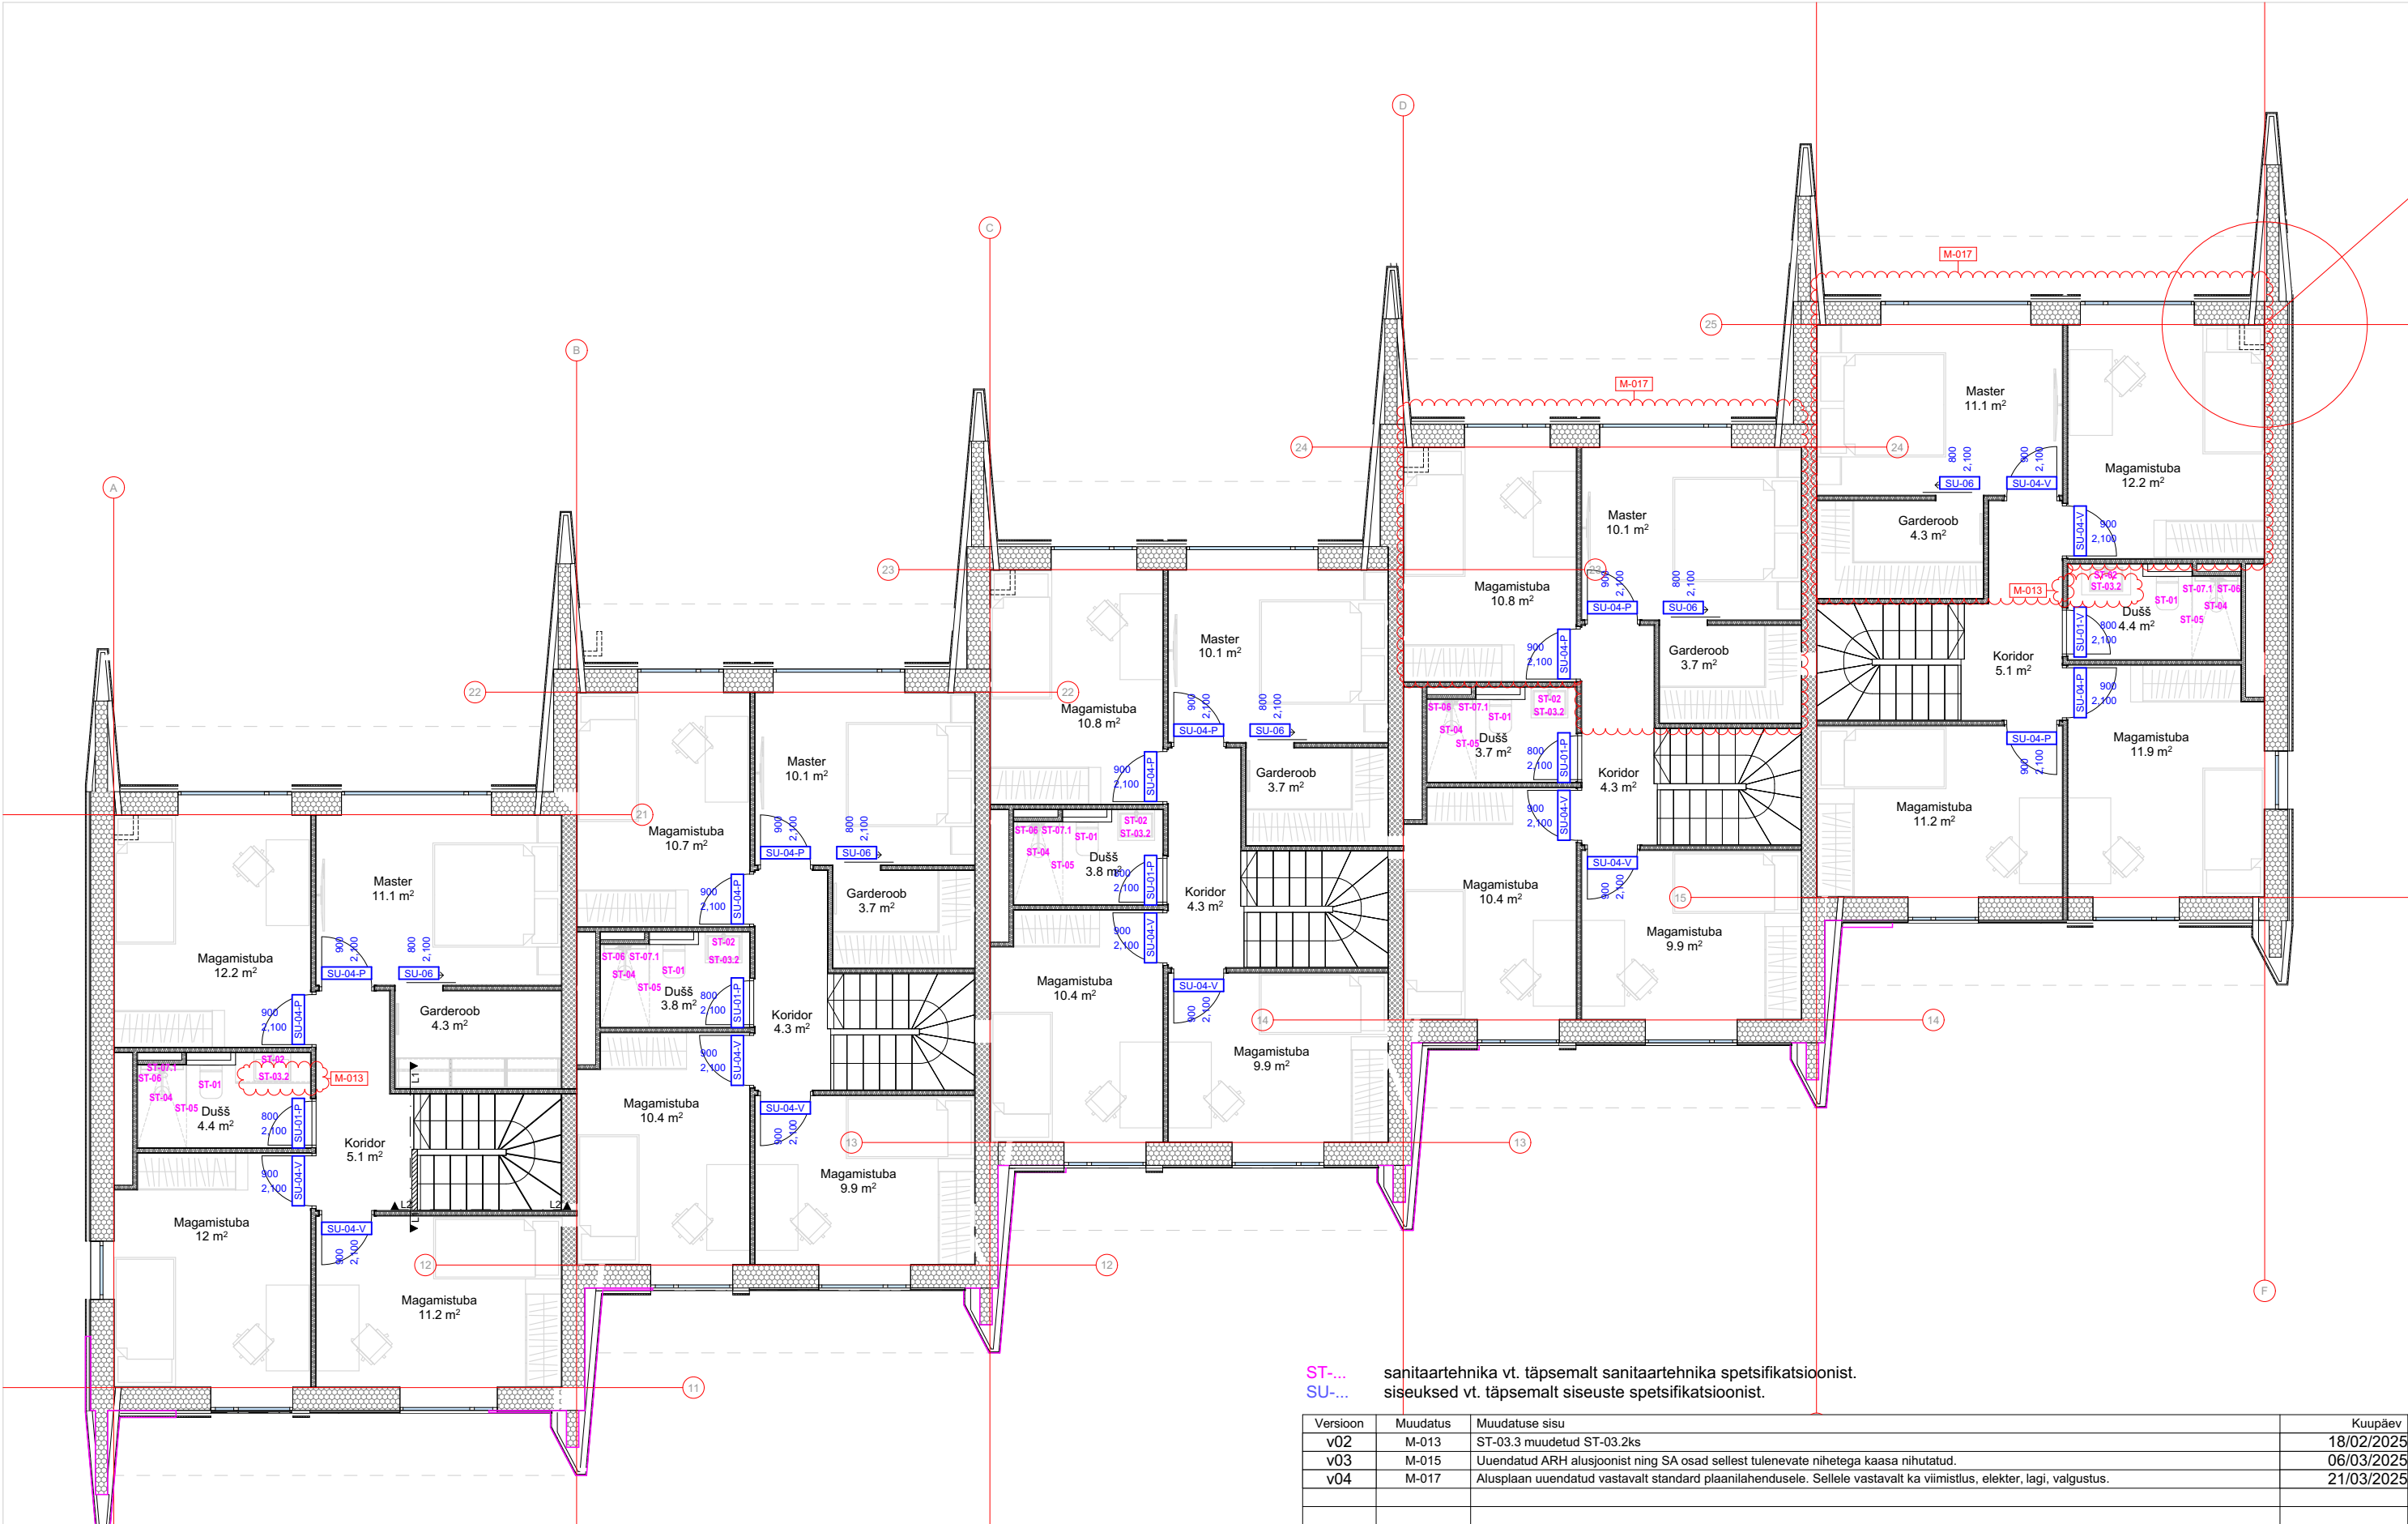

ST-... sanitaartehnika vt. täpsemalt sanitaartehnika spetsifikatsioonist.
SU-... siseüksed vt. täpsemalt siseuste spetsifikatsioonist.

Version	Muudatus	Muudatuse sisu	Kuupäev
v02	M-013	ST-03.3 muudetud ST-03.2ks	18/02/2025
v03	M-015	Uuendatud ARH alusjoonist ning SA osad sellest tulenevate nihetega kaasa nihutatud.	06/03/2025
v04	M-017	Alusplaan uuendatud vastavalt standard plaanilahendusele. Sellele vastavalt ka viimistlus, elekter, lagi, valgustus.	21/03/2025

ARHITEKT

Objekt:
Saku Ridaelamu

Joonis:
2K pohlplan

Projekteeris:
Tiiu Rull

Arhitekt11 OÜ, reg nr 12190827; Joa 2/1, 10127 Tallinn, Eesti; info@arhitekt11.ee; KMKR EE101499183

Aadress:
Kuu tee 16 Saku

Vastutav spetsialist:
Hannelore Kääramees

Joonise nr:
SA-5-01.2

Esm. väljaandmise kp:
17/01/2025

Mõõkava:
1:100

Töö nr:
2024-11-01

Projekti juht:
Rita Ratušnaja

Kuupäev:
21/03/2025

Formaat:
A3

Stadium:
PP

+372 512 4858; rita.ratushnaja@arhitekt11.ee

ÜLDMÄRKUSED:

- Käesolevat joonist käsitleda koos teiste projektiosadega. Vastuolude ilmnemisel võtta ühendust projekteerijaga.
- Kõikide materjalide ja ehitustööde kvaliteet peab vastama Eesti Vabariigis kehtivate seadusandlike aktide järgi kehtestatud nõuetele ja olema kooskõlas hea ehitustavaga.
- Kõik ehitusega seotud muudatused konstruktsioonide, mõõtude, materjalide, avatäidete, piirete, detailide jms. osas kooskõlastada kõigepealt projekteerijaga, seejärel tellijaga.
- Enne uste, akende, piirete, detailide ja muude sarnaste elementide valmistamist kontrollida eelnevalt avade ja karkassi tegelikud mõõtmed, avanemissuunad ja kogused.
- **Tootejoonised kooskõlastada enne valmistamist projekti sisearhitektiga.**
- **Kõik mõõdud tuleb kohapeal üle mõõta ja kontrollida reaalsel olukorda platsil. Vastuolude ilmnemisel võtta ühendust sisearhitektiga.**