


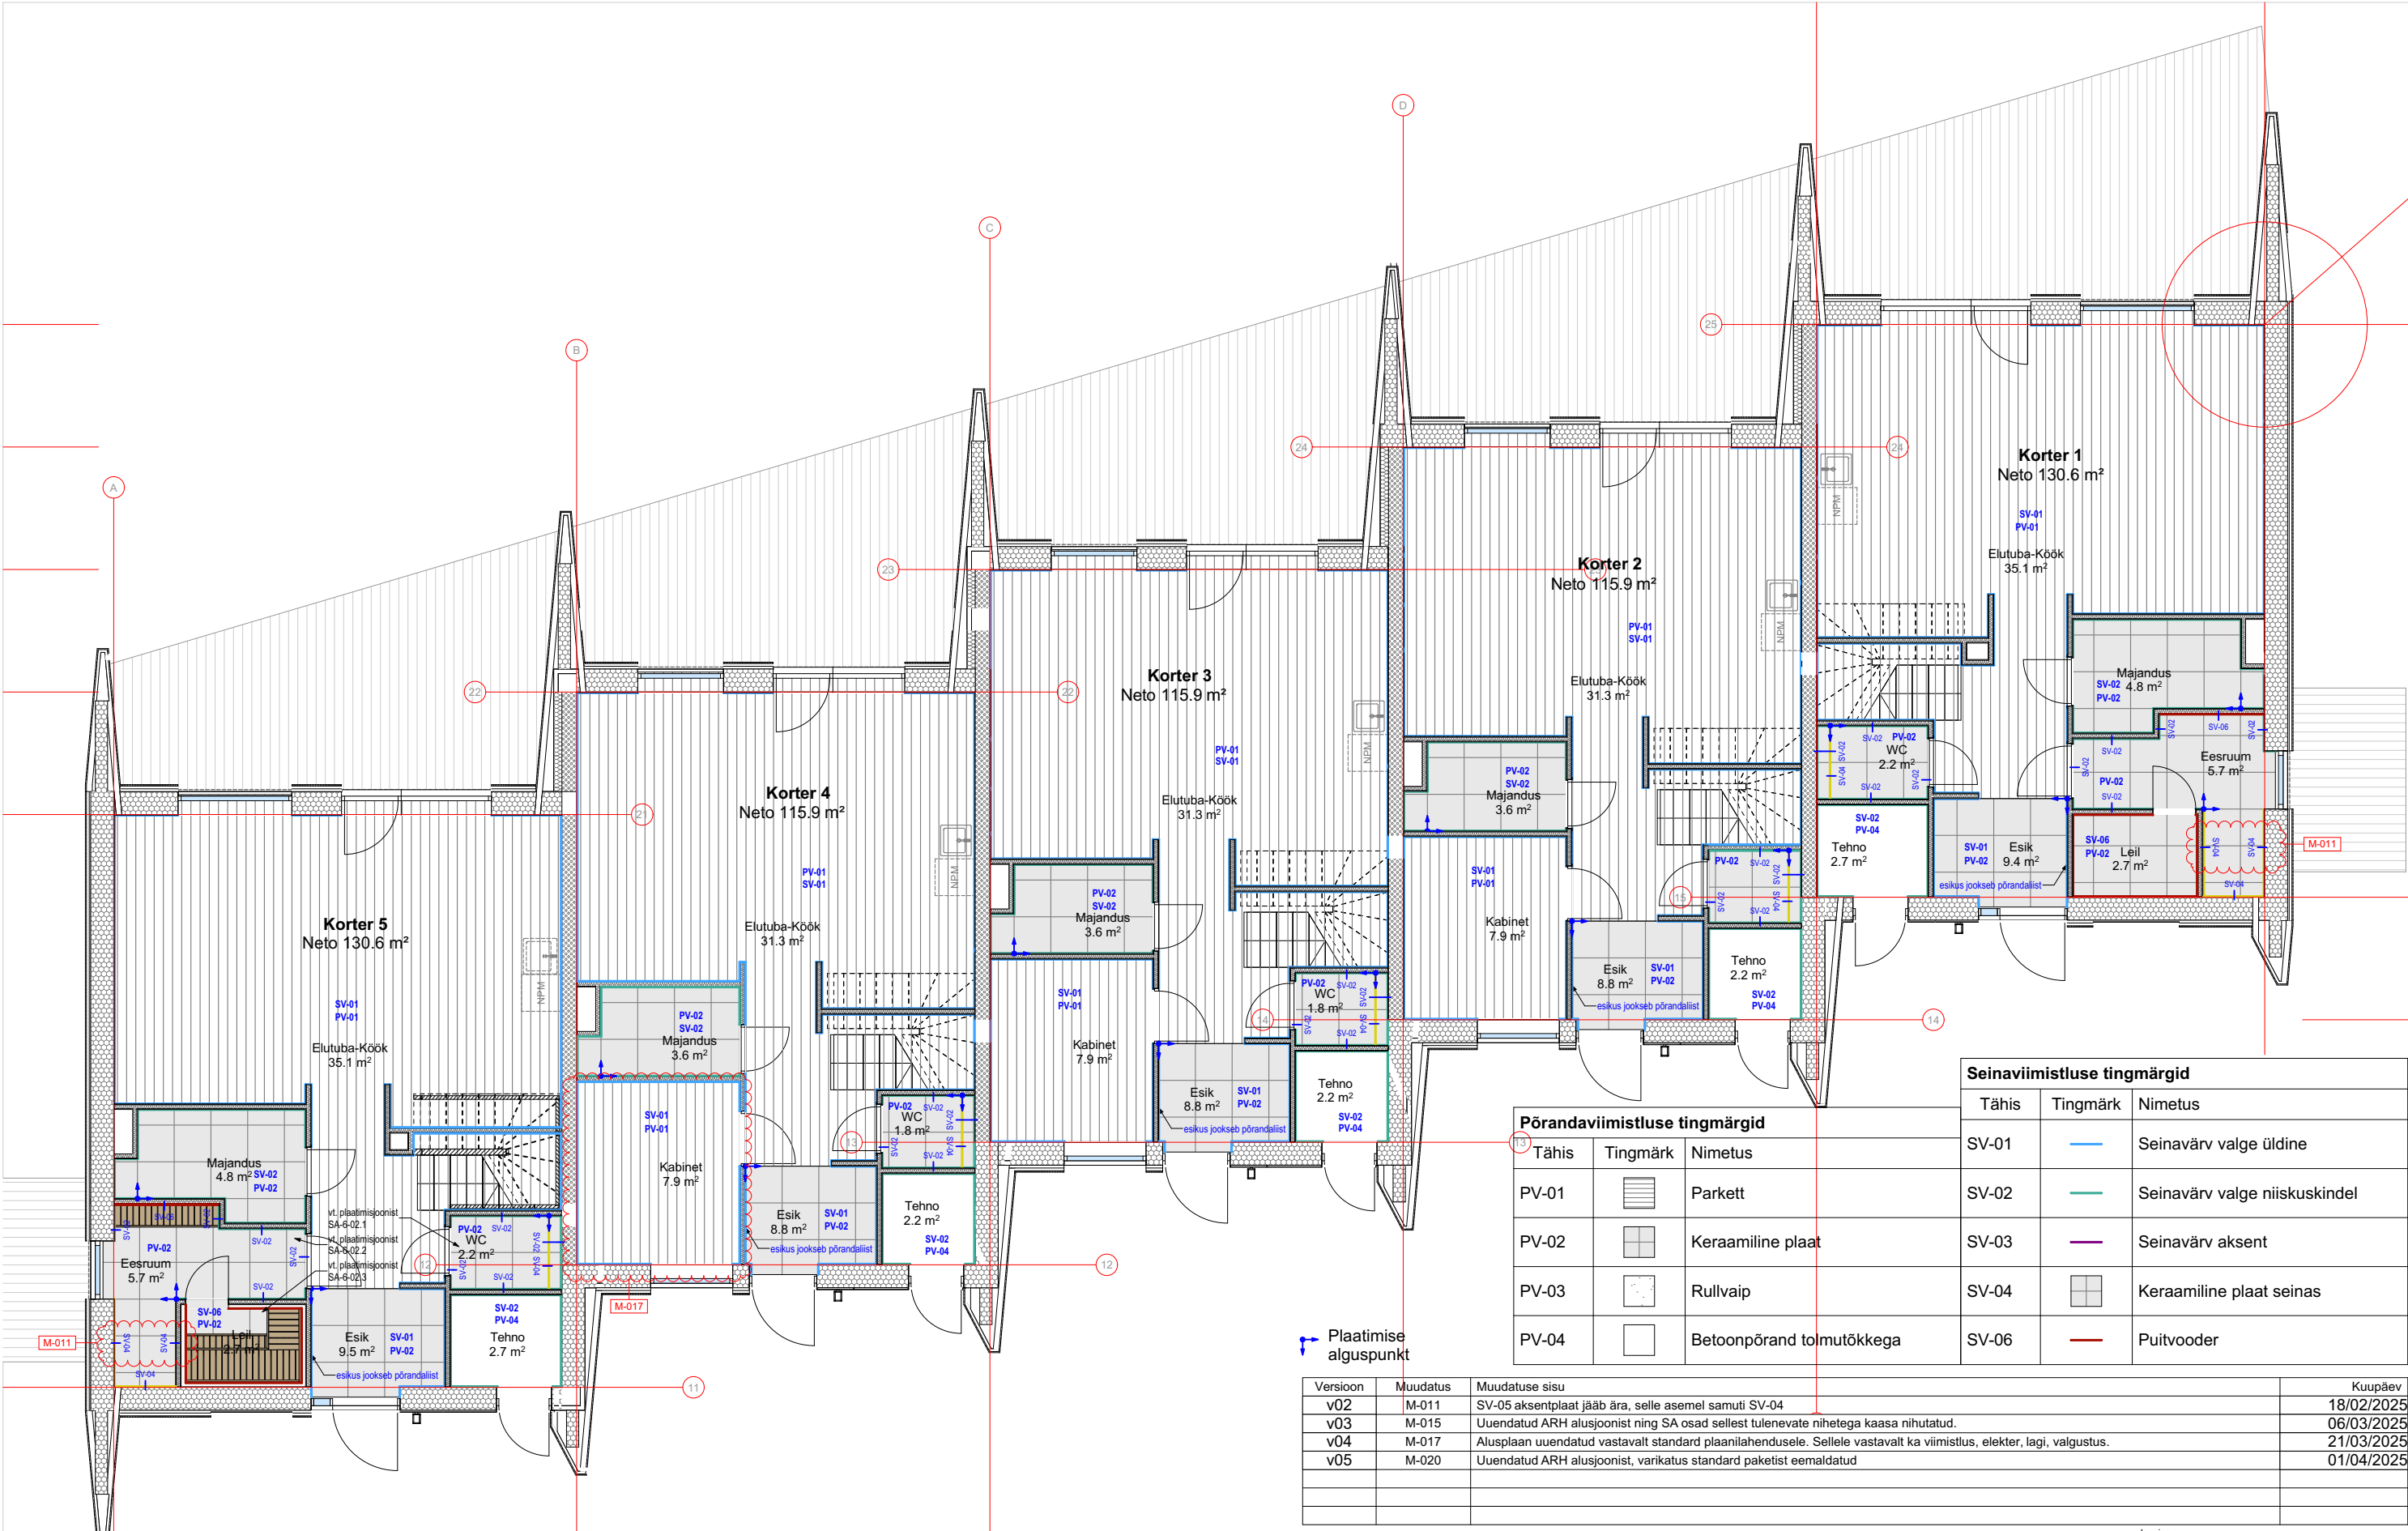

ÜLDMÄRKUSED:

- Käesolevat joonist käsitleda koos teiste projektiosadega. Vastuolude ilmnemisel võtta ühendust projekteerijaga.
- Kõikide materjalide ja ehitustööde kvaliteet peab vastama Eesti Vabariigis kehtivate seadusandlike aktide järgi kehtestatud nõuetele ja olema kooskõlas hea ehitustavaga.
- Kõik ehitusega seotud muudatused konstruktsioonide, mõõtude, materjalide, avatäidete, piirete, detailide jms. osas kooskõlastada kõigepealt projekteerijaga, seejärel tellijaga.
- Enne uste, akende, piirete, detailide ja muude sarnaste elementide valmistamist kontrollida eelnevalt avade ja karkassi tegelikud mõõtmed, avanemissuunad ja kogused.
- **Tootejoonised kooskõlastada enne valmistamist projekti sisearhitektiga.**
- **Kõik mõõdud tuleb kohapeal üle mõõta ja kontrollida reaalsel olukorda platsil. Vastuolude ilmnemisel võtta ühendust sisearhitektiga.**

ARHITEKT

Objekt:
Saku Ridaelamu

Joonis:
1K siseviimistlusplan

Projekteeris:
Tiit Rull

Arhitekt11 OÜ, reg nr 12190827; Joa 2/1, 10127 Tallinn, Eesti; info@arhitekt11.ee; KMKR EE101499183

Address:
Kuu tee 16 Saku

Vastutav spetsialist:
Hannelore Kääramees

Joonise nr:
SA-5-02.1

Esm. väljaandmise kp:	Kuupäev:	Version:
17/01/2025	01/04/2025	v05
Mõõtkava:	Formaat:	Staadium:
1:100	A3	PP
Töö nr:	2024-11-01	
Projekti juht:	Rita Ratušnaja	
+372 512 4858; rita.ratushnaja@arhitekt11.ee		