


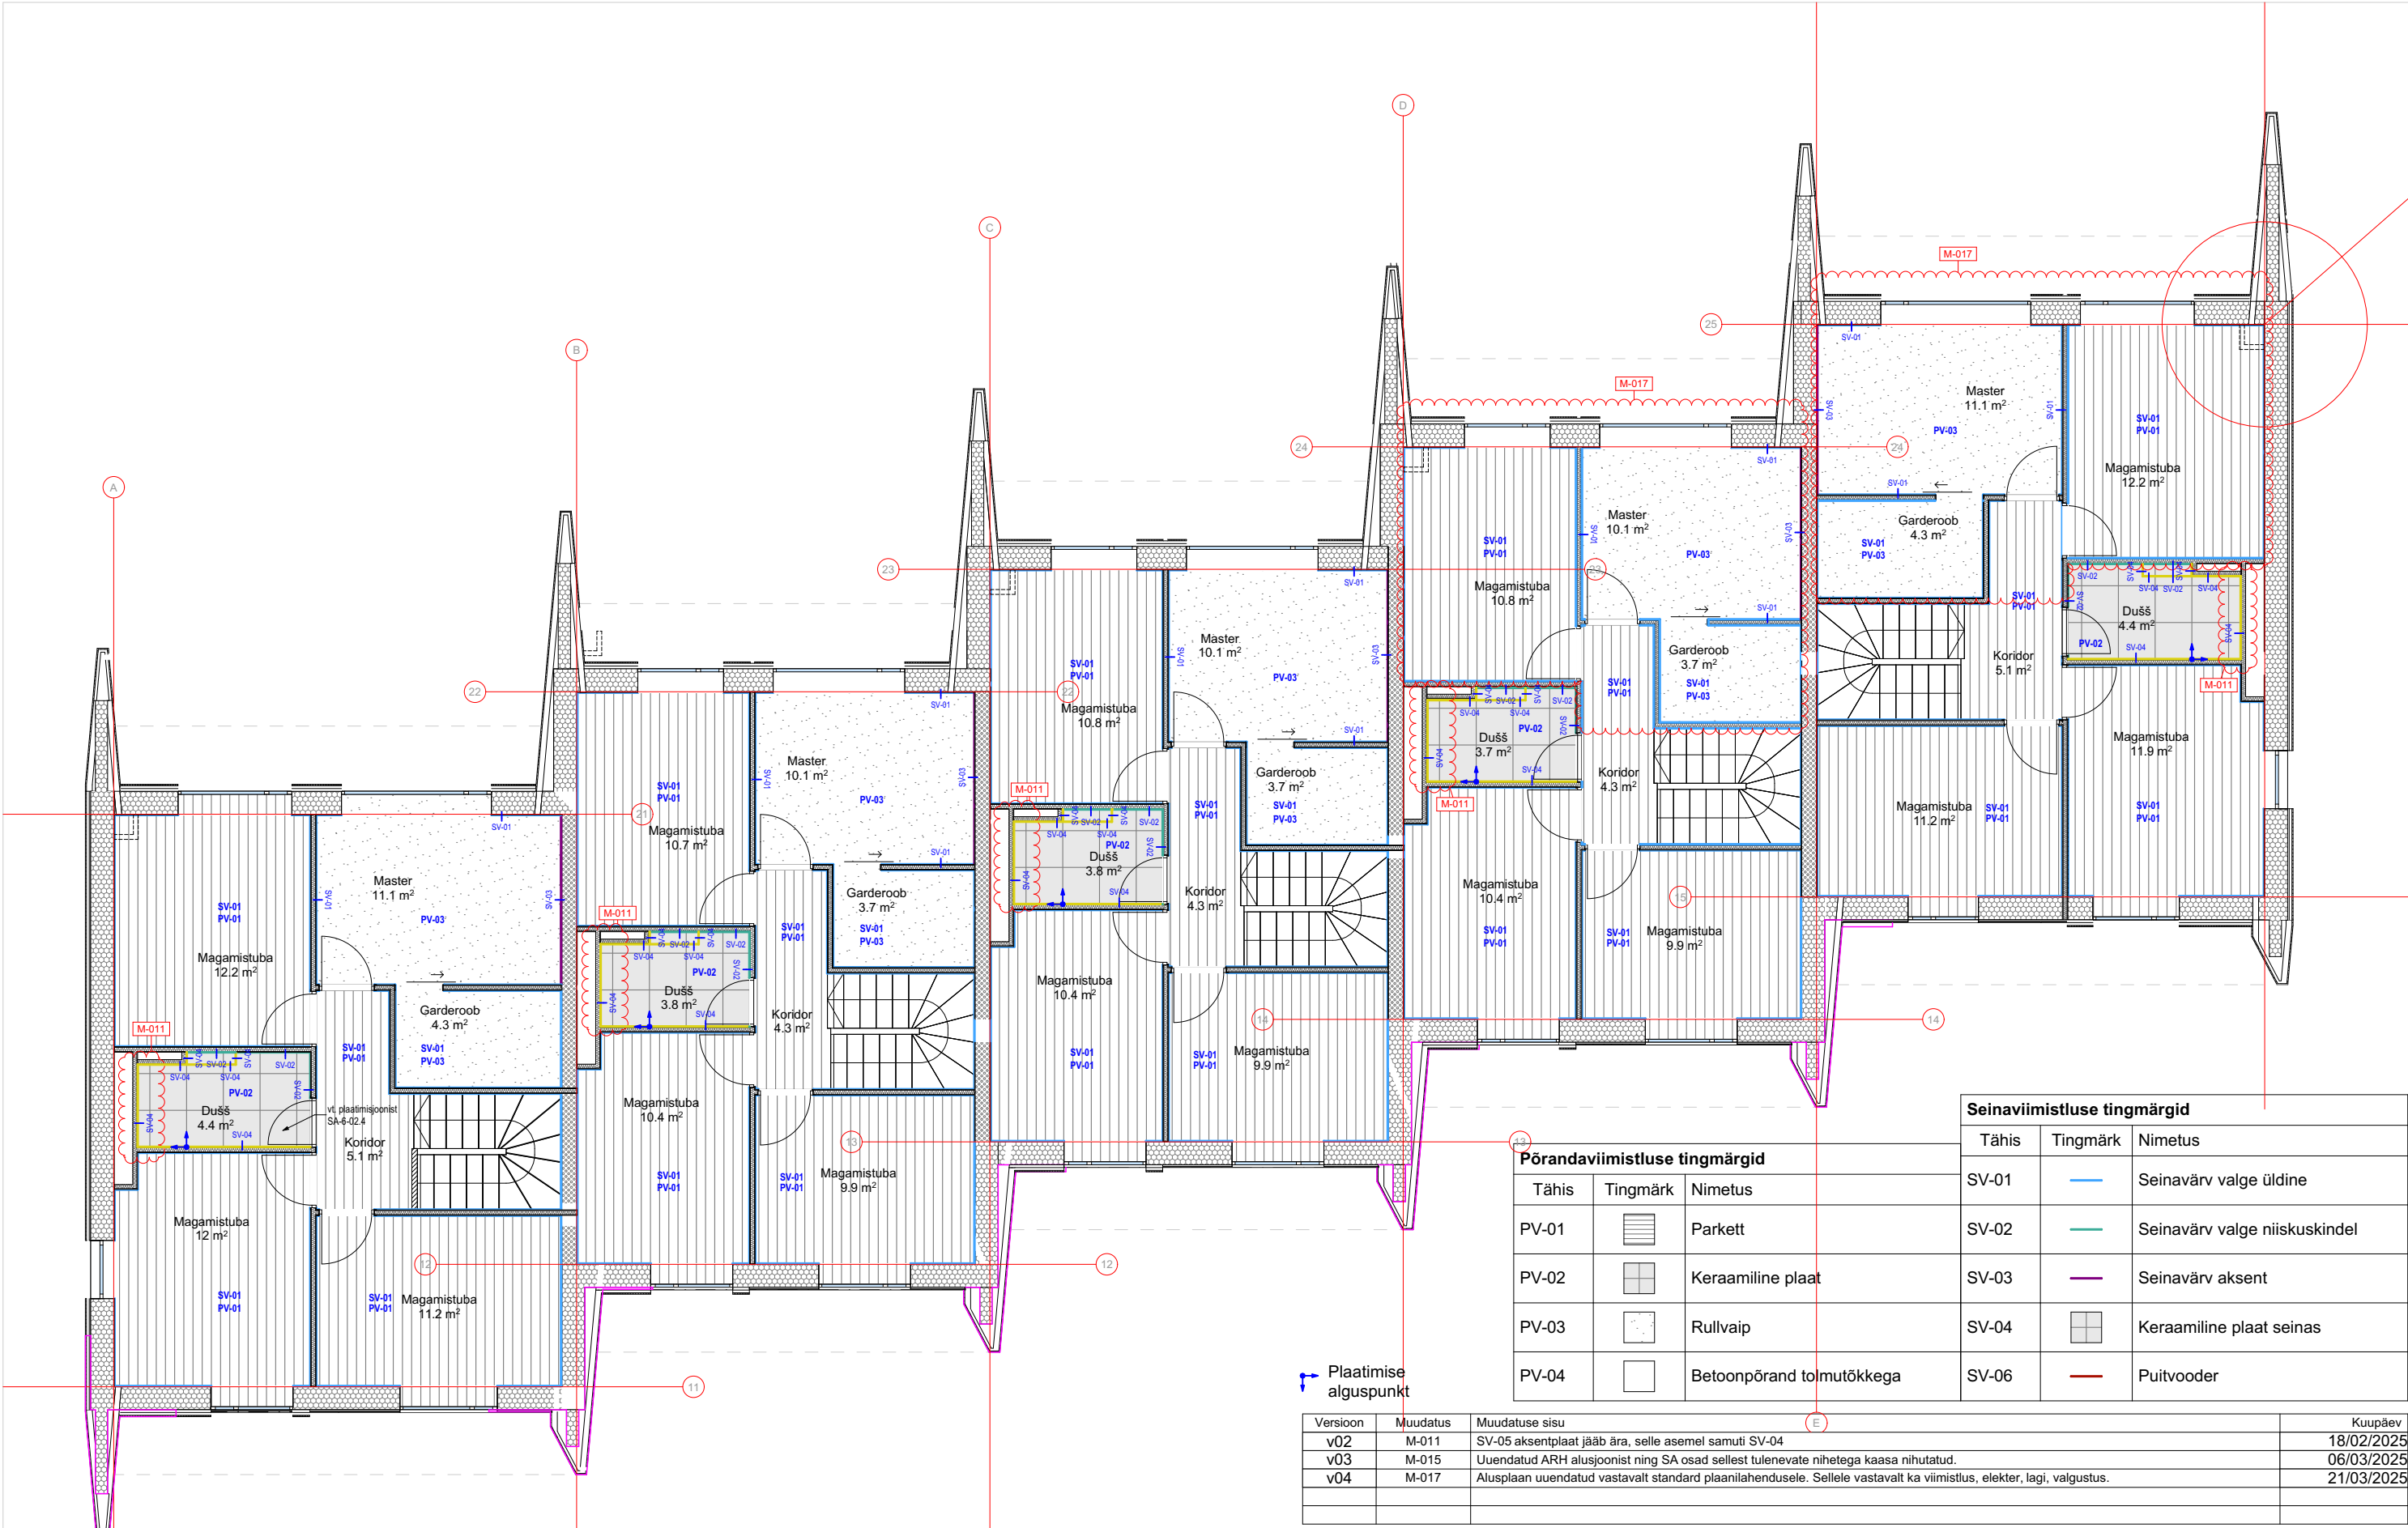

ÜLDMÄRKUSED:

- Käesolevat joonist käsitleda koos teiste projektiosadega. Vastuolude ilmnemisel võtta ühendust projekteerijaga.
- Kõikide materjalide ja ehitustööde kvaliteet peab vastama Eesti Vabariigis kehtivate seadusandlike aktide järgi kehtestatud nõuetele ja olema kooskõlas hea ehitustavaga.
- Kõik ehitusega seotud muudatused konstruktsioonide, mõõtude, materjalide, avatäidete, piirete, detailide jms. osas kooskõlastada kõigepealt projekteerijaga, seejärel tellijaga.
- Enne uste, akende, piirete, detailide ja muude sarnaste elementide valmistamist kontrollida eelnevalt avade ja karkassi tegelikud mõõtmed, avanemissuunad ja kogused.
- **Tootejoonised kooskõlastada enne valmistamist projekti sisearhitektiga.**
- **Kõik mõõdud tuleb kohapeal üle mõõta ja kontrollida reaalsel olukorda platsil. Vastuolude ilmnemisel võtta ühendust sisearhitektiga.**

Põrandaviimistluse tingmargid			Seinaviimistluse tingmargid		
Tähis	Tingmärk	Nimetus	Tähis	Tingmärk	Nimetus
SV-01		Seinavärv valge üldine	SV-01		Seinavärv valge üldine
PV-01		Parkett	SV-02		Seinavärv valge niiskuskindel
PV-02		Keraamiline plaat	SV-03		Seinavärv aksent
PV-03		Rullvaip	SV-04		Keraamiline plaat seinas
PV-04		Betoonpõrand tolmutõkkega	SV-06		Puitvooder

Version	Muudatus	Muudatuse sisu	Kuupäev
v02	M-011	SV-05 aksentplaat jääb ära, selle asemel samuti SV-04	18/02/2025
v03	M-015	Uuendatud ARH alusjoonist ning SA osad sellest tulenevate nihetega kaasa nihutatud.	06/03/2025
v04	M-017	Alusplaan uuendatud vastavalt standard plaanilahendusele. Sellele vastavalt ka viimistlus, elekter, lagi, valgustus.	21/03/2025

ARHITEKT

Objekt:

Saku Ridaelamu

Joonis:

2K siseviimistlusplaan

Projekteeris:

Tiiu Rull

Vastutav spetsialist:

Hannelore Kääramees

Arhitekt11 OÜ, reg nr 12190827; Joa 2/1, 10127 Tallinn, Eesti; info@arhitekt11.ee; KMKR EE101499183

Arhitekt11 OÜ, reg nr 12190827; Joa 2/1, 10127 Tallinn, Eesti; info@arhitekt11.ee; KMKR EE101499183

Address:

Kuu tee 16 Saku

Esm. väljaandmise kp:

17/01/2025

Mõõtkava:

1:100

Töö nr:

2024-11-01

Projekti juht:

Rita Ratušnaja

Kuupäev:

21/03/2025

Formaat:

A3

Staadium:

PP

Version:

v04

Arhitekt11 OÜ, reg nr 12190827; Joa 2/1, 10127 Tallinn, Eesti; info@arhitekt11.ee; KMKR EE101499183

Arhitekt11 OÜ, reg nr 12190827; Joa 2/1, 10127 Tallinn, Eesti; info@arhitekt11.ee; KMKR EE101499183

Joonise nr:
SA-5-02.2