


MÄRKUSED:

- Laeviimistlus vt. täpselt laeviimistluse spetsifikatsioonist.
- Valgustid vt. täpsemalt valgustite spetsifikatsioonist.
- Lülitid paigaldada kõrgusele H1.050, kui ei ole märgitud teisiti.
- Lülitite seeria PAKETT 1: Schneider, Merten System M, polaarvalge läikiv
- Lülitite seeria PAKETT 2: Schneider, Merten System M, antratsiit matt

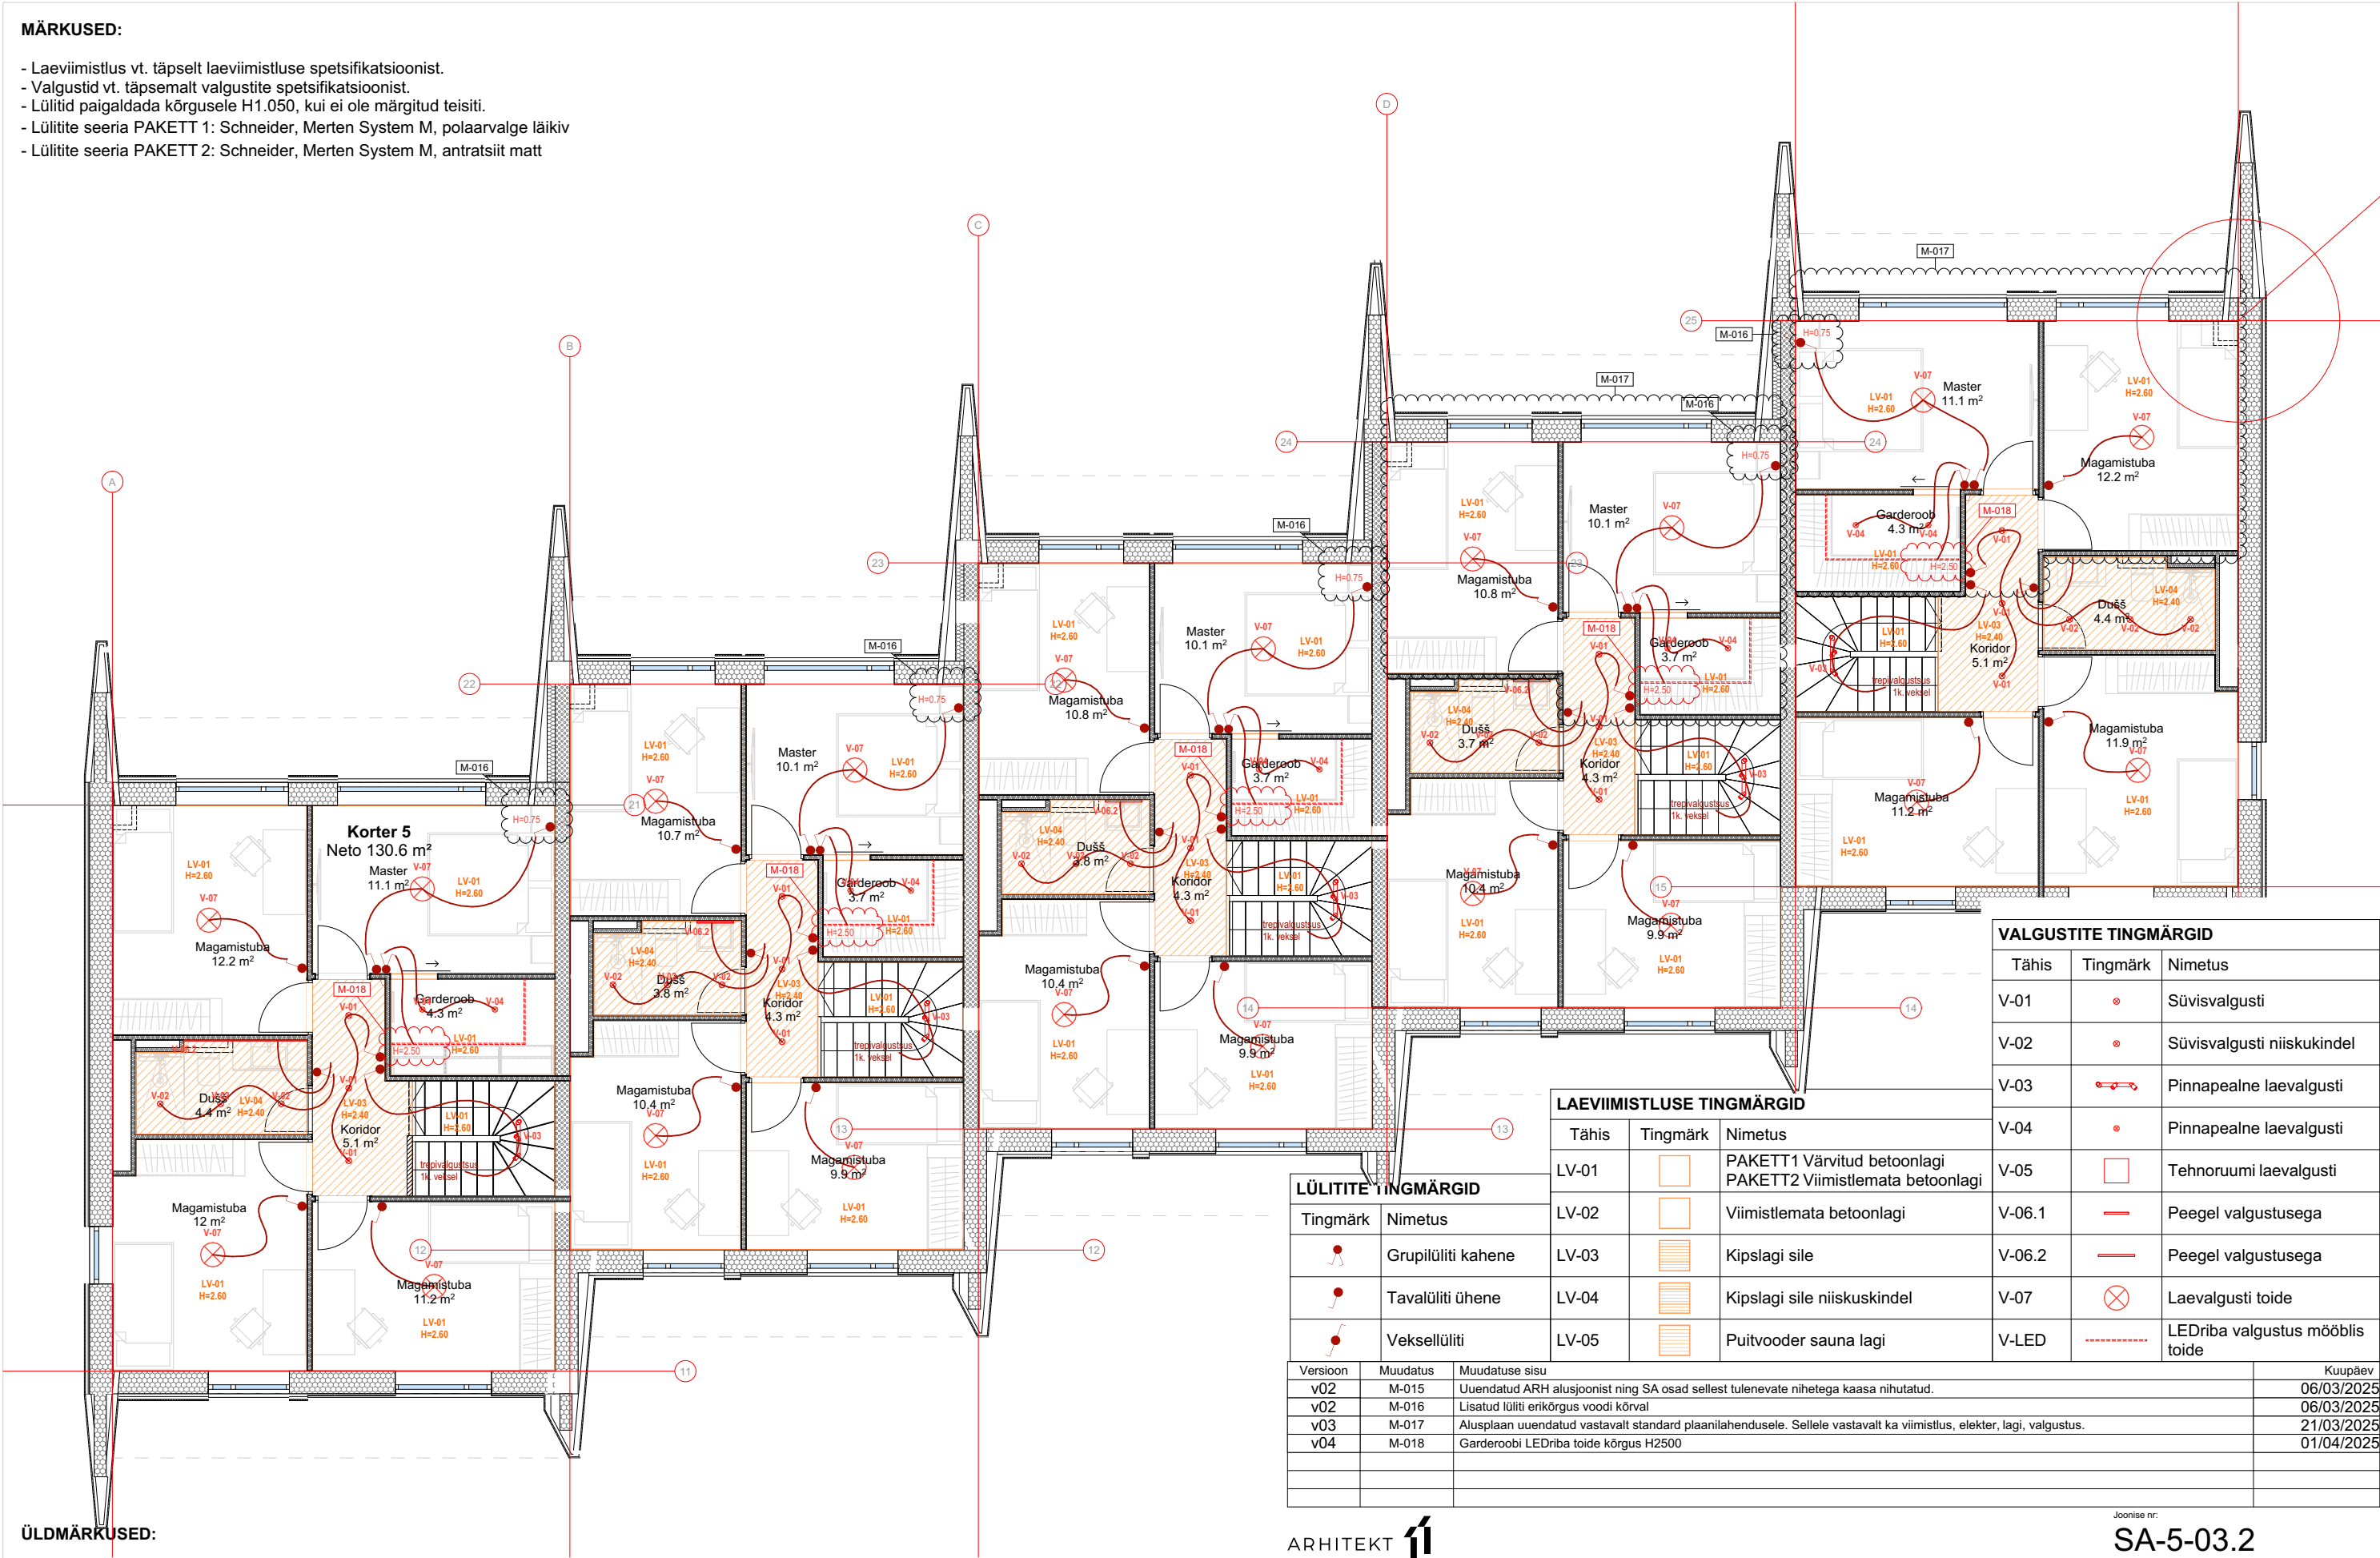

ARHITEKT

Saku Ridaelamu

Joonis:

2K lae- ja valgustusplaan

Projekteeris:

Tiiu Rull

Arhitekt11 OÜ, reg nr 12190827; Joa 2/1, 10127 Tallinn, Eesti; info@arhitekt11.ee; KMKR EE101499183

Vastutav spetsialist:

Hannelore Kääramees

Joonise nr:

SA-5-03.2

Esm. väljaandmise kp: 13/12/2024 Kuupäev: 01/04/2025 Versioon: v04

Mõõkava: 1:100 Formaati: A3 Staadium: PP

Töö nr: 2024-11-01

Projekti juht: Rita Ratušnaja

+372 512 4858; rita.ratushnaja@arhitekt11.ee