


MÄRKUSED:

- Pistikud paigaldada põrandast kõrgusele H0.200, kui ei ole märgitud teisiti.
- Pistikute seeria PAKETT 1: Schneider, Merten System M, polaarvalge läikiv
- Pistikute seeria PAKETT 2: Schneider, Merten System M, antratsiit matt

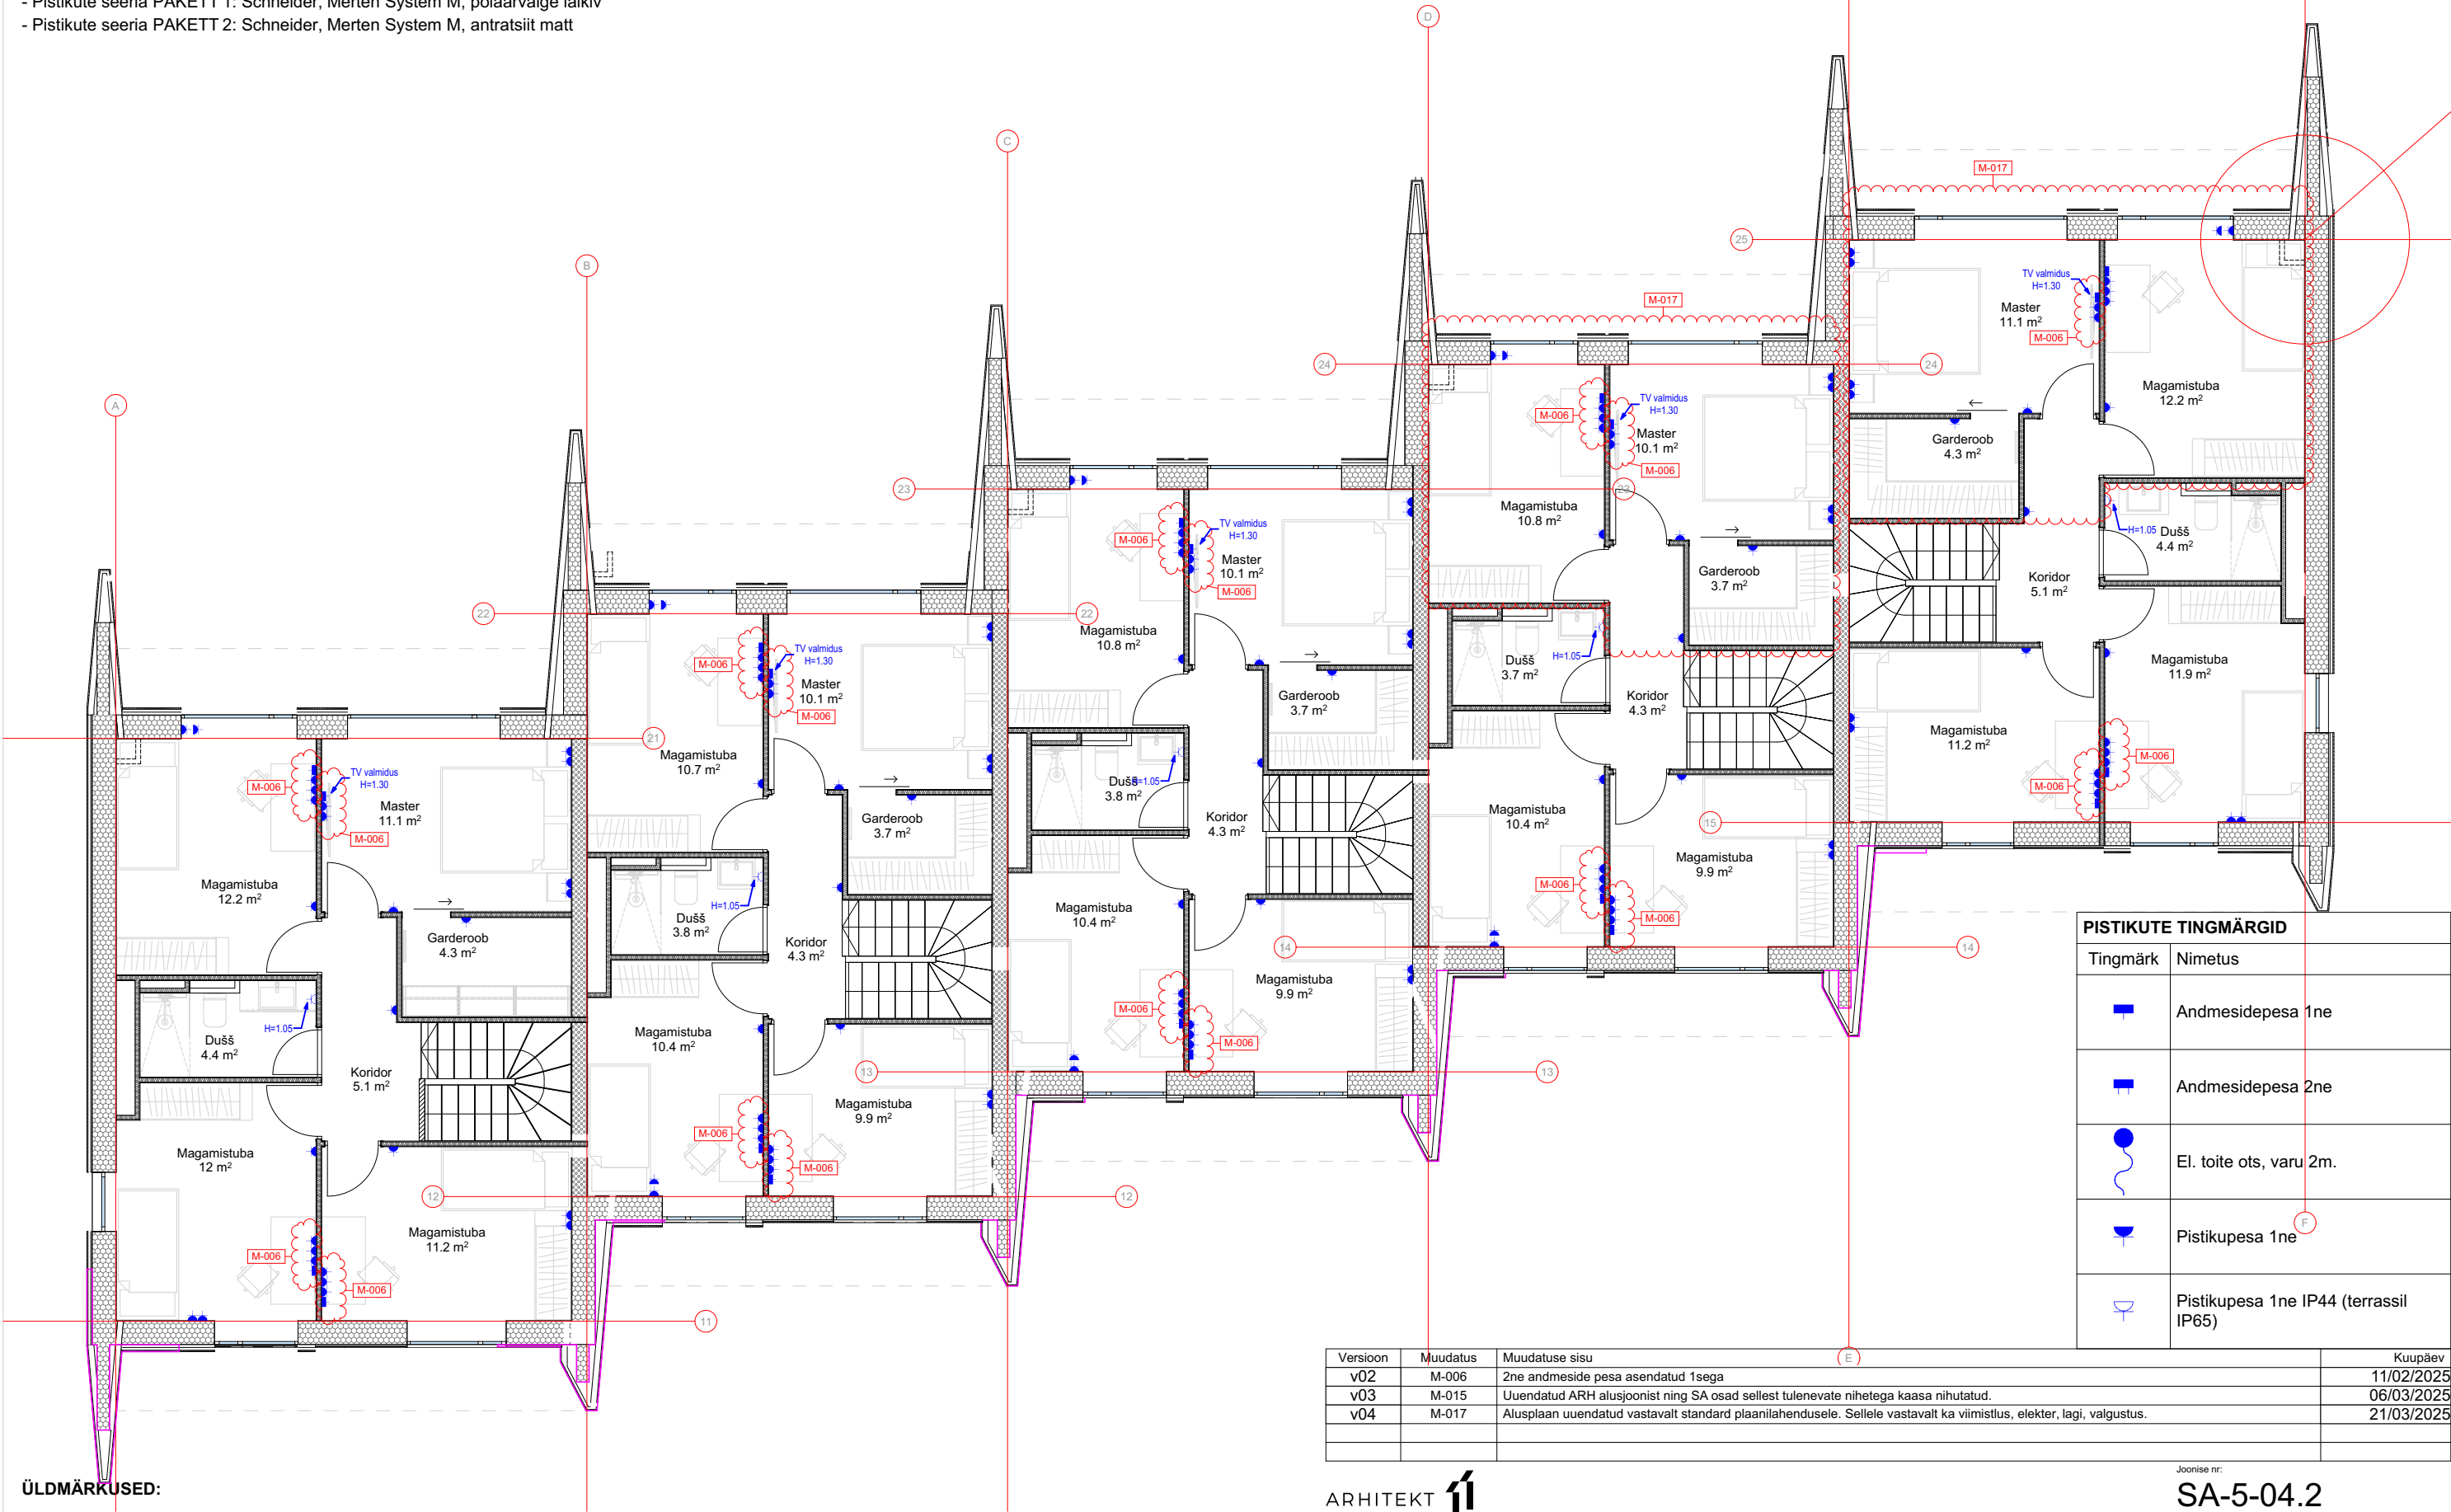

ÜLDMÄRKUSED:

- Käesolevat joonist käsitleda koos teiste projektiosadega. Vastuolude ilmnemisel võtta ühendust projekteerijaga.
- Kõikide materjalide ja ehitustööde kvaliteet peab vastama Eesti Vabariigis kehtivate seadusandlike aktide järgi kehtestatud nõuetele ja olema kooskõlas hea ehitustavaga.
- Kõik ehitusega seotud muudatused konstruktsioonide, mõõtude, materjalide, avatäidete, piirete, detailide jms. osas kooskõlastada kõigepealt projekteerijaga, seejärel tellijaga.
- Enne uste, akende, piirete, detailide ja muude sarnaste elementide valmistamist kontrollida eelnevalt avade ja karkassi tegelikud mõõtmed, avanemissuunad ja kogused.
- **Tootejoonised kooskõlastada enne valmistamist projekti sisearhitektiga.**
- **Kõik mõõdud tuleb kohapeal üle mõõta ja kontrollida reaalsel olukorda platsil. Vastuolude ilmnemisel võtta ühendust sisearhitektiga.**

Version	Muudatus	Muudatuse sisu	Kuupäev
v02	M-006	2ne andmeside pesa asendatud 1sega	11/02/2025
v03	M-015	Uuendatud ARH alusjoonist ning SA osad sellest tulenevate nihetega kaasa nihutatud.	06/03/2025
v04	M-017	Alusplaan uuendatud vastavalt standard plaanilahendusele. Sellele vastavalt ka viimistlus, elekter, lagi, valgustus.	21/03/2025

ARHITEKT

Objekt:
Saku Ridaelamu

Joonis:

Projekteeris:
Tiiu Rull

Arhitekt11 OÜ, reg nr 12190827; Joa 2/1, 10127 Tallinn, Eesti; info@arhitekt11.ee; KMKR EE101499183

Address:
Kuu tee 16 Saku

Vastutav spetsialist:
Hannelore Kääramees

Joonise nr:
SA-5-04.2

Esm. väljaandmise kp:
13/12/2024

Mõõtkava:
1:100

Töö nr:
2024-11-01

Projektijuht:
Rita Ratušnaja

Kuupäev:
21/03/2025

Formaat:
A3

Version:
v04

Stadium:
PP

+372 512 4858; rita.ratushnaja@arhitekt11.ee