




TREPI LÕIGE 1

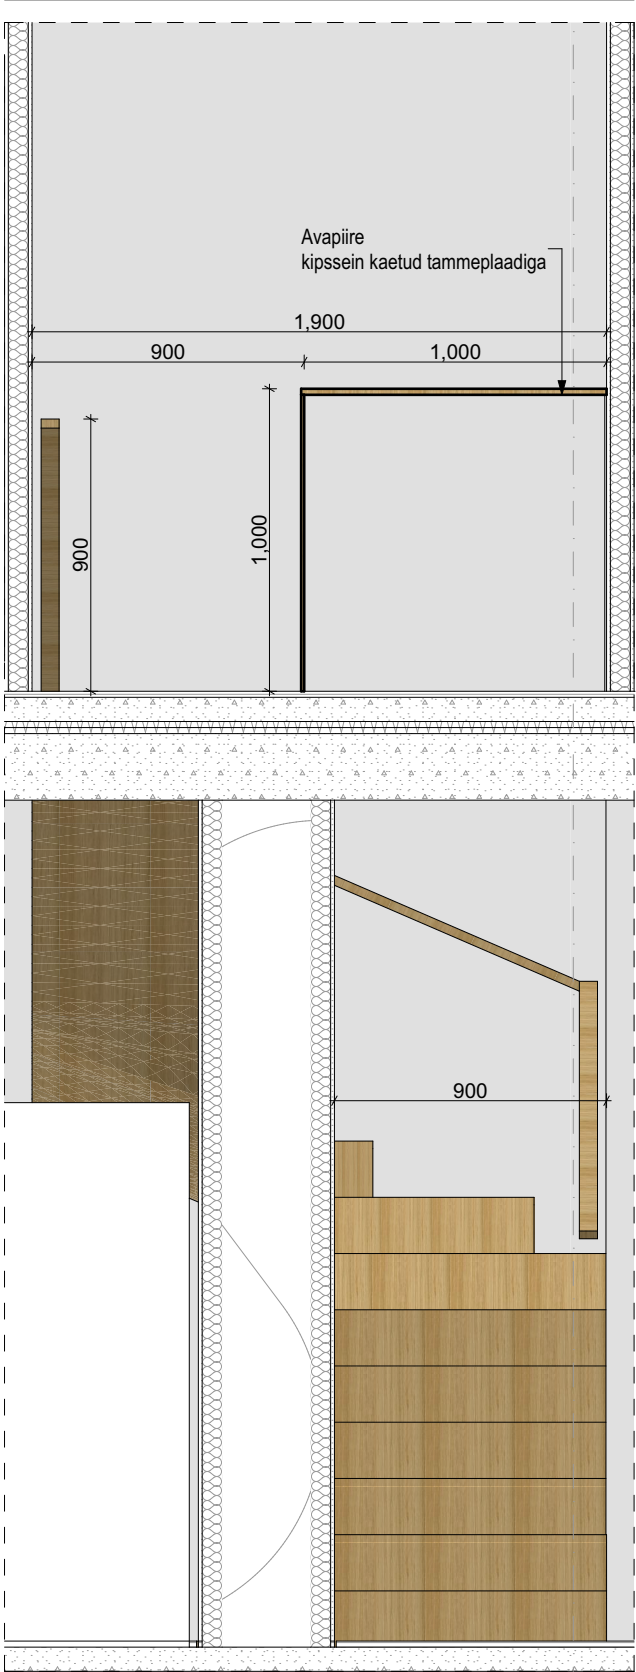


TREPI LÕIGE 2

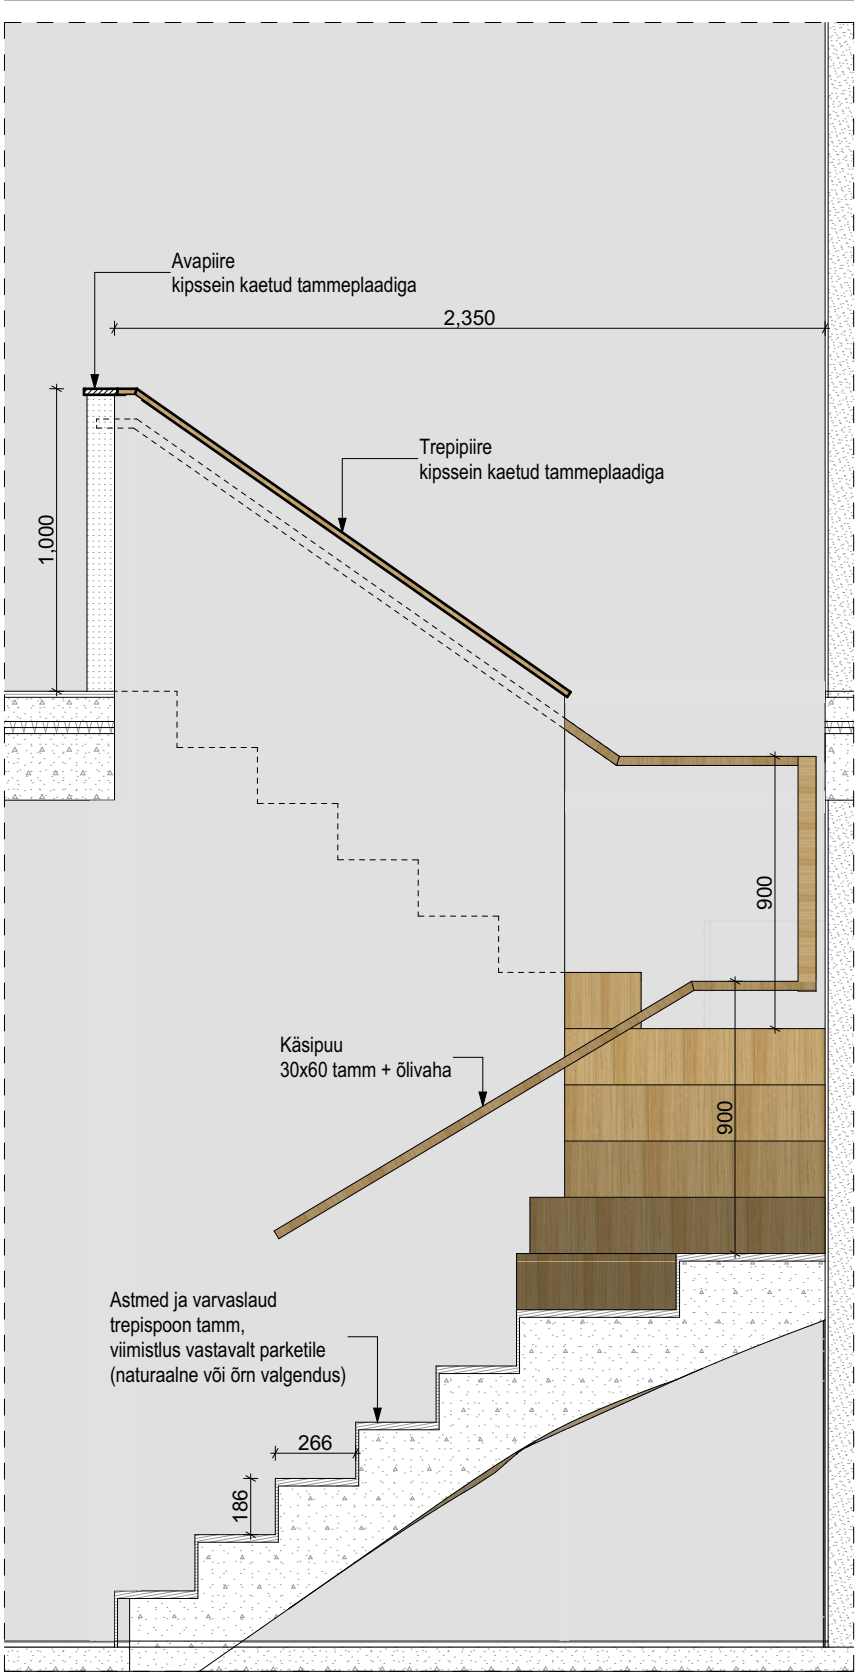

PEALTVAADE 1k

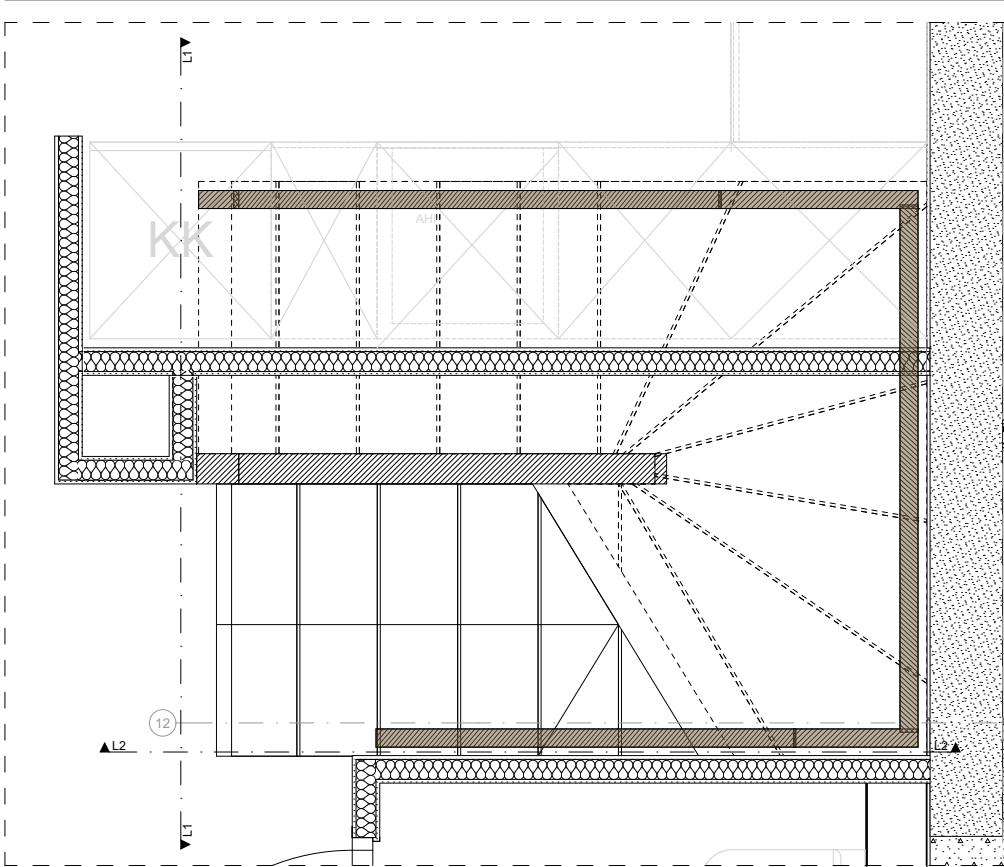

PEALTVAADE 2k

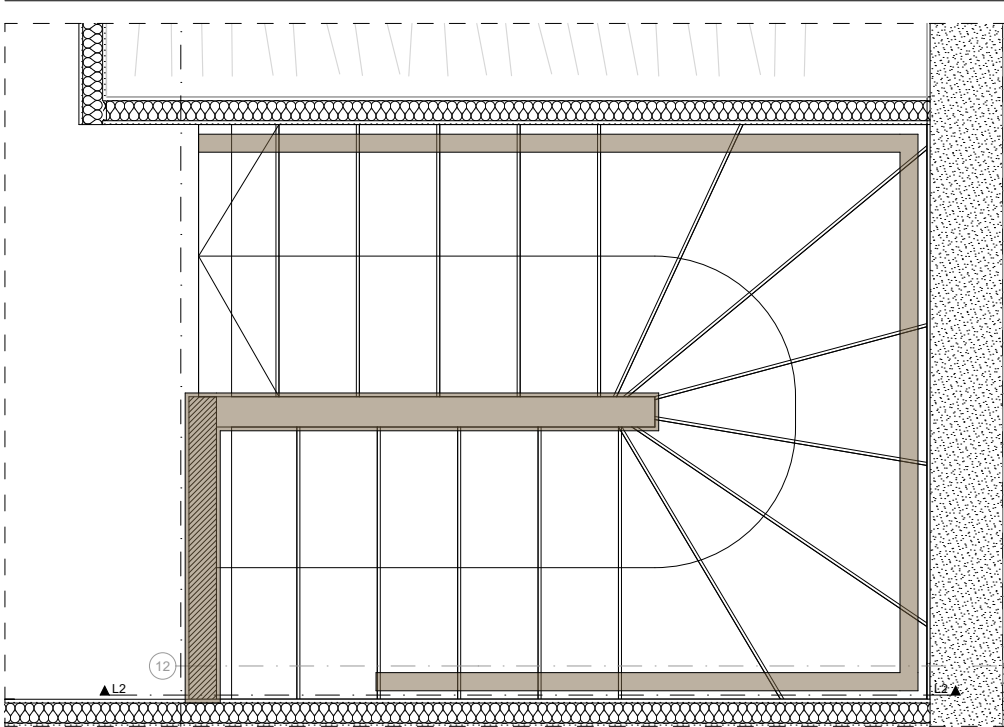

TÄPSE TEOSTUSJONISE PROJEKTEERIB TOOTJA.

Versioon	Muudatus	Muudatuse sisu	Kuupäev

ARHITEKT

Objekt:

Saku Ridaelamu

Joonis:

Trepipiire ja kasipuu

Projekteeris:

Tiiu Rull

Arhitekt11 OÜ, reg nr 12190827; Joa 2/1, 10127 Tallinn, Eesti; info@arhitekt11.ee; KMKR EE101499183

Address:

Kuu tee 16 Saku

Eem. väljaandmise kp:

17/01/2025

Mõõkava:

1:25

Töö nr:

2024-11-01

Projekti juht:

Rita Ratušnaja

Vastutav spetsialist:

Hannelore Kääramees

Arhitekt11 OÜ, reg nr 12190827; Joa 2/1, 10127 Tallinn, Eesti; info@arhitekt11.ee; KMKR EE101499183

Joonise nr:

SA-6-01.1

Eem. väljaandmise kp:

17/01/2025

Mõõkava:

1:25

Töö nr:

2024-11-01

Projekti juht:

Rita Ratušnaja

Vastutav spetsialist:

Hannelore Kääramees

Arhitekt11 OÜ, reg nr 12190827; Joa 2/1, 10127 Tallinn, Eesti; info@arhitekt11.ee; KMKR EE101499183

Kuupäev:

Versioon:

v01

Stadium:

PP

Arhitekt11 OÜ, reg nr 12190827; Joa 2/1, 10127 Tallinn, Eesti; info@arhitekt11.ee; KMKR EE101499183

ÜLDMÄRKUSED:

- Käesolevat joonist käsitleda koos teiste projektiosadega. Vastuolude ilmnemisel võtta ühendust projekteerijaga.
- Kõikide materjalide ja ehitustööde kvaliteet peab vastama Eesti Vabariigis kehtivate seadusandlike aktide järgi kehtestatud nõuetele ja olema kooskõlas hea ehitustavaga.
- Kõik ehitusega seotud muudatused konstruktsioonide, mõõtude, materjalide, avatäidete, piirete, detailide jms. osas kooskõlastada kõigepealt projekteerijaga, seejärel tellijaga.
- Enne uste, akende, piirete, detailide ja muude sarnaste elementide valmistamist kontrollida eelnevalt avade ja karkassi tegelikud mõõtmed, avanemissuunad ja kogused.
- **Tootejoonised kooskõlastada enne valmistamist projekti sisearhitektiga.**
- **Kõik mõõdud tuleb kohapeal üle mõõta ja kontrollida reaalsel olukorda platsil. Vastuolude ilmnemisel võtta ühendust sisearhitektiga.**