


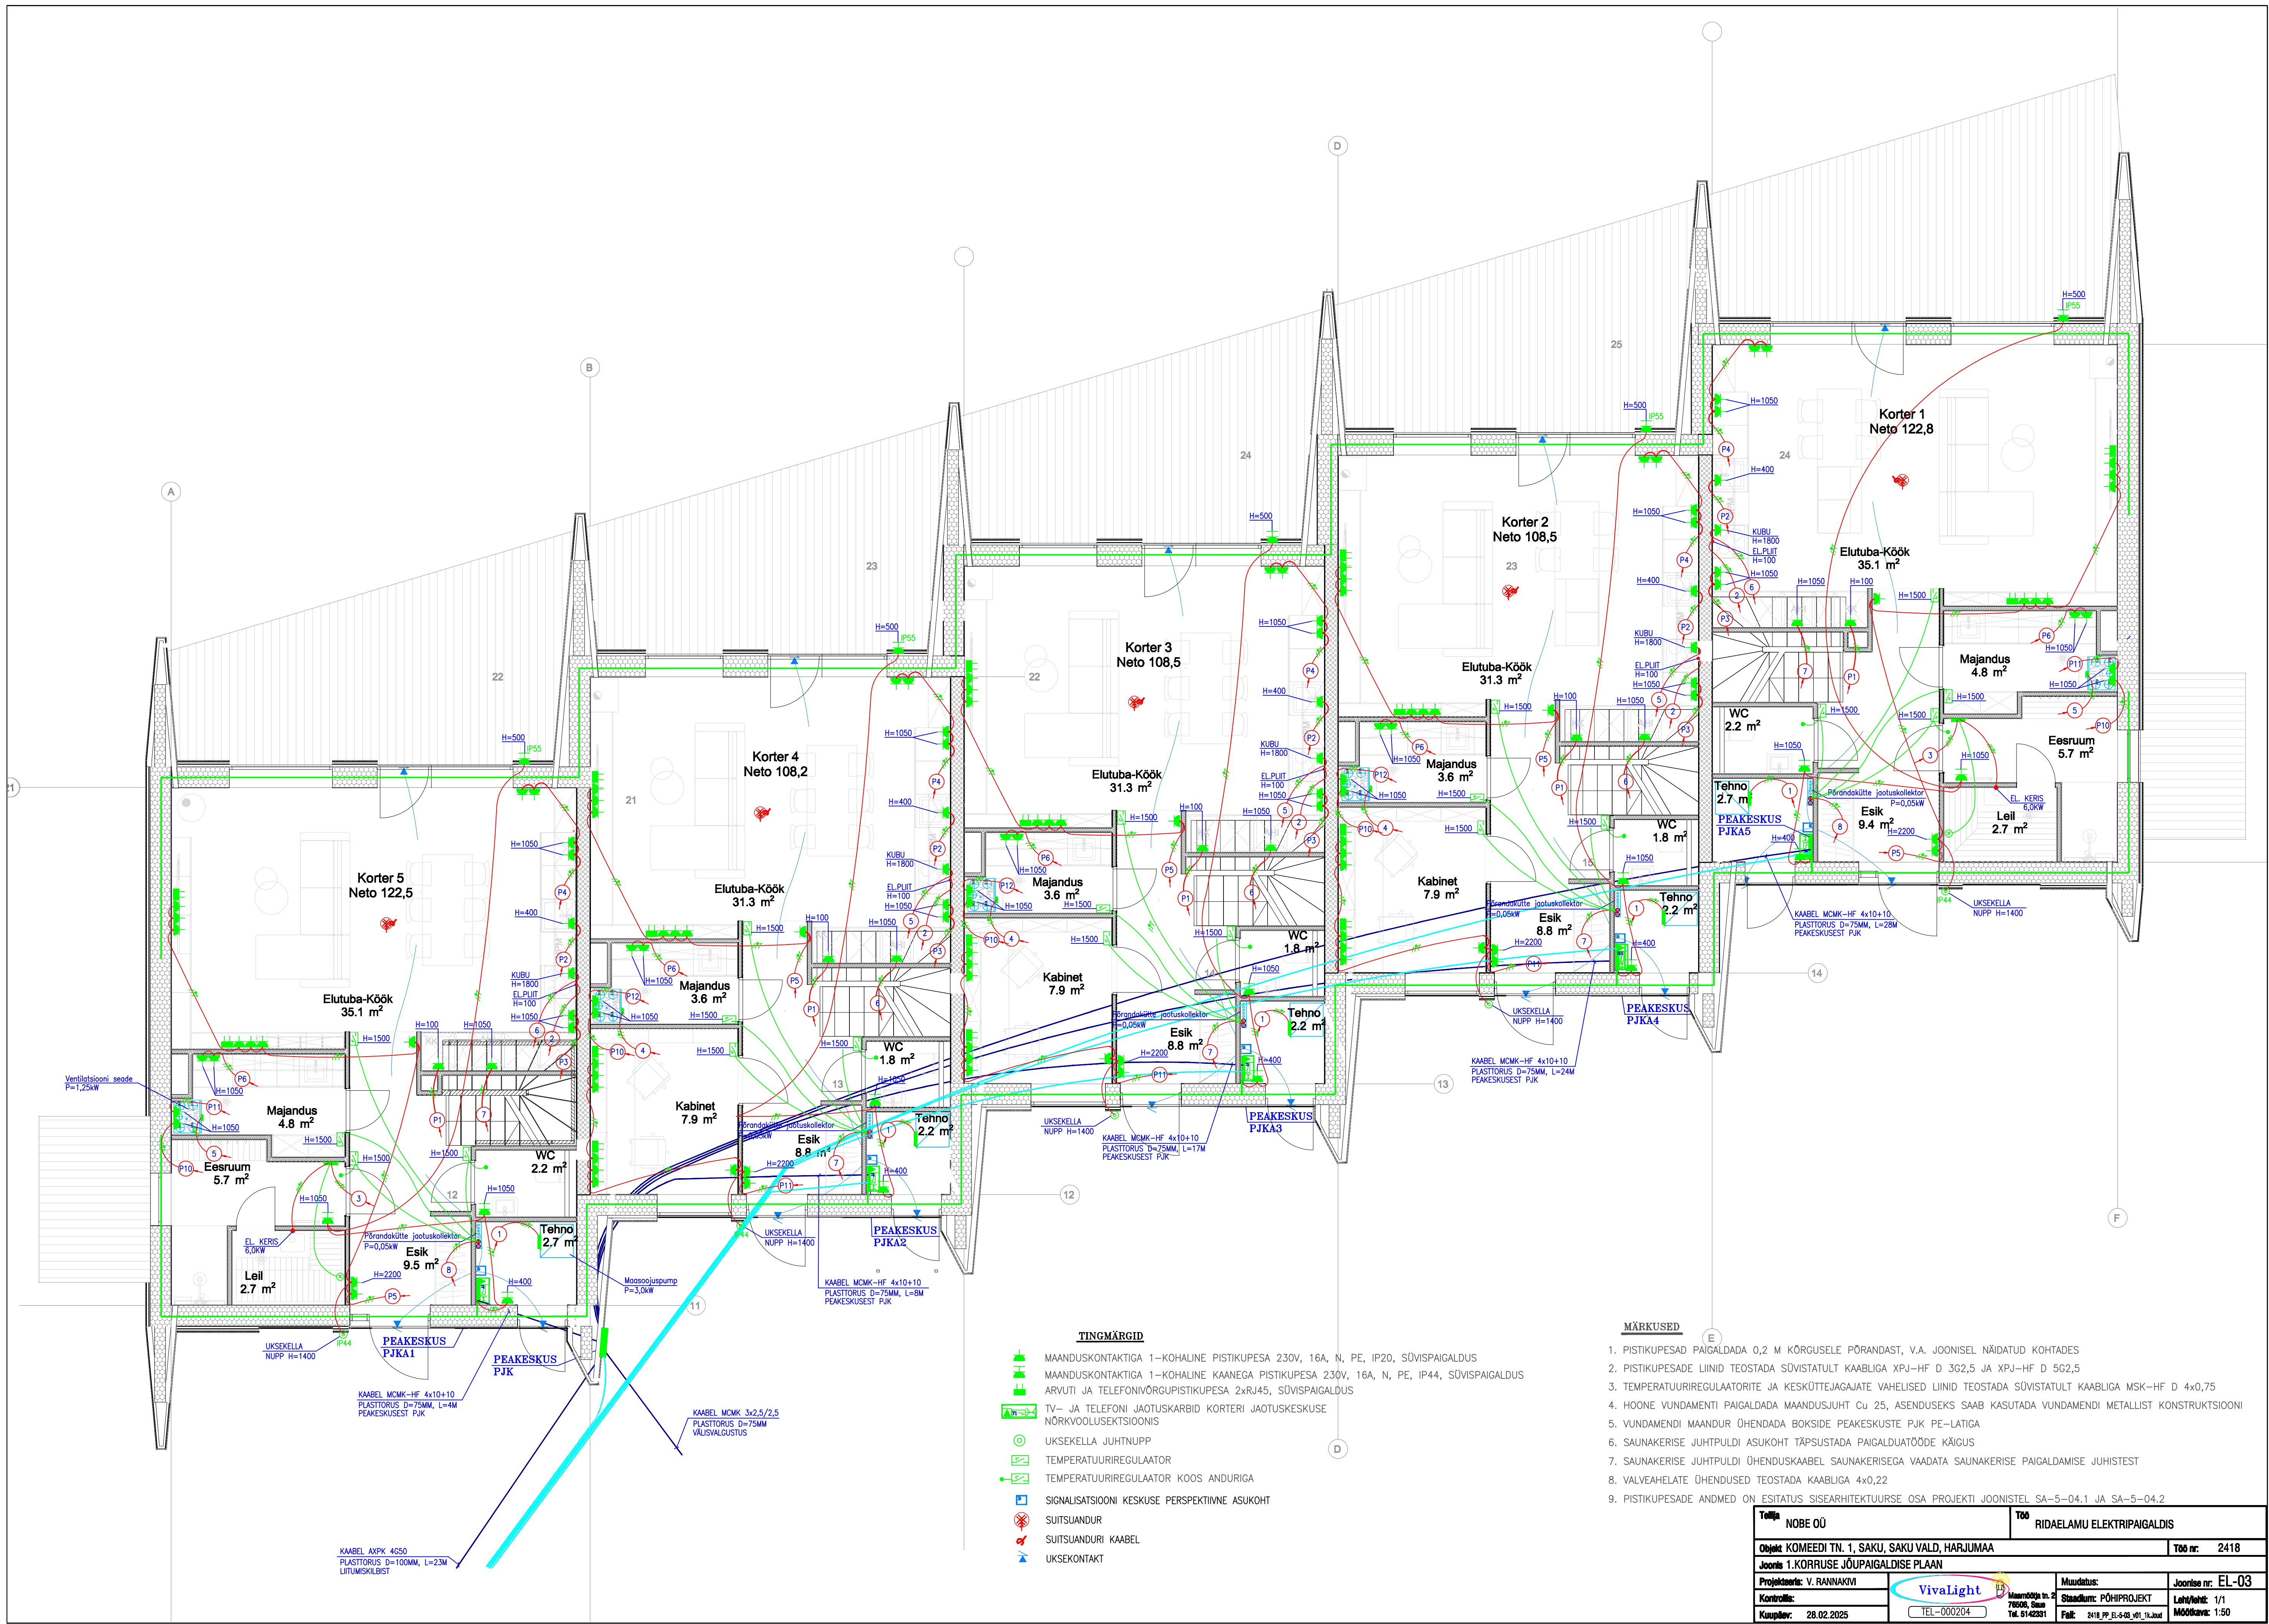

- TINGMÄRGID**
- MAANDUSKONTAKTIGA 1—KOHALINE PISTIKUPESA 230V, 16A, N, PE, IP20, SÜVISPAGALDUS
 - MAANDUSKONTAKTIGA 1—KOHALINE KANAEVA PISTIKUPESA 230V, 16A, N, PE, IP44, SÜVISPAGALDUS
 - ARVUTI JA TELEFONIVÕRGUPISTIKUPESA 2xRJ45, SÜVISPAGALDUS
 - TV- JA TELEFONI JAOTUSKARPID KORTERI JAOTUSKESKUSE NÕRKVÕLUSEKTSIOONIS
 - UKSEKELLA JUHTNUPP
 - TEMPERATUURIREGULAATOR
 - TEMPERATUURIREGULAATOR KOOS ANDURIGA
 - SIGNALISATSIOONI KESKUSE PERSPEKTIVNE ASUKOHT
 - SUITSUANDUR
 - SUITSUANDURI KABEL
 - UKSEKONTAKT

- MÄRKUSED**
- PISTIKUPESAD PAIGALDADA 0,2 M KÕRGUSELE PÖRANDAST, V.A. JOONISEL NÄIDATUD KOHTADES
 - PISTIKUPESADE LIINID TEOSTADA SÜVISTATULT KAABLIGA XPJ—HF D 3G2,5 JA XPJ—HF D 5G2,5
 - TEMPERATUURIREGULAATORITE JA KESKÜTEJAGAJATE VAHELISED LIINID TEOSTADA SÜVISTATULT KAABLIGA MSK—HF D 4x0,75
 - HOONE VUNDAMENTI PAIGALDADA MAANDUSJUHT Cu 25, ASENDUSEKS SAAB KASUTADA VUNDAMENTI METALLIST KONSTRUKTSIOONI
 - VUNDAMENTI MAANDUR ÜHENDADA BOKSIDE PEAKESKUSTE PJK PE—LATIGA
 - SAUNAKERISE JUHTPULDI ASUKOHT TÄPSUSTADA PAIGALDUATÕDE KÄIGUS
 - SAUNAKERISE JUHTPULDI ÜHENDUSKABEL SAUNAKERISEGA VAADATA SAUNAKERISE PAIGALDAMISE JUHISTEST
 - VALVEAHELATE ÜHENDUSED TEOSTADA KAABLIGA 4x0,22
 - PISTIKUPESADE ANDMED ON ESITATUD SISEARHITEKTUURSE OSA PROJEKTI JOONISTEL SA—5—04.1 JA SA—5—04.2

Töökoht NOBE OÜ		Töö RIDAELAMU ELEKTRIPAIGALDIS	
Objekt KOMEEDI TN. 1, SAKU, SAKU VALD, HARJUMAA		Töö nr: 2418	
Joonis 1.KORRUSE JÕUPAIGALDISE PLAAN			
Projekteerin V. RANNAKIVI	 Määratud in 76066, Sane Tel: 6142381	Muudatus:	Joonis nr: EL-03
Kontrollin:		Staudium: PÕHIPROJEKT	Leht/nr: 1/1
Kuupäev: 28.02.2025	Tel: 000204	Faht: 2418_PP_EL-03_v01_11.dwg	Mõõtkava: 1:50