


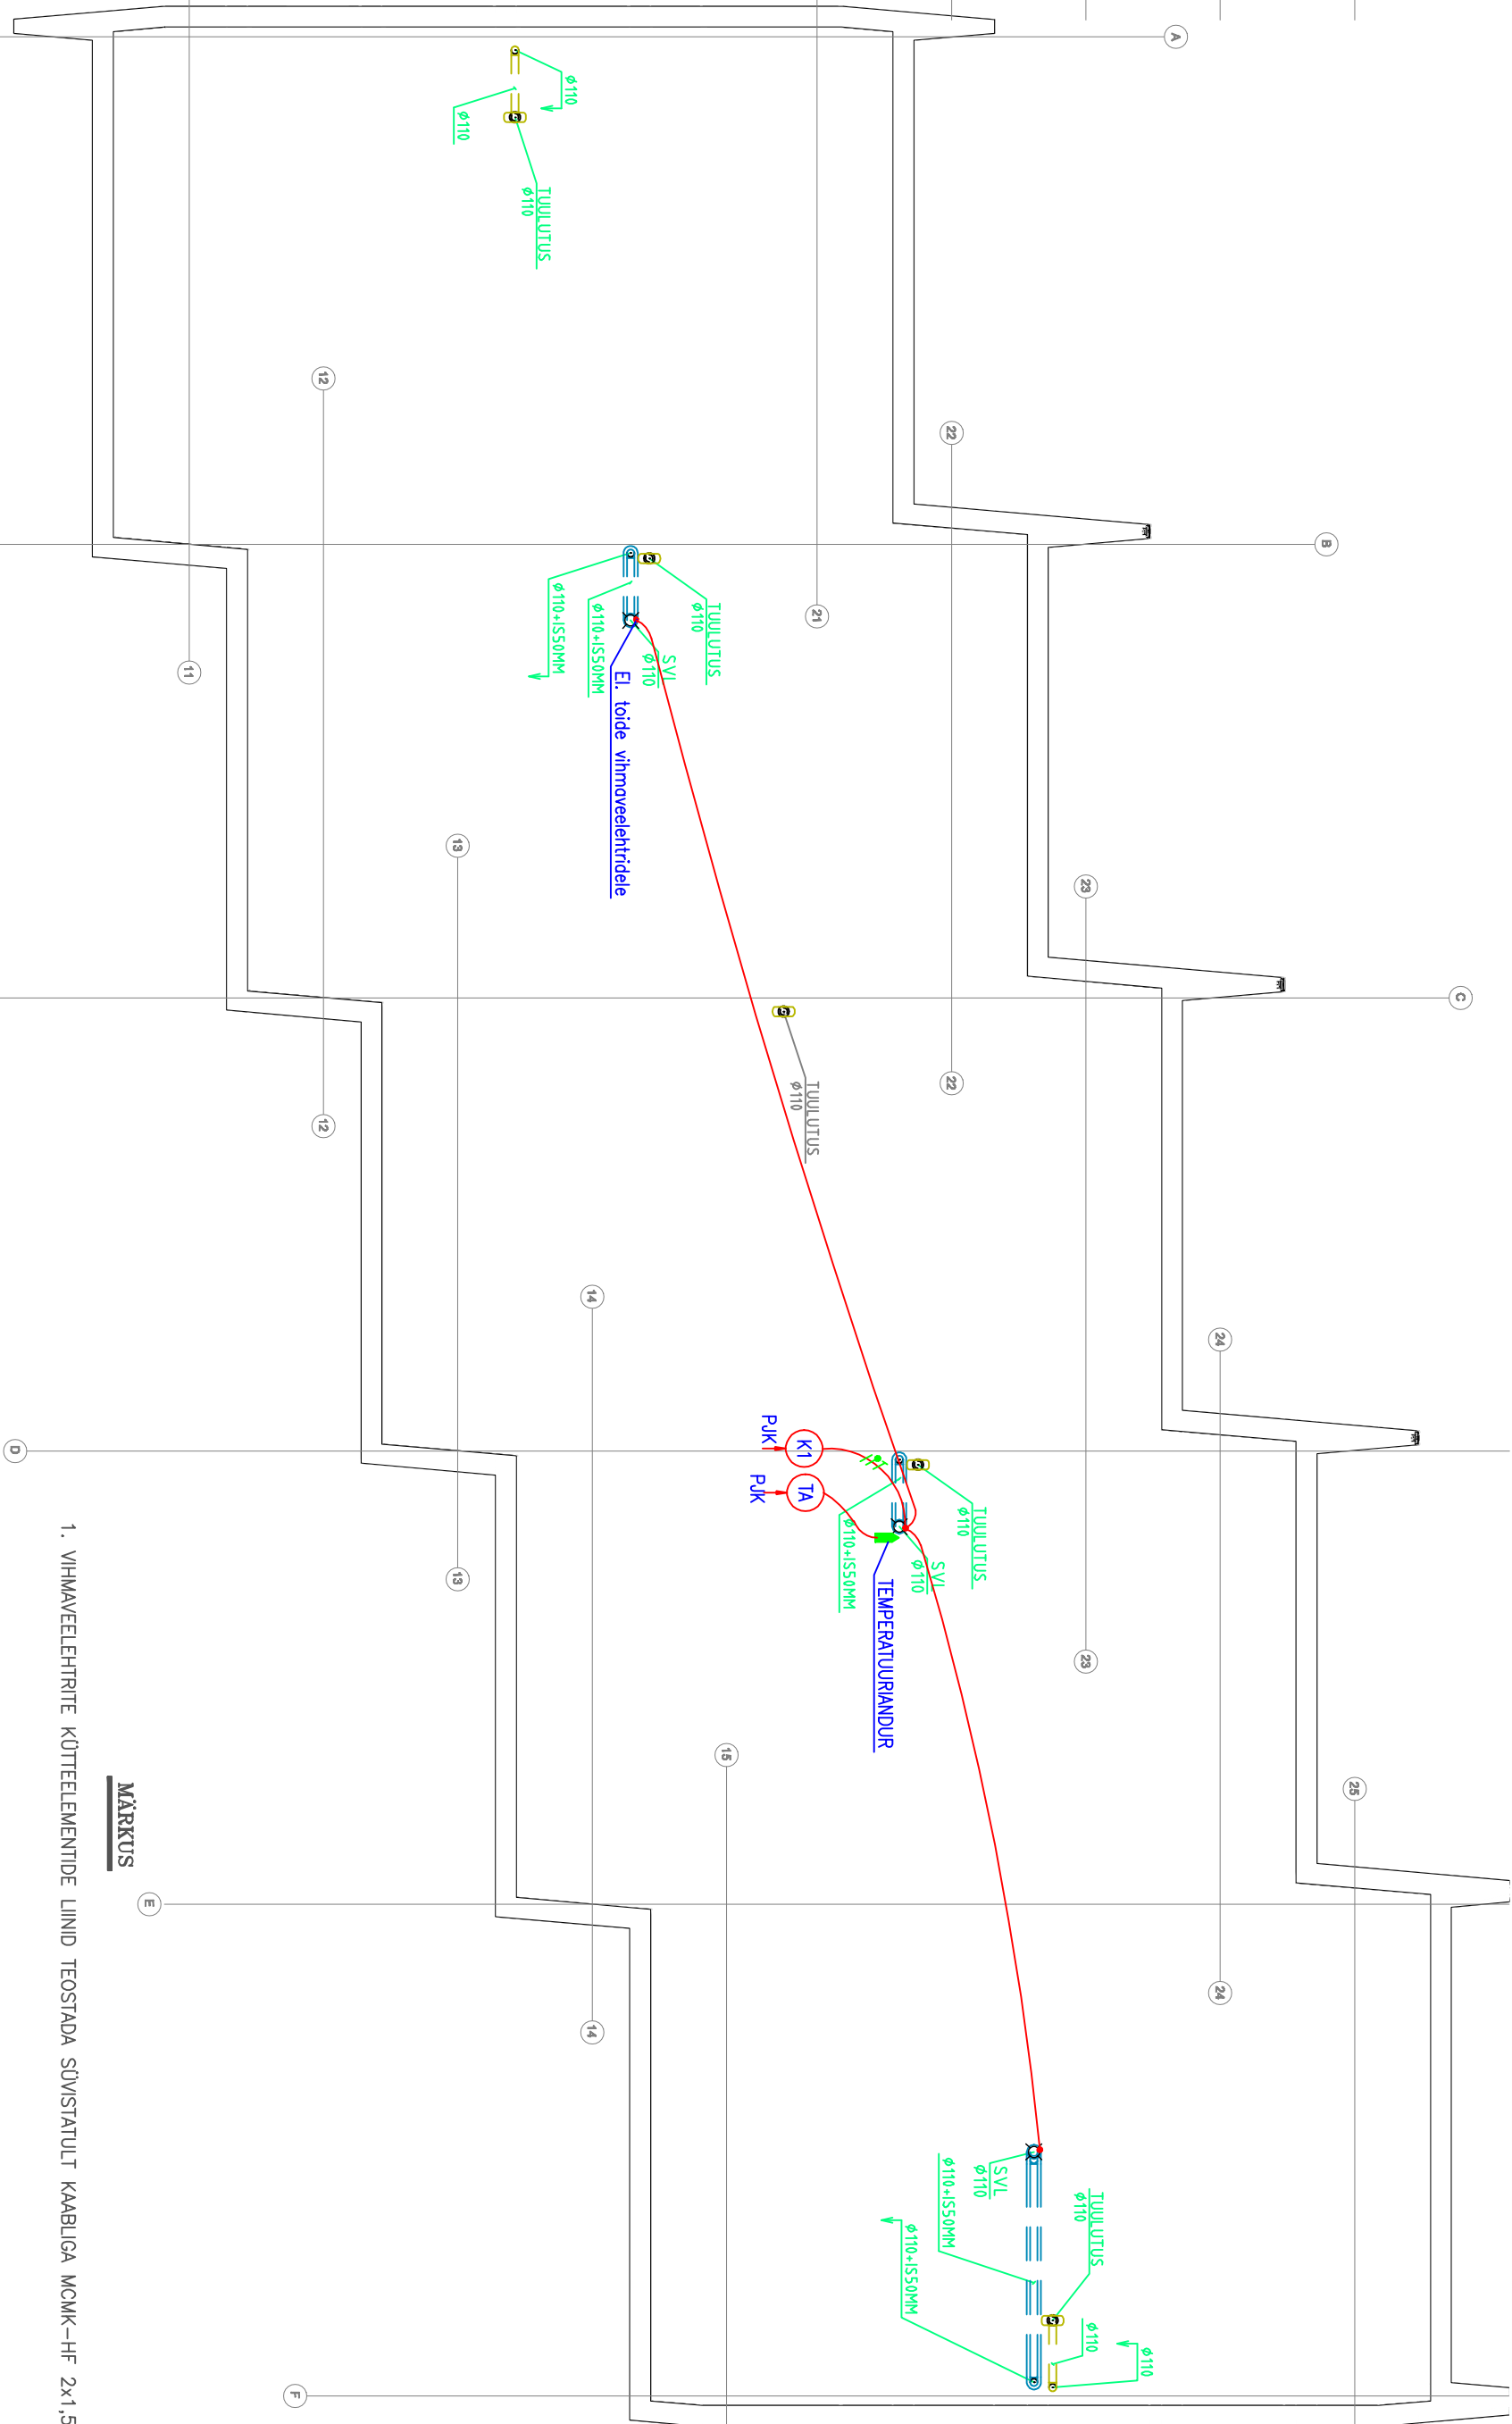

Tellijä NOBE OÜ		Töö RIIÐAELAMU ELEKTRIPAIGALDIS	
Objekt KOMEEDI TN. 1, SAKU, SAKU VALD, HARJUMAA		Töö nr. 2418	
Joonis KATUSE ELEKTRIPAIGALDISE PLAAN			
Projekteeris: V. RANNAKIVI		Muudatus:	
Kontrollis:		Staadium: PÕHIPROJEKT	
Kujutatud: 28.02.2025		Lõpetamise: 1/1	
		Mõõtkava: 1:50	

Tel. 000204

Maandaja tn. 2
76506, Saue
Tel. 5142351

Muudatus:

Staadium: PÕHIPROJEKT

Joonise nr. EL-05

Lõpetamise: 1/1

Mõõtkava: 1:50