


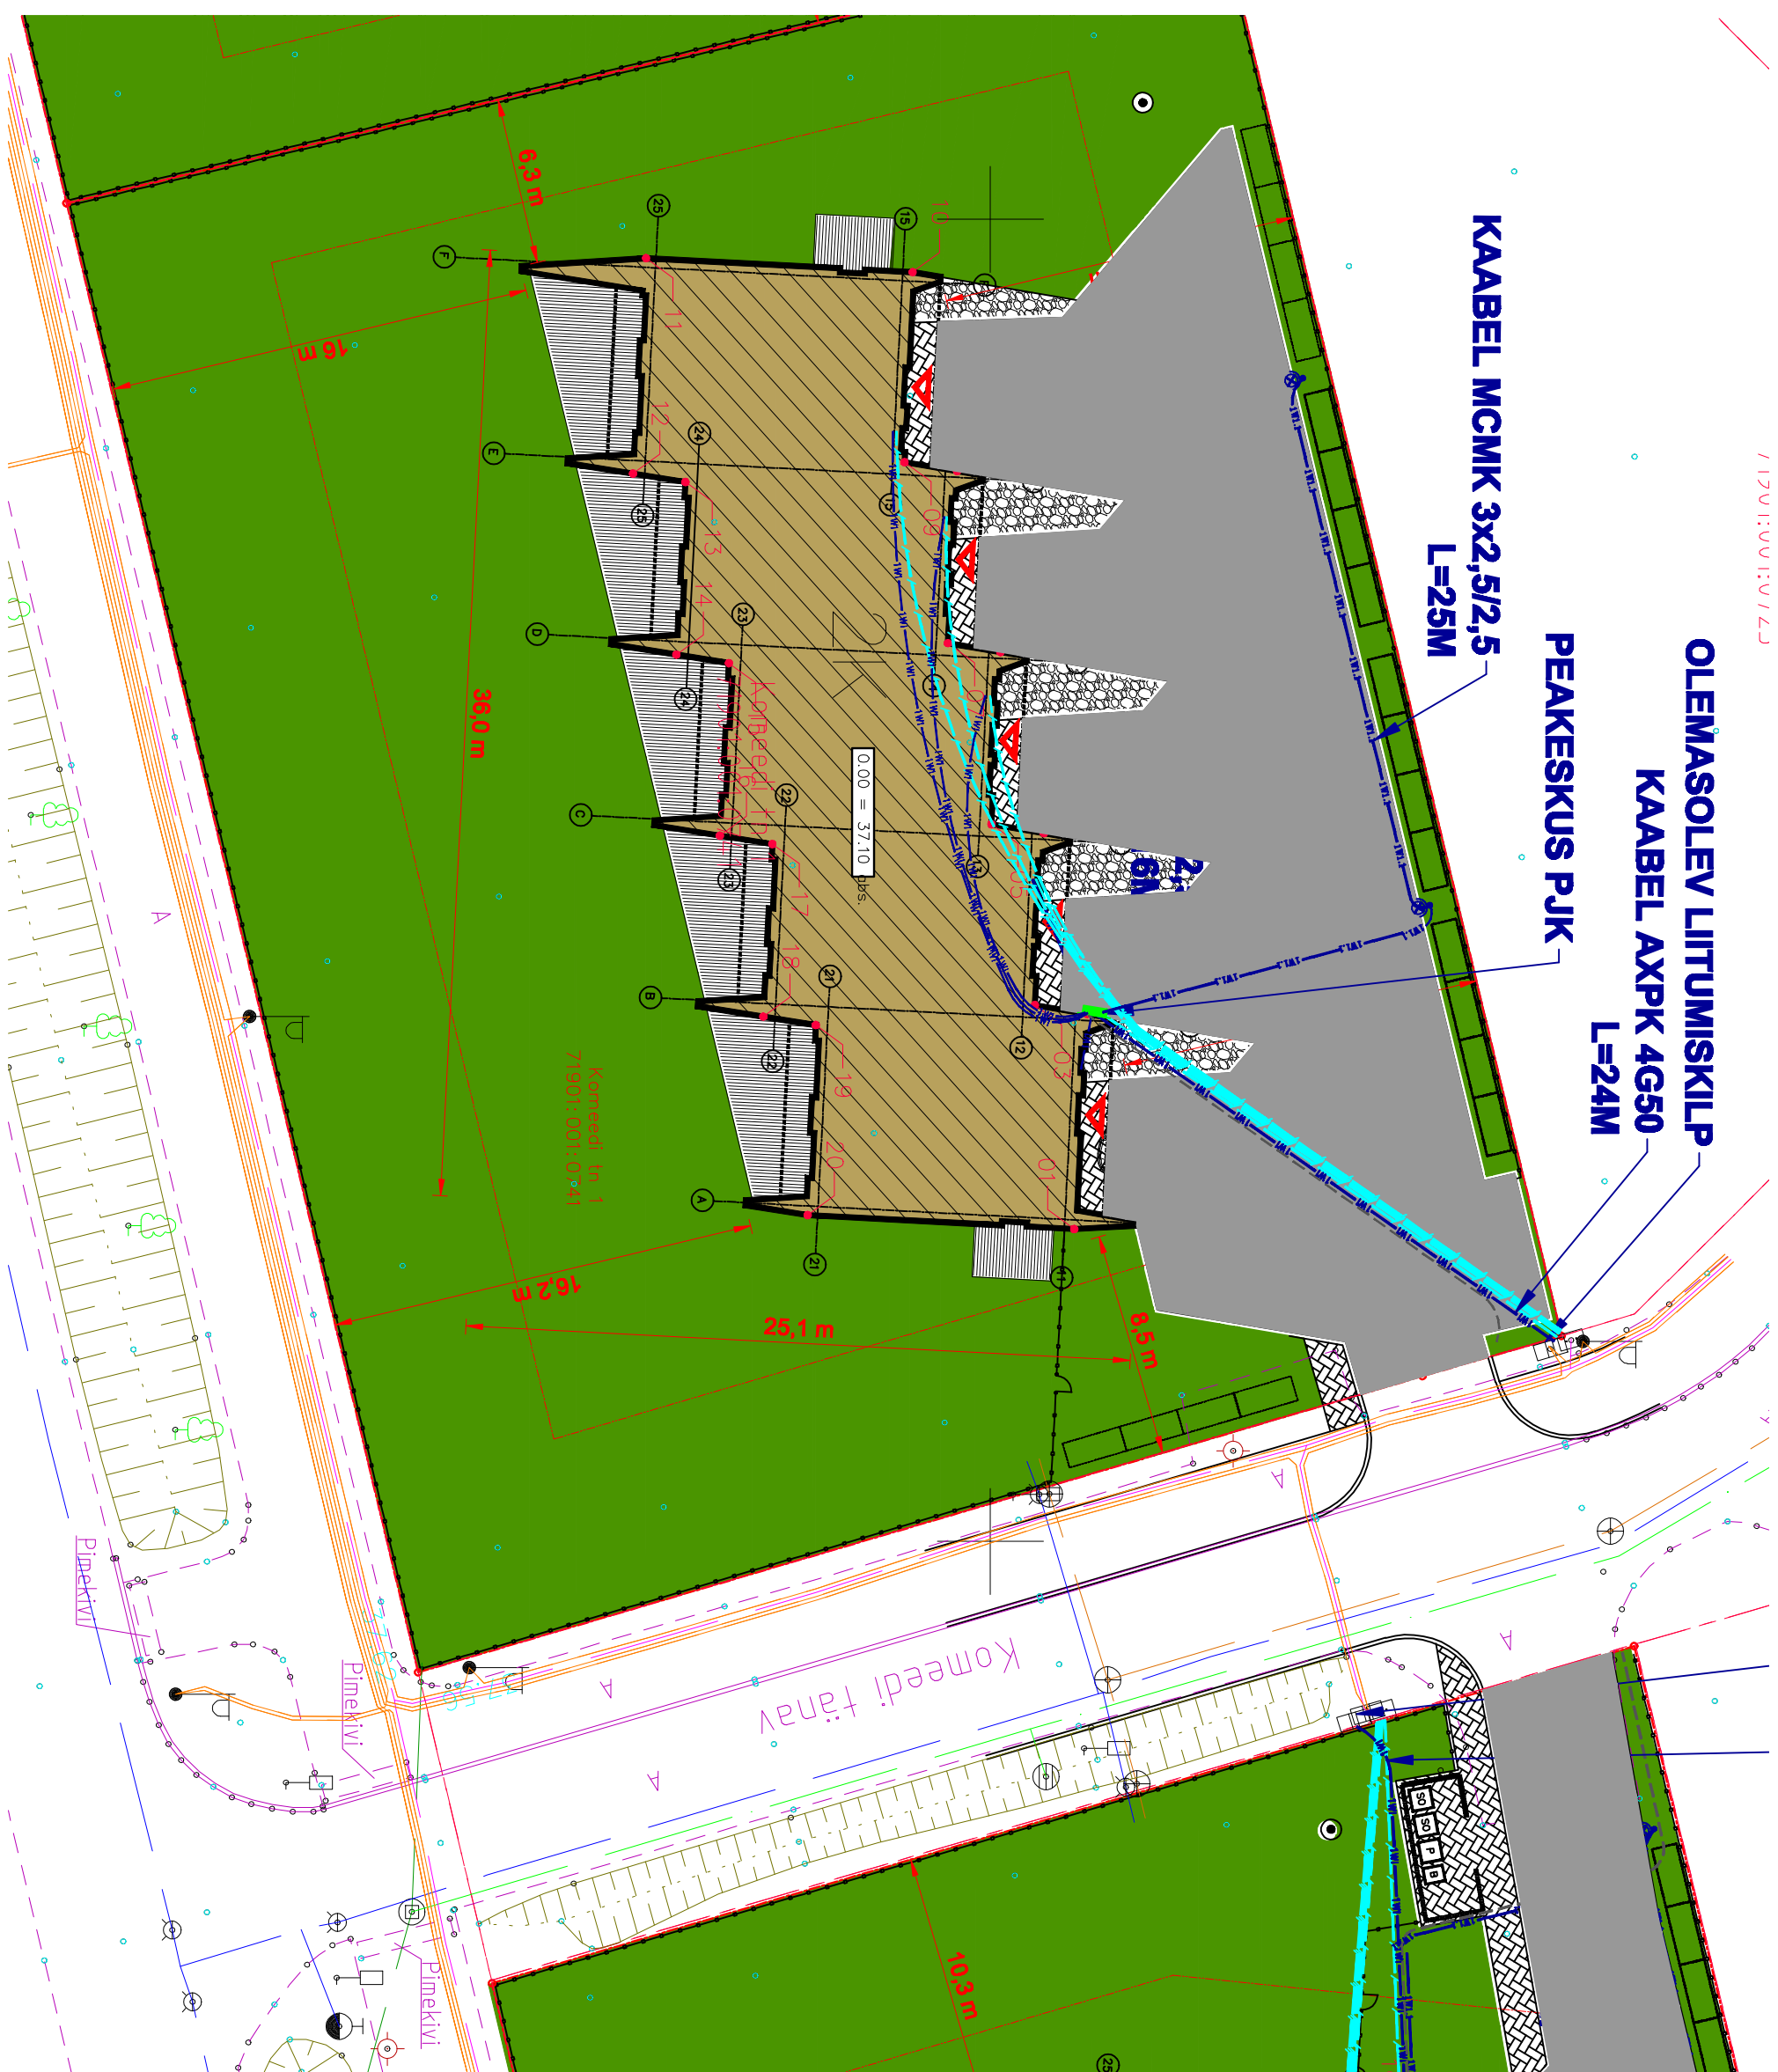

VÄLISPAIGALDISE TINGMÄRGID:


- 








- PROJEKTEENTUD 0,6/1KV, KAABEL MAAS, PLASTORUS d=100mm, 750N
 PROJEKTEENTUD VÄLISVALGUSTUSE 0,6/1KV
 KAABEL MAAS, PLASTORUS d=75mm, 750N
 PROJEKTEENTUD PLASTORU d=50mm, 750N
 OLEMAOLEV LITUMISKILP
 PROJEKTEENTUD VÄLISVALGUSTUSE POSTIL H=4M
 PROJEKTEENTUD SIDEKANALISATSIOONI PLASTORU UPOTEL A d=50mm

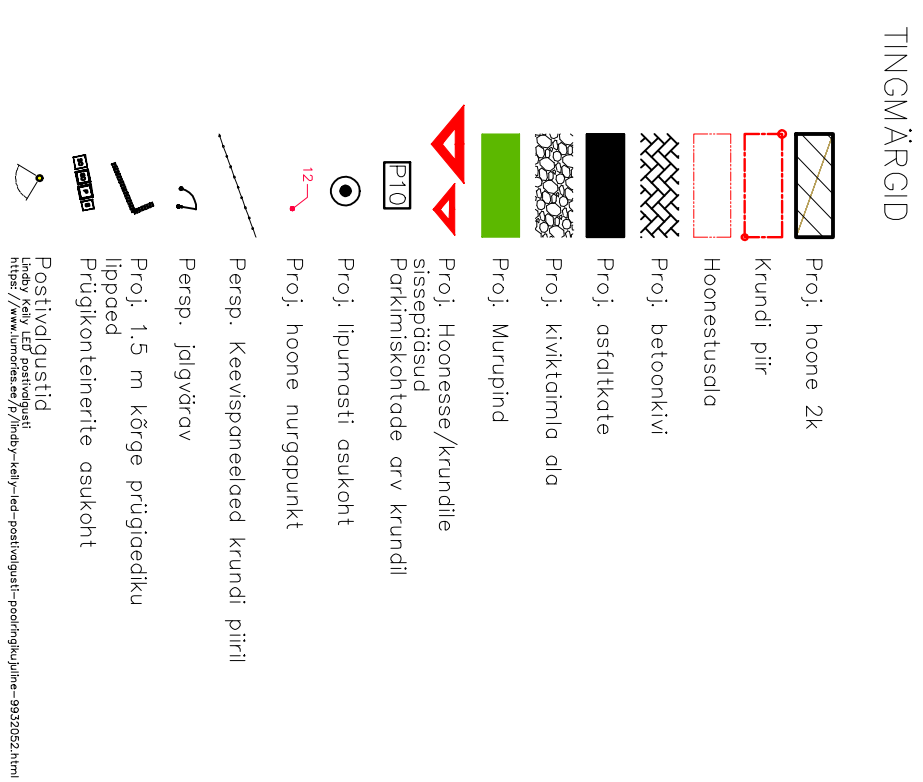

Telliisa		Tööd	
NOBE OÜ		RIDAELAMU ELEKTRIPAALDIS	
Objekt KOMEDI TN 1, SAKU, SAKU VALD, HARJUMA		Töö nr.	2418
Joonis VÄLISPAIGALDISE PLaan			
Projekteeris: V. RANNAKU	Määratus:		Joonis nr. ELV-01
Kontrollis:	Staadium: PÕHIPROJEKT		Leht/lehti: 1/1
Kuupäev: 28.02.2025	Faiil: 2418_PV_ELV-01_v01_Plan		Mõõtkava: 1:500