


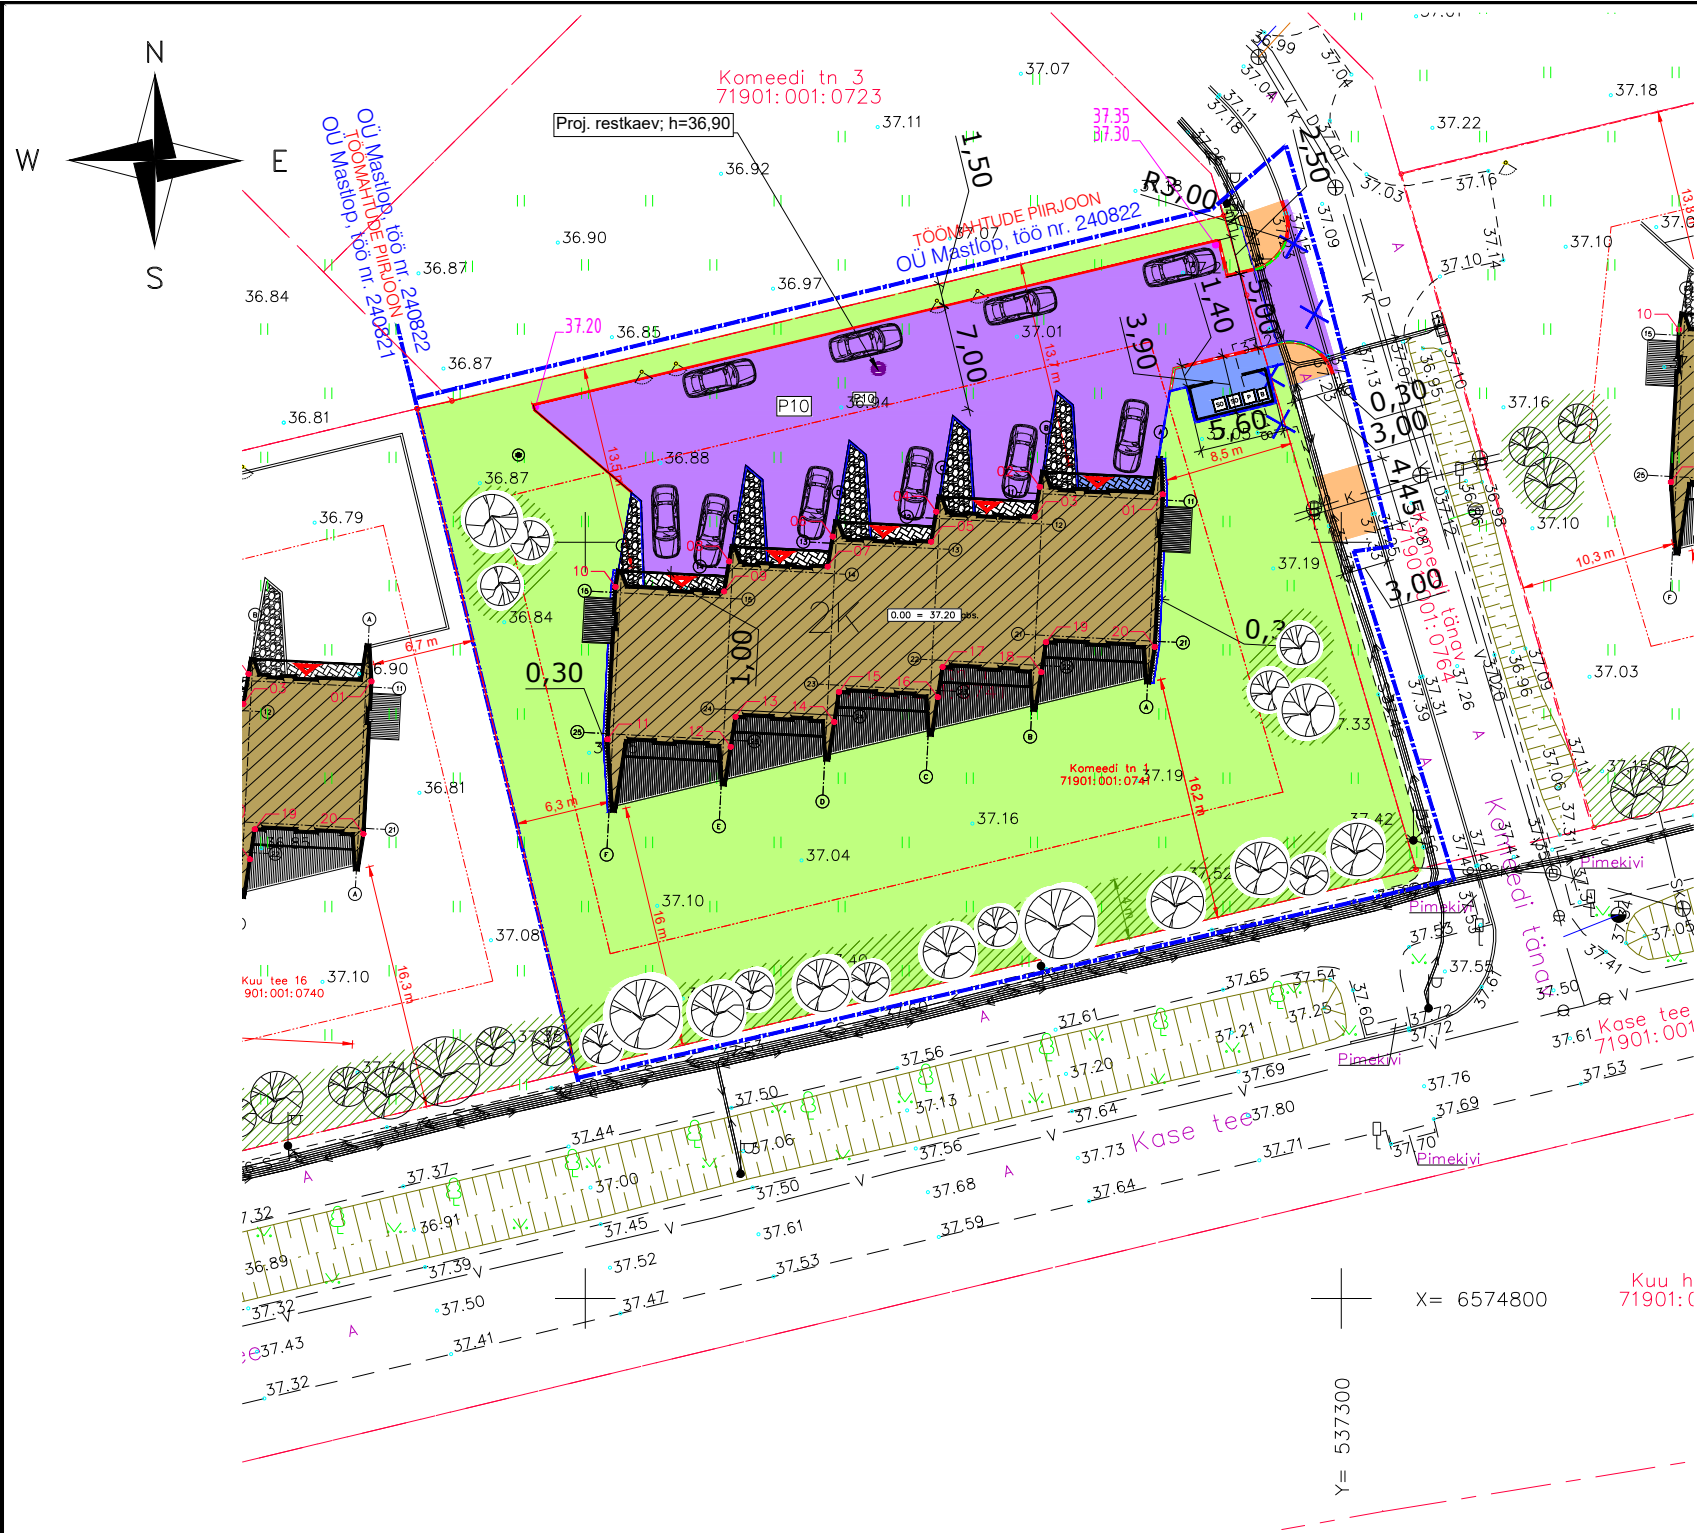

- OÜ Mastlop
TINGMÄRGID**
- OLEMASOLEV KINNISTU PIIR
 - OLEMASOLEV DRENAAZITORUSTIK
 - OLEMASOLEV REDVEEKANALISATSIOONITORUSTIK
 - OLEMASOLEV SADEVEEKANALISATSIOON
 - OLEMASOLEV VEETORUSTIK
 - OLEMASOLEV SIDEKABEL
 - OLEMASOLEV MADALPINGEKABEL
 - OLEMASOLEV NÕLV
 - OLEMASOLEV PUU
 - OLEMASOLEV KAEVUKAAS
 - OLEMASOLEV TV -POST
 - OLEMASOLEV LIKLUSMÄRK
 - OLEMASOLEV EL-KAPP
 - PROJEKTEERTAV SÕIDUTEE KATTE SEEV
 - PROJEKTEERTAV SÕIDUTEE KATTE TAASTAMINE
 - PROJEKTEERTAV KÕNNITEE A/B KATTE TAASTAMINE (Tõrva maa-ala)
 - PROJEKTEERTAV KÕNNITEE BETONKIVIKATE (h=6cm)
 - PROJEKTEERTAV GRANITIKIV SÕELMETEST MÜTSALA
 - PROJEKTEERTAV GRANITISÕELMETEST SOKLI ÄÄRE SILLUTIS
 - PROJEKTEERTAV/TAASTATAV MURUPIND (h=15cm)
 - PROJEKTEERTAV SÕIDUTEE ÄÄREKIVI (80x15x20cm, h=5 cm)
 - PROJEKTEERTAV SÕIDUTEE ÄÄREKIVI (80x15x20cm, h=10 cm)
 - PROJEKTEERTAV KÕNNITEE ÄÄREKIVI (100x8x20cm, h=2 cm)
 - PROJEKTEERTAV PUDUST PEENRAÄRIS
 - TÖÖMAHTUDE PIIRJOON
 - LIKVIDEERTAV ÄÄREKIVI

- Arhitekt111 OÜ, töö nr. KOMEEDI1
TINGMÄRGID
- Proj. hoone 2k
 - Hoonealusala
 - Proj. Murupind
 - Proj. Kõrgharjastus
 - Proj. Hoone/ruundile
sõepõhjad
Parkimisala arv krundil
 - Proj. Iipumasti osukoht
 - Proj. hoone nurgapunkt
 - Proj. 1.5 m kõrgse prüglöödu
ilgpool
Prügliteeliste osukoht
 - Rastivõrgustik
100/150/200/250/300/350/400/450/500/550/600/650/700/750/800/850/900/950/1000

KOMEEDI TN 1 PROJ. HOONE TEHNILISED NÄITAJAD	
KORRUSELUS	1P3
TULEOHUSKLAAS	
NETOPIND	607.2 m²
- sh. korumide pind	344.2 m²
- sh. Tehnapind	13.0 m²
BRUTOPIND	779.6 m²
HOONE MAHT	4951.0 m³
HOONEALINE PIND	379.3 m²
KRUNDI PINDALA	2319.0 m²
KRUNDI TASEMTUSE %	15.1 %
PARKIMISKOHTADE ARV	10

MÄRKUSED:

- 1) Geodeesia koostaja OÜ Radiaan. Teostatud 6.11.2024.a. Töö nr. 2578G24
- 2) Projekteeritud ja olemasolev katend tuleb omavahel kõrguslikult kokku viia
- 3) Kui ol.olevat katendit kahjustatakse suuremas ulatuses kui projektdokumentatsioonis kajastatud, tuleb see normidekohaselt taastada.

Mastlop

OÜ Mastlop

Reg.kood 12618952; EEP003122; ELK000079
Peterburi tee 2F, Tallinn 11415
tel. +372 56 24 26 34, e-mail ppoltsam@gmail.com

Projektijuht	Pärt Põltsam
Projekteeris	Pärt Põltsam
Kontrollis	Pärt Põltsam (tunnistuse nr. 163405/163406)

Koostatud / trükitud: 19.05.2025/ 19.05.2025

Projekti nimetus:	KOMEEDI TN 1 RIDAELAMU TEEDE-EHITUSLIK OSA	Töö nr:	240822
Asukoht:	KOMEEDI TN 1/KOMEEDI TÄNAV SAKU ALEVIK, SAKU VALD, HARJU MK	Leht nr:	TL-02
Tellija:	Saku Arendus OÜ	Staadium:	PÕHIPROJEKT
Joonise nimetus:	ASENDIPLAAN	Mõõtkava:	1:500