
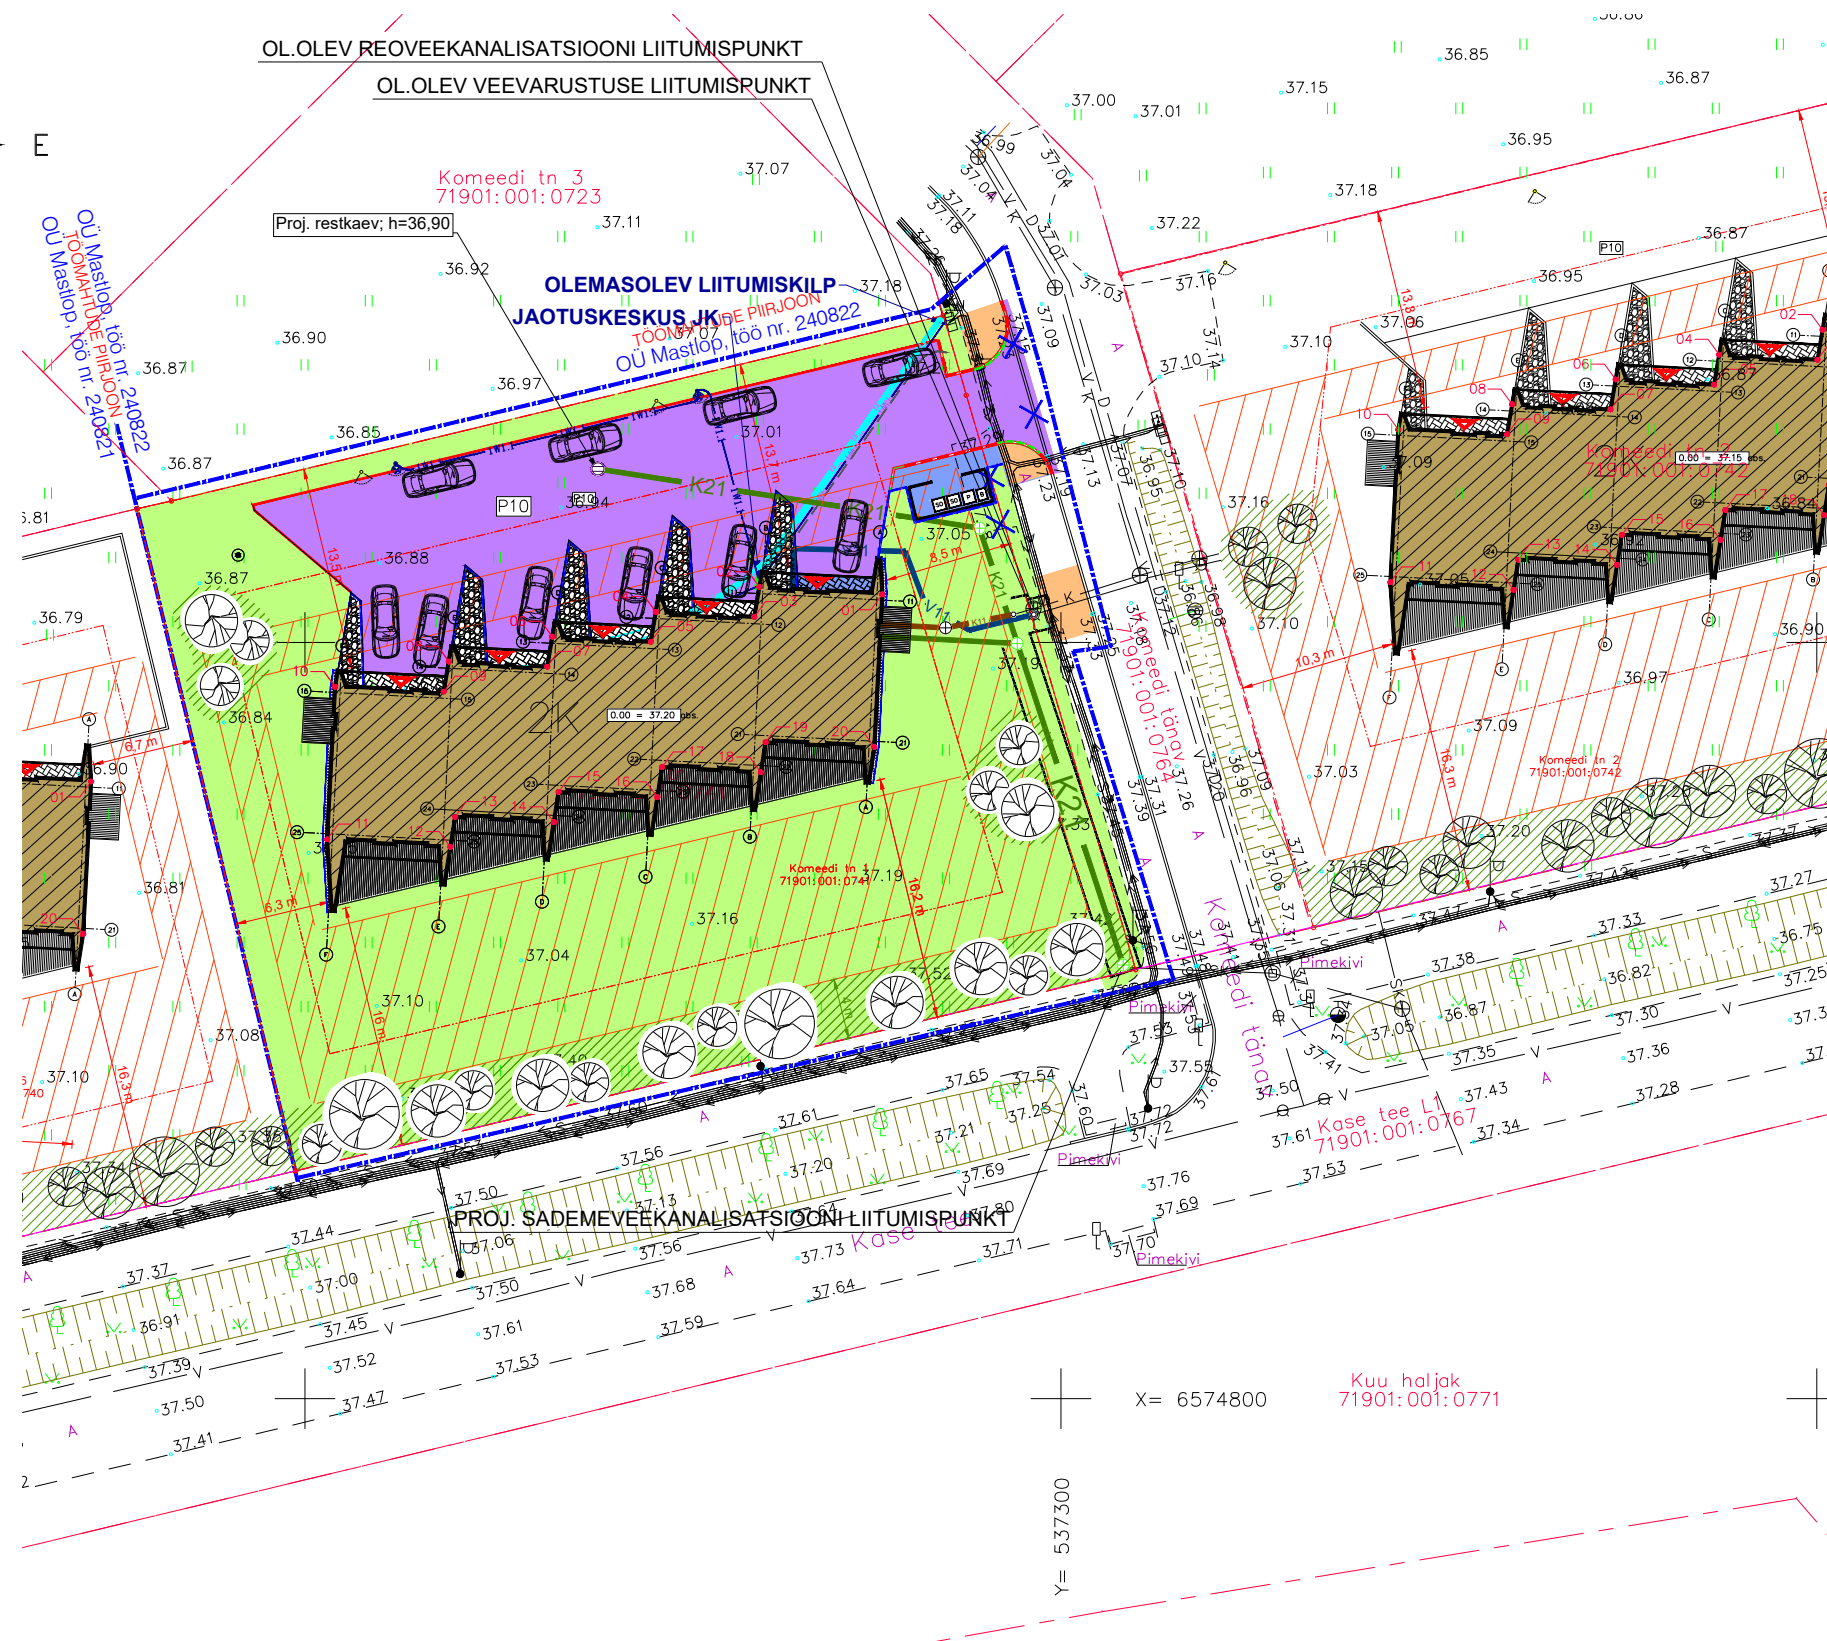


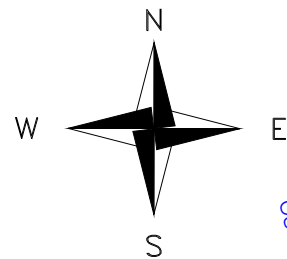

- OÜ Mastlop
TINGMÄRGID**
- OLEMASOLEV KINNISTU PIR
 - OLEMASOLEV DRENAAZITORUSTIK
 - OLEMASOLEV REOVEEKANALISATSIOONITORUSTIK
 - OLEMASOLEV SADEVEEKANALISATSIOON
 - OLEMASOLEV VEETORUSTIK
 - OLEMASOLEV SIDA-KABEL
 - OLEMASOLEV MADALPINGE-KABEL
 - OLEMASOLEV NÖLV
 - OLEMASOLEV PUU
 - OLEMASOLEV KAEVUKAAS
 - OLEMASOLEV TV-POST
 - OLEMASOLEV LIKKUSMÄRK
 - OLEMASOLEV EL-KAPP
 - PROJEKTEERITAV SÖDUTE KATTE SERV
 - PROJEKTEERITAV SÖDUTE A/B KATTE KATTE TAASTAMINE
 - PROJEKTEERITAV KÖNNITEE A/B KATTE TAASTAMINE (Tänavatähega)
 - PROJEKTEERITAV KÖNNITEE BETOONKIVIKATE (h=6cm)
 - PROJEKTEERITAV GRANITKIV SÖLMETEST MULTSALA
 - PROJEKTEERITAV GRANITKIV SÖLMETEST SOKU ÄÄRE SILLUTIS
 - PROJEKTEERITAV TAISTATAV MURUPIND (h=15cm)
 - PROJEKTEERITAV SÖDUTE ÄÄREKIVI (80x15x20cm, h=5 cm)
 - PROJEKTEERITAV SÖDUTE ÄÄREKIVI (80x15x20cm, h=9 cm)
 - PROJEKTEERITAV KÖNNITEE ÄÄREKIVI (100x20cm, h=2 cm)
 - PROJEKTEERITAV PUUDIST PEEHNAAMIS
 - TÖÖMAHTUDE PIIRJOON
 - KAEVUKU SERV
 - LIKKIDEERITAV ÄÄREKIVI
 - MAAKÜTTEKONTUUR PÕHIMÖTTELINE ASUKOHT (Projekti koostaja KVKV Projekt OÜ)

- Arhitekt11 OÜ, töö nr. KOMEEDI1
TINGMÄRGID**
- Proj. hoone 2k
 - Hooneasutuse
 - Proj. Murupind
 - Proj. Kõrgalajustus
 - Proj. Hoone/kruvide asukoht
 - Parkimispaikade arv kruntil
 - Proj. Ipmastis asukoht
 - Proj. hoone nurgapunkt
 - Proj. 1.5 m kõrge prüglaseku liigend
 - Puugkanalite asukoht
 - Puugkanalid
 - 1000 mm kõrgune kaitse sein

**TINGMÄRGID
(SMART PIPES OÜ töö nr 24060)**

- V11 PROJEKTEERITUD KINNISTU VEETORUSTIK
- K11 PROJEKTEERITUD KINNISTU REOVEEKANALISATSIOONITORUSTIK
- K21 PROJEKTEERITUD KINNISTU SADEMEVEEKANALISATSIOONITORUSTIK

VIVALIGHT OÜ, töö nr 2417, VÄLISPAIGALDISE TINGMÄRGID:

- PROJEKTEERITUD 0,6/1kV KAABEL MAAS, PLASTTORUS d=100mm, 750N
- PROJEKTEERITUD VÄLISVALGUSTUSE 0,6/1kV KAABEL MAAS, PLASTTORUS UPOTEL A d=75mm, 750N
- PROJEKTEERITUD PLASTTORU UPOTEL A d=50mm, 750N
- OLEMASOLEV LIITUMISKILP
- PROJEKTEERITUD VÄLISVALGUSTI VÄLISVALGUSTUSE POSTIL H=4 M
- PROJEKTEERITUD SIDA-KANALISATSIOONI PLASTTORU UPOTEL A d=50mm

X= 6574800

Y= 537300

Mastlop OÜ Mastlop Reg.kood 12618952; EEP003122; ELK000079 Peterburi tee 2F, Tallinn 11415 tel. +372 56 24 26 34, e-mail ppoltsam@gmail.com		Projekti nimetus:	KOMEEDI TN 1 RIDAELAMU TEEDE-EHITUSLIK OSA	Töö nr:	240822
		Asukoht:	KOMEEDI TN 1/KOMEEDI TÄNAV SAKU ALEVIK, SAKU VALD, HARJU MK	Leht nr:	TL-04
		Tellija:	Saku Arendus OÜ	Staadium:	PÕHIPROJEKT
		Joonise nimetus:	TEHNOVÕRKUDE KOONDPLAAN	Mõõtkava:	1:500
Projektijuht	Pärt Põltsam	Koostatud / trükitud: 19.05.2025/ 19.05.2025			
Projekteeris	Pärt Põltsam				
Kontrollis	Pärt Põltsam (tunnistuse nr. 163405/163406)				

MÄRKUSED:

- Geodeesia koostaja OÜ Radiaan. Teostatud 6.11.2024.a. Töö nr. 2578G24
- Projekteeritud ja olemasolev katend tuleb omavahel kõrguslikult kokku viia
- Kui ol.olevat katendit kahjustatakse suuremas ulatuses kui projektdokumentatsioonis kajastatud, tuleb see normidekohaselt taastada.