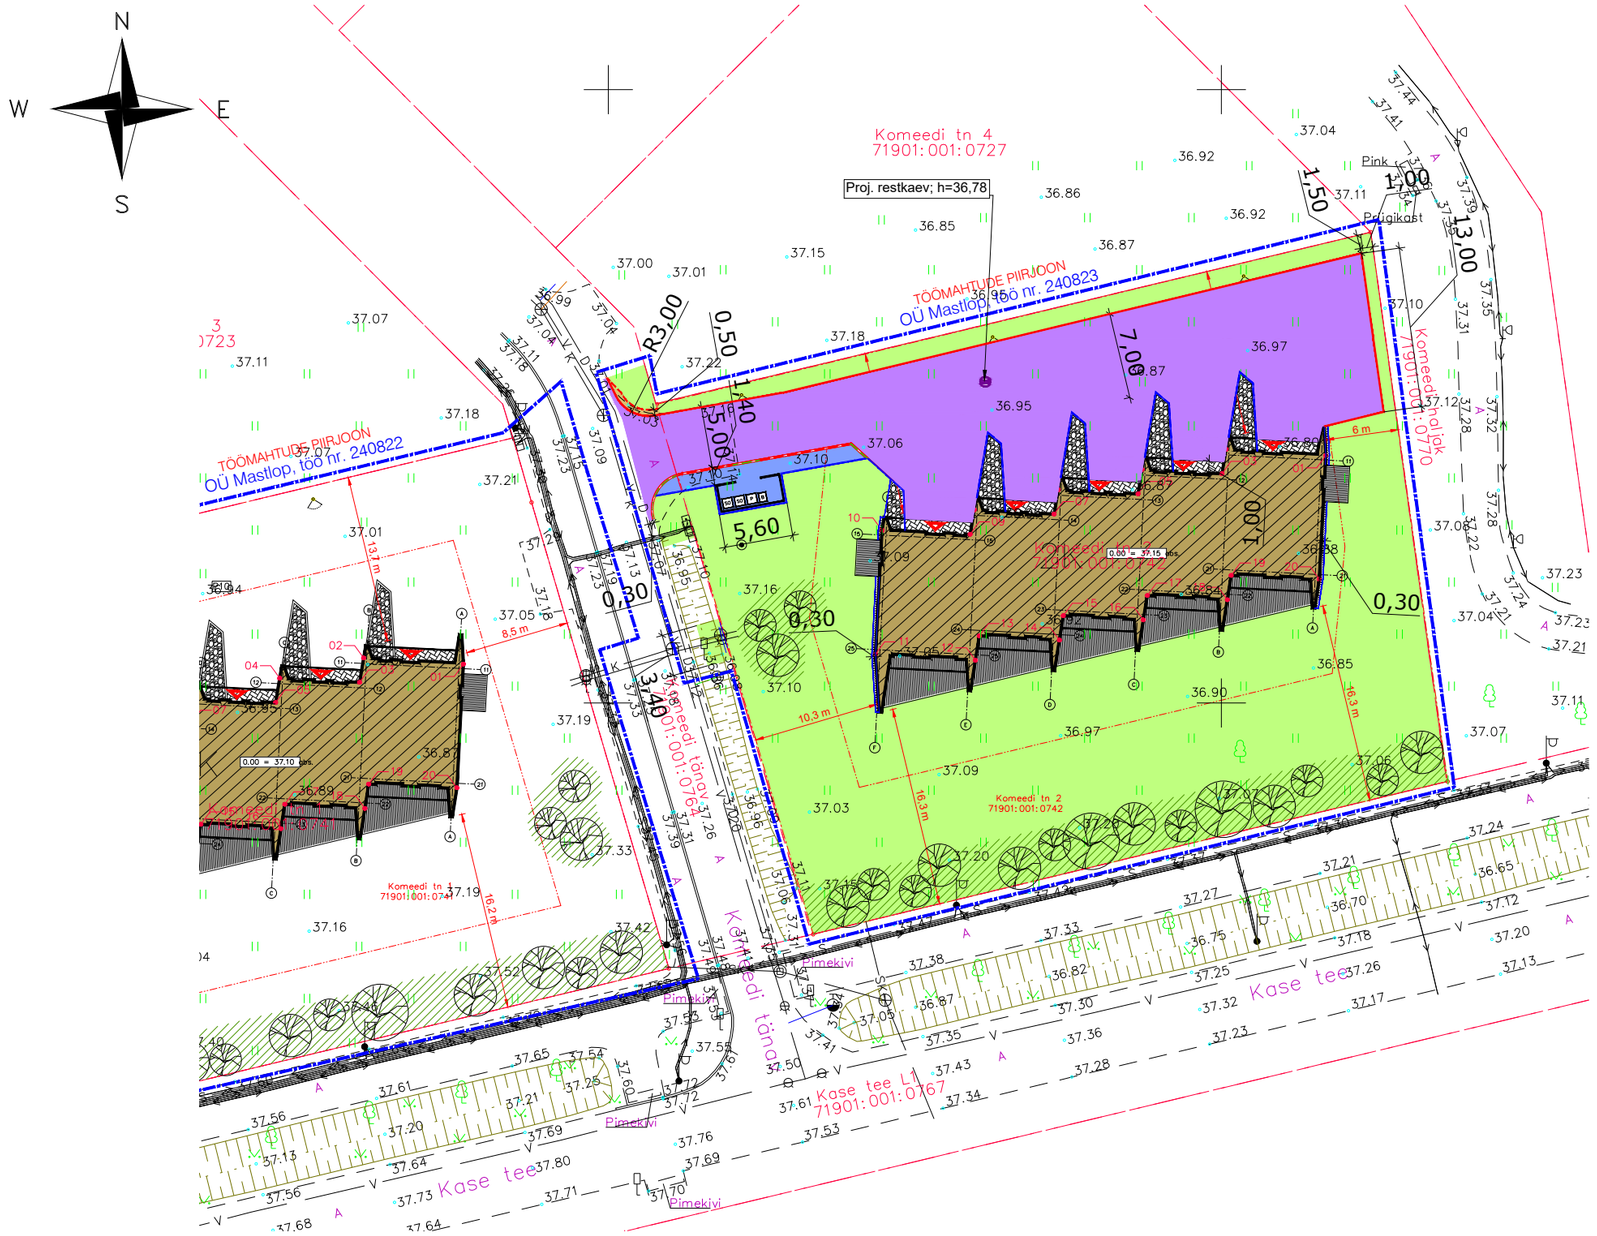

OÜ Mastlop

TINGMÄRGID

- OLEMASOLEV KINNISTU PIIR
- OLEMASOLEV DRENAAZITORUSTIK
- OLEMASOLEV REOVEEKANALISATSIOONITORUSTIK
- OLEMASOLEV SADEVEEKANALISATSIOON
- OLEMASOLEV VEETORUSTIK
- OLEMASOLEV SIDEKAABEL
- OLEMASOLEV MADALPINGEKAABEL
- OLEMASOLEV NÕLV
- OLEMASOLEV PUU
- OLEMASOLEV KAEVUKAAS
- OLEMASOLEV TV -POST
- OLEMASOLEV LIIKLUSMÄRK
- OLEMASOLEV EL KAPP
- PROJEKTEERITAV SÕIDUTEE KATTE SERV
- PROJEKTEERITAV SÕIDUTEE PEENRA SERV
- PROJEKTEERITAV SÕIDUTEE A/B KATE/ KATTE TAASTAMINE
- PROJEKTEERITAV KÕNNITEE BETOONKIVIKATE (h=6cm)
- PROJEKTEERITAV PARKLA BETOONKIVIKATE (h=8cm)
- PROJEKTEERITAV GRANIITKIVI SÕELMETEST MULTŠALA
- PROJEKTEERITAV GRANIITSÕELMETEST SOKLI ÄÄRE SILLUTIS
- PROJEKTEERITAV KRUUSAST TEEPEENAR
- PROJEKTEERITAV/TAASTATAV MURUPIND (h=15cm)
- PROJEKTEERITAV SÕIDUTEE ÄÄREKIVI (80x15x29cm, h=5 cm)
- PROJEKTEERITAV SÕIDUTEE ÄÄREKIVI (80x15x29cm, h=0 cm)
- PROJEKTEERITAV KÕNNITEE ÄÄREKIVI (100x8x20cm, h=2 cm)
- PROJEKTEERITAV PUDUST PEENRAÄÄRIS
- TÖÖMAHTUDE PIIRJOON
- LIKVIDEERITAV ÄÄREKIVI

Arhitekt11 OÜ, töö nr. KOMEEDI2

TINGMÄRGID

- Proj. hoone 2k
- Hoonestusala
- Proj. Murupind
- Proj. Kõrghaljastus
- Proj. Hoonesse/krundile sisse/sõidud Parkimiskohtade arv krundil
- Proj. tipumasti asukoht
- Proj. hoone nurgapunkt
- Proj. 1,5 m kõrge prügiaedku lipsaed Prügikonteinerite asukoht
- Postivalgustid

KOMEEDI TN 2
PROJ. HOONE TEHNILISED NÄITAJAD

KORRUSELISUS	2
TULEPÜSIVUSKLASS	TP3
NETOPIND	607.2 m²
– sh. õuruumide pind	594.2 m²
– s.h. Tehnopind	13.0 m²
BRUTOPIND	779.6 m²
HOONE MAHT	4951.0 m³
HOONEALUNE PIND	379.3 m²
KRUNDI PINDALA	2548.0 m²
KRUNDI TÄISEHITUSE %	14.9 %
PARKIMISKOHTADE ARV	10

MÄRKUSED:

1) Geodeesia koostaja OÜ Radiaan. Teostatud 6.11.2024.a. Töö nr. 2578G24
2) Projekteeritud ja olemasolev katend tuleb omavahel kõrguslikult kokku viia
3) Kui ol.olevat katendit kahjustatakse suuremas ulatuses kui projektdokumentatsioonis kajastatud, tuleb see normidekohaselt taastada.

OÜ Mastlop
Reg.kood 12618952; EEP003122; ELK000079
Peterburi tee 2F, Tallinn 11415
tel. +372 56 24 26 34, e-mail ppoltsam@gmail.com

Projektijuht	Pärt Põltsam
Projekteeris	Pärt Põltsam
Kontrollis	Pärt Põltsam (tunnistuse nr. 163405/163406)
Koostatud / trükitud:	19.05.2025/ 19.05.2025

Projekti nimetus:
KOMEEDI TN 2 RIDAELAMU
TEEDE-EHITUSLIK OSA

Asukoht:
KOMEEDI TN 2/KOMEEDI TÄNAV
SAKU ALEVIK, SAKU VALD, HARJU MK

Tellija:
Saku Arendus OÜ

Joonise nimetus:
ASENDIPLAAN

Töö nr: 240823
Leht nr: TL-02
Staadium: PÕHIPROJEKT
Mõõtkava: 1:500