


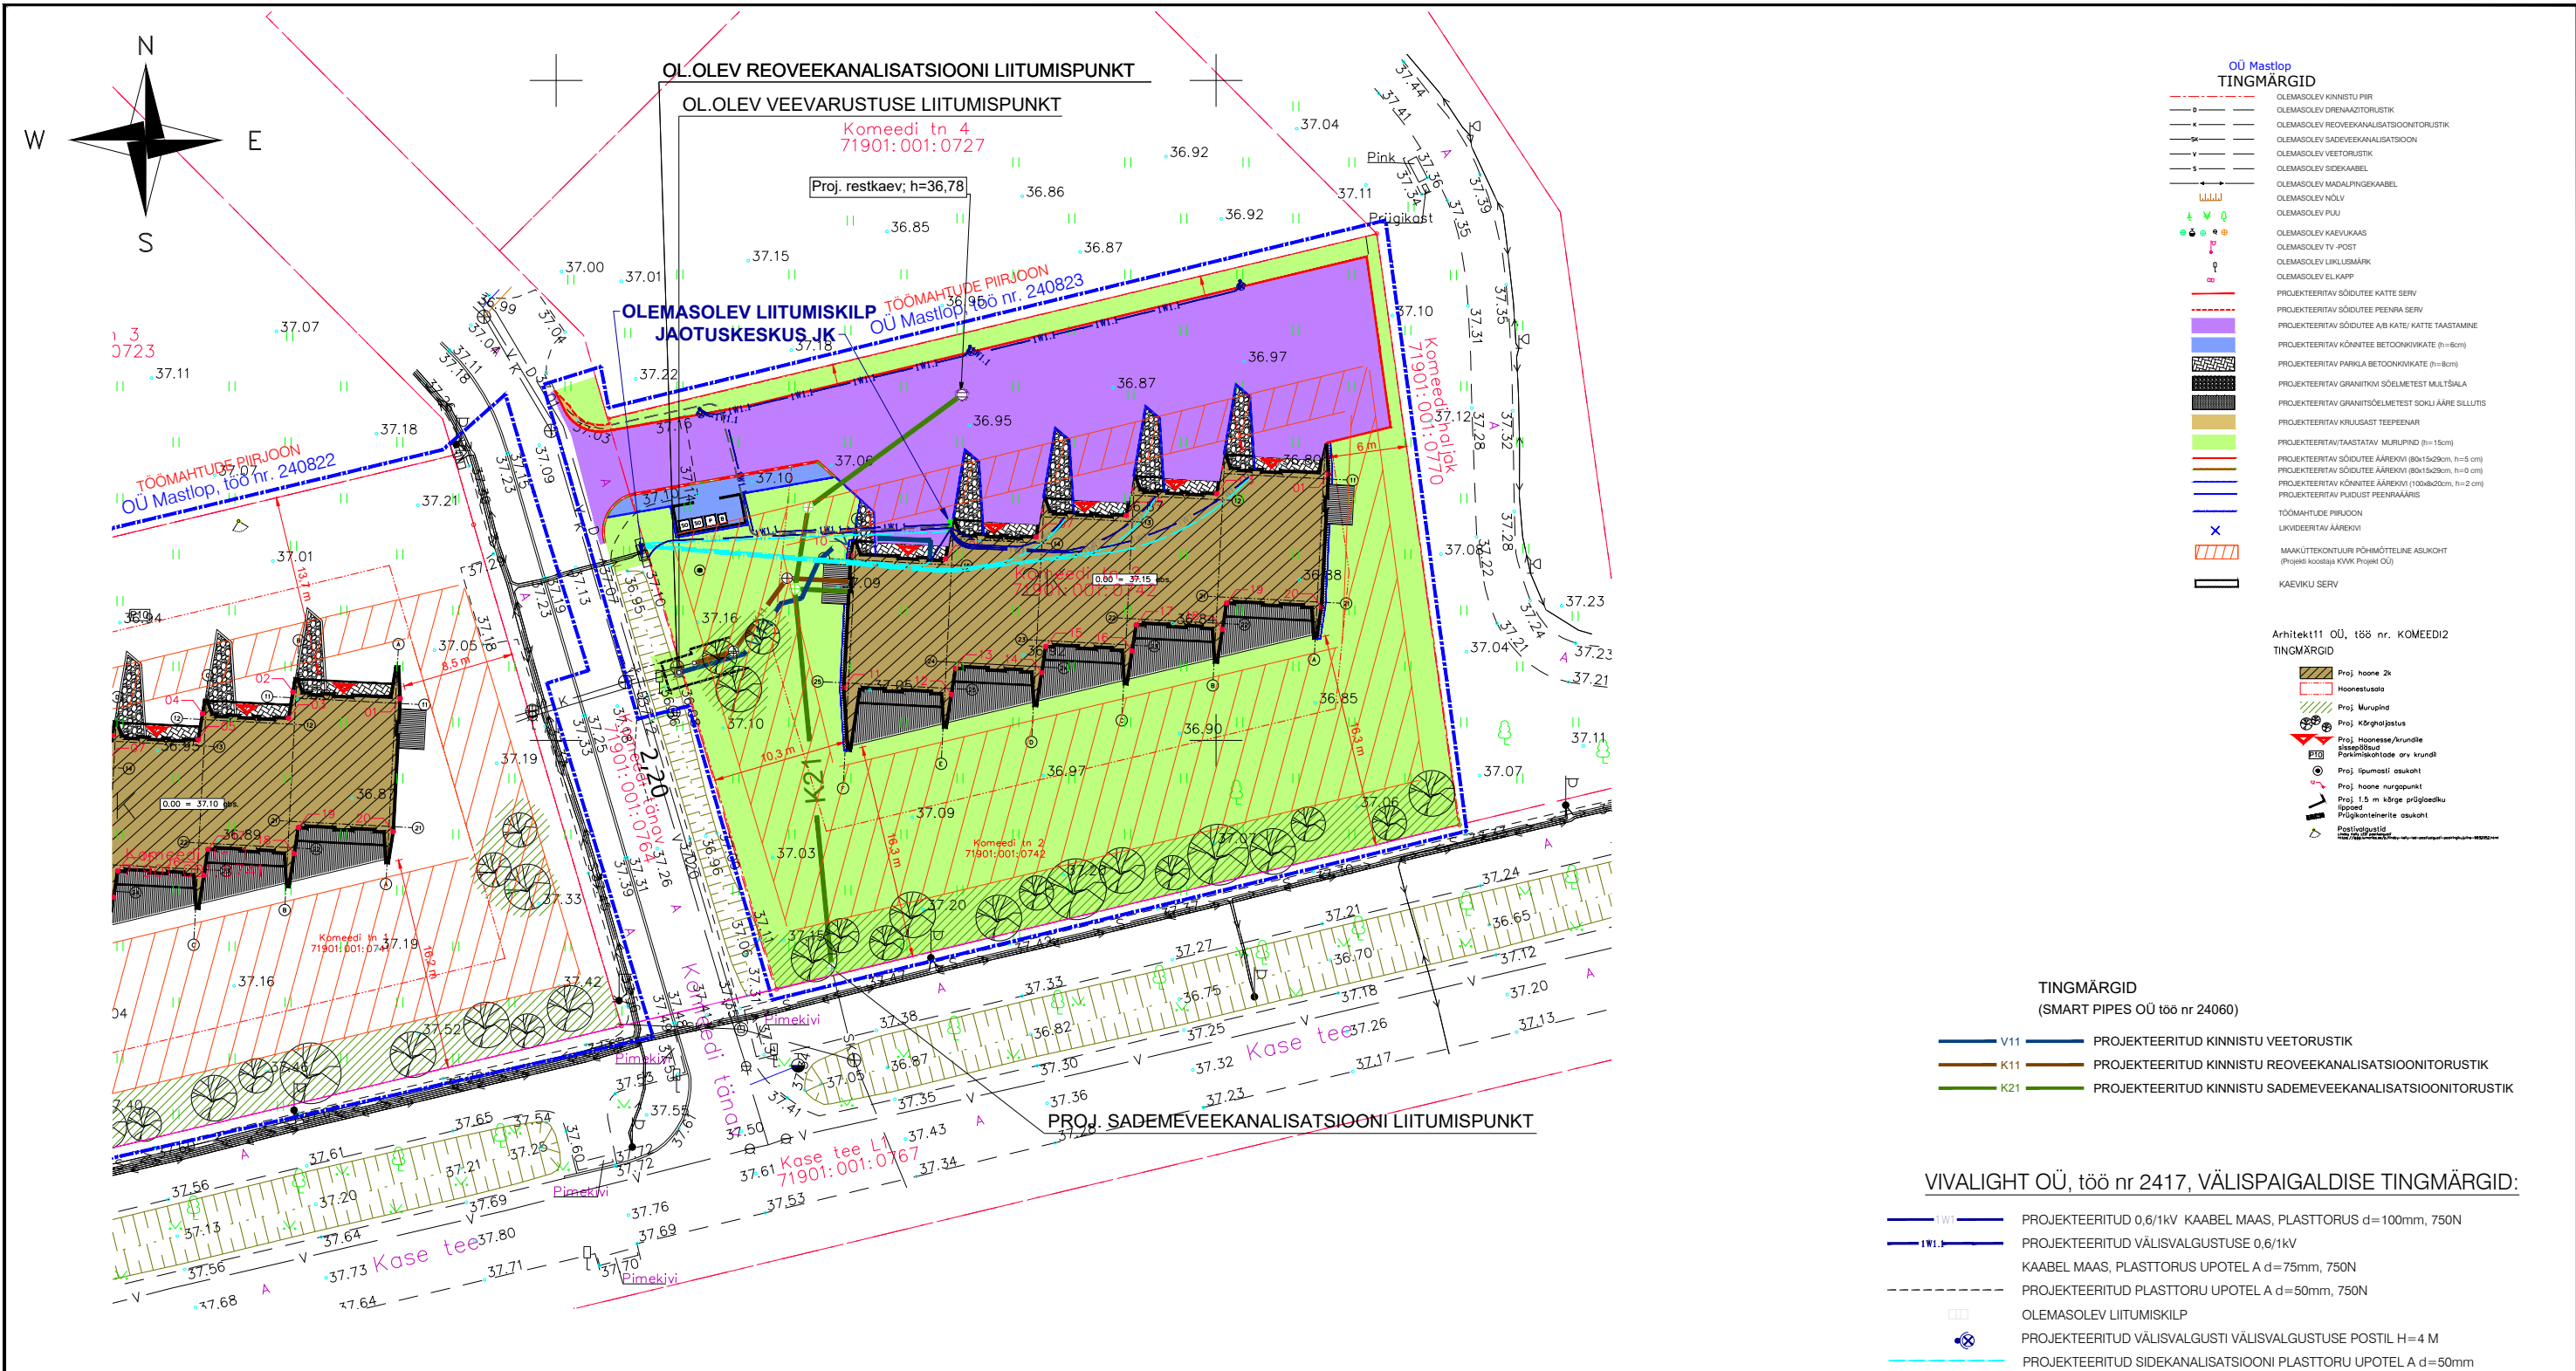

MÄRKUSED:

- 1) Geodeesia koostaja OÜ Radiaan. Teostatud 6.11.2024.a. Töö nr. 2578G24
- 2) Projekteeritud ja olemasolev katend tuleb omavahel kõrguslikult kokku viia
- 3) Kui ol.olevat katendit kahjustatakse suuremas ulatuses kui projektdokumentatsioonis kajastatud, tuleb see normidekohaselt taastada.

Mastlop OÜ Mastlop Reg.kood 12618952; EEP003122; ELK000079 Peterburi tee 2F, Tallinn 11415 tel. +372 56 24 26 34, e-mail ppoltsam@gmail.com		Projekti nimetus:	KOMEEDI TN 2 RIDAELAMU TEEDE-EHITUSLIK OSA	Töö nr: 240823
		Asukoht:	KOMEEDI TN 2/KOMEEDI TÄNAV SAKU ALEVIK, SAKU VALD, HARJU MK	Leht nr: TL-04
		Tellijä:	Saku Arendus OÜ	Staadium: PÕHIPROJEKT
		Joonise nimetus:	TEHNOVÕRKUDE KOONDPLAAN	Mõõtkava: 1:500
Projektijuht	Pärt Põltsam			
Projekteeris	Pärt Põltsam			
Kontrollis	Pärt Põltsam (tunnistuse nr. 163405/163406)			
Koostatud / trükitud:19.05.2025/ 19.05.2025				